Project Schedule(Level 3)

Activity ID	Activity Name	Start	Finish
Project Schedule(Level 3)		2026-02-15	2030-08-15
Main Mile Stone		2026-02-15	2030-08-15
MS1010	Commencement Date	2026-02-15*	
MS1020	Site Handover for 1 hectares in zones A1 for cast in-situ pile test		2026-04-30
MS1030	Site Handover for zones A1		2026-07-15
MS1040	Site Handover for zones A2		2026-08-15
MS1050	Site Handover for zones A3		2026-10-15
MS1060	Site Handover for zones B		2026-12-15
MS1070	Site Handover for zones C		2027-01-15
MS1080	Site Handover for zones D		2027-03-15
MS1090	Site Handover for zones E		2027-04-15
MS1100	Site Handover for zones F		2027-05-15
MS1110	1st Batch of Contractor Personnel Mobilize on Site	2026-06-01	
MS1120	First Pile Date	2026-10-15	
MS1130	Tempoary 10kV Power for Cathode Sealing by the Employer	2027-08-15*	
MS1140	Power Plant Available for Phase 1A Pre-Operating Tests	2028-08-15*	
MS1150	Power Plant Available for Phase 1B Pre-Operating Tests		2029-07-15
MS1160	First Baked Anode of Phase 1A		2029-05-15
MS1170	First Baked Anode of Phase 1B		2029-11-15
MS1180	Mechanical Completion Date of Phase 1A		2029-03-15
MS1190	First Metal of Phase 1A (0.5 MMTPA)		2029-04-15
MS1200	Last Metal of Phase 1A (0.5 MMTPA)		2029-11-15
MS1210	Mechanical Completion Date of Phase 1B		2030-02-05
MS1220	First Metal of Phase 1B (0.5 MMTPA)		2030-02-15
MS1230	Last Metal of Phase 1B (0.5 MMTPA)		2030-08-15
Detailed Engineering Design		2026-02-15	2027-03-08
E00 External Engineering Works Outside Plant Fence		2026-07-08	2026-12-06
E01 Raw Material Conveying system		2026-07-08	2026-12-06
DD1010	Pile diagram	2026-07-08	2026-09-06
DD1020	Issue pile drawing	2026-10-05	2026-10-05
DD1030	Other professional drawings	2026-07-08	2026-11-05
DD1040	Issue DED drawing	2026-12-06	2026-12-06
S00 Aluminum Reduction Plant		2026-02-15	2027-01-15
S01 Potroom		2026-02-15	2026-06-14
DD1050	Pile diagram	2026-02-15	2026-04-24
DD1060	Issue pile drawing	2026-05-23	2026-05-23
DD1070	Other professional drawings	2026-02-15	2026-05-14
DD1080	Issue DED drawing	2026-06-14	2026-06-14
S02 Potline Gas Treatment Center		2026-05-25	2026-10-14
DD1090	Pile diagram	2026-05-25	2026-07-24
DD1100	Issue pile drawing	2026-08-29	2026-08-29
DD1110	Other professional drawings	2026-05-25	2026-09-13
DD1120	Issue DED drawing	2026-10-14	2026-10-14
S03 Alumina Storage		2026-06-05	2026-11-03
DD1130	Pile diagram	2026-06-05	2026-08-04
DD1140	Issue pile drawing	2026-09-02	2026-09-02
DD1150	Other professional drawings	2026-06-05	2026-10-03
DD1160	Issue DED drawing	2026-11-03	2026-11-03
S04 Alumina Conveying and Daly Silo		2026-06-10	2026-10-29
DD1170	Pile diagram	2026-06-10	2026-08-04
DD1180	Issue pile drawing	2026-09-02	2026-09-02
DD1190	Other professional drawings	2026-06-10	2026-09-28
DD1200	Issue DED drawing	2026-10-29	2026-10-29
S05 Fluoride Storage		2026-05-25	2026-09-11
DD1210	Pile diagram	2026-05-25	2026-07-09
DD1220	Issue pile drawing	2026-08-07	2026-08-07
DD1230	Other professional drawings	2026-05-25	2026-08-11
DD1240	Issue DED drawing	2026-09-11	2026-09-11
S06 Super Dense Phase Conveying System		2026-05-10	2026-08-27
DD1250	Pile diagram	2026-05-10	2026-06-24
DD1260	Issue pile drawing	2026-07-23	2026-07-23
DD1270	Other professional drawings	2026-05-10	2026-07-27
DD1280	Issue DED drawing	2026-08-27	2026-08-27
S07 Anode Covering Material Storage & Conveying System		2026-04-10	2026-07-28
DD1290	Pile diagram	2026-04-10	2026-05-25
DD1300	Issue pile drawing	2026-06-23	2026-06-23
DD1310	Other professional drawings	2026-04-10	2026-06-27
DD1320	Issue DED drawing	2026-07-28	2026-07-28
S08 Cast House		2026-06-28	2026-12-21
DD1330	Pile diagram	2026-06-28	2026-10-06
DD1340	Issue pile drawing	2026-11-04	2026-11-04
DD1350	Other professional drawings	2026-06-28	2026-11-20
DD1360	Issue DED drawing	2026-12-21	2026-12-21

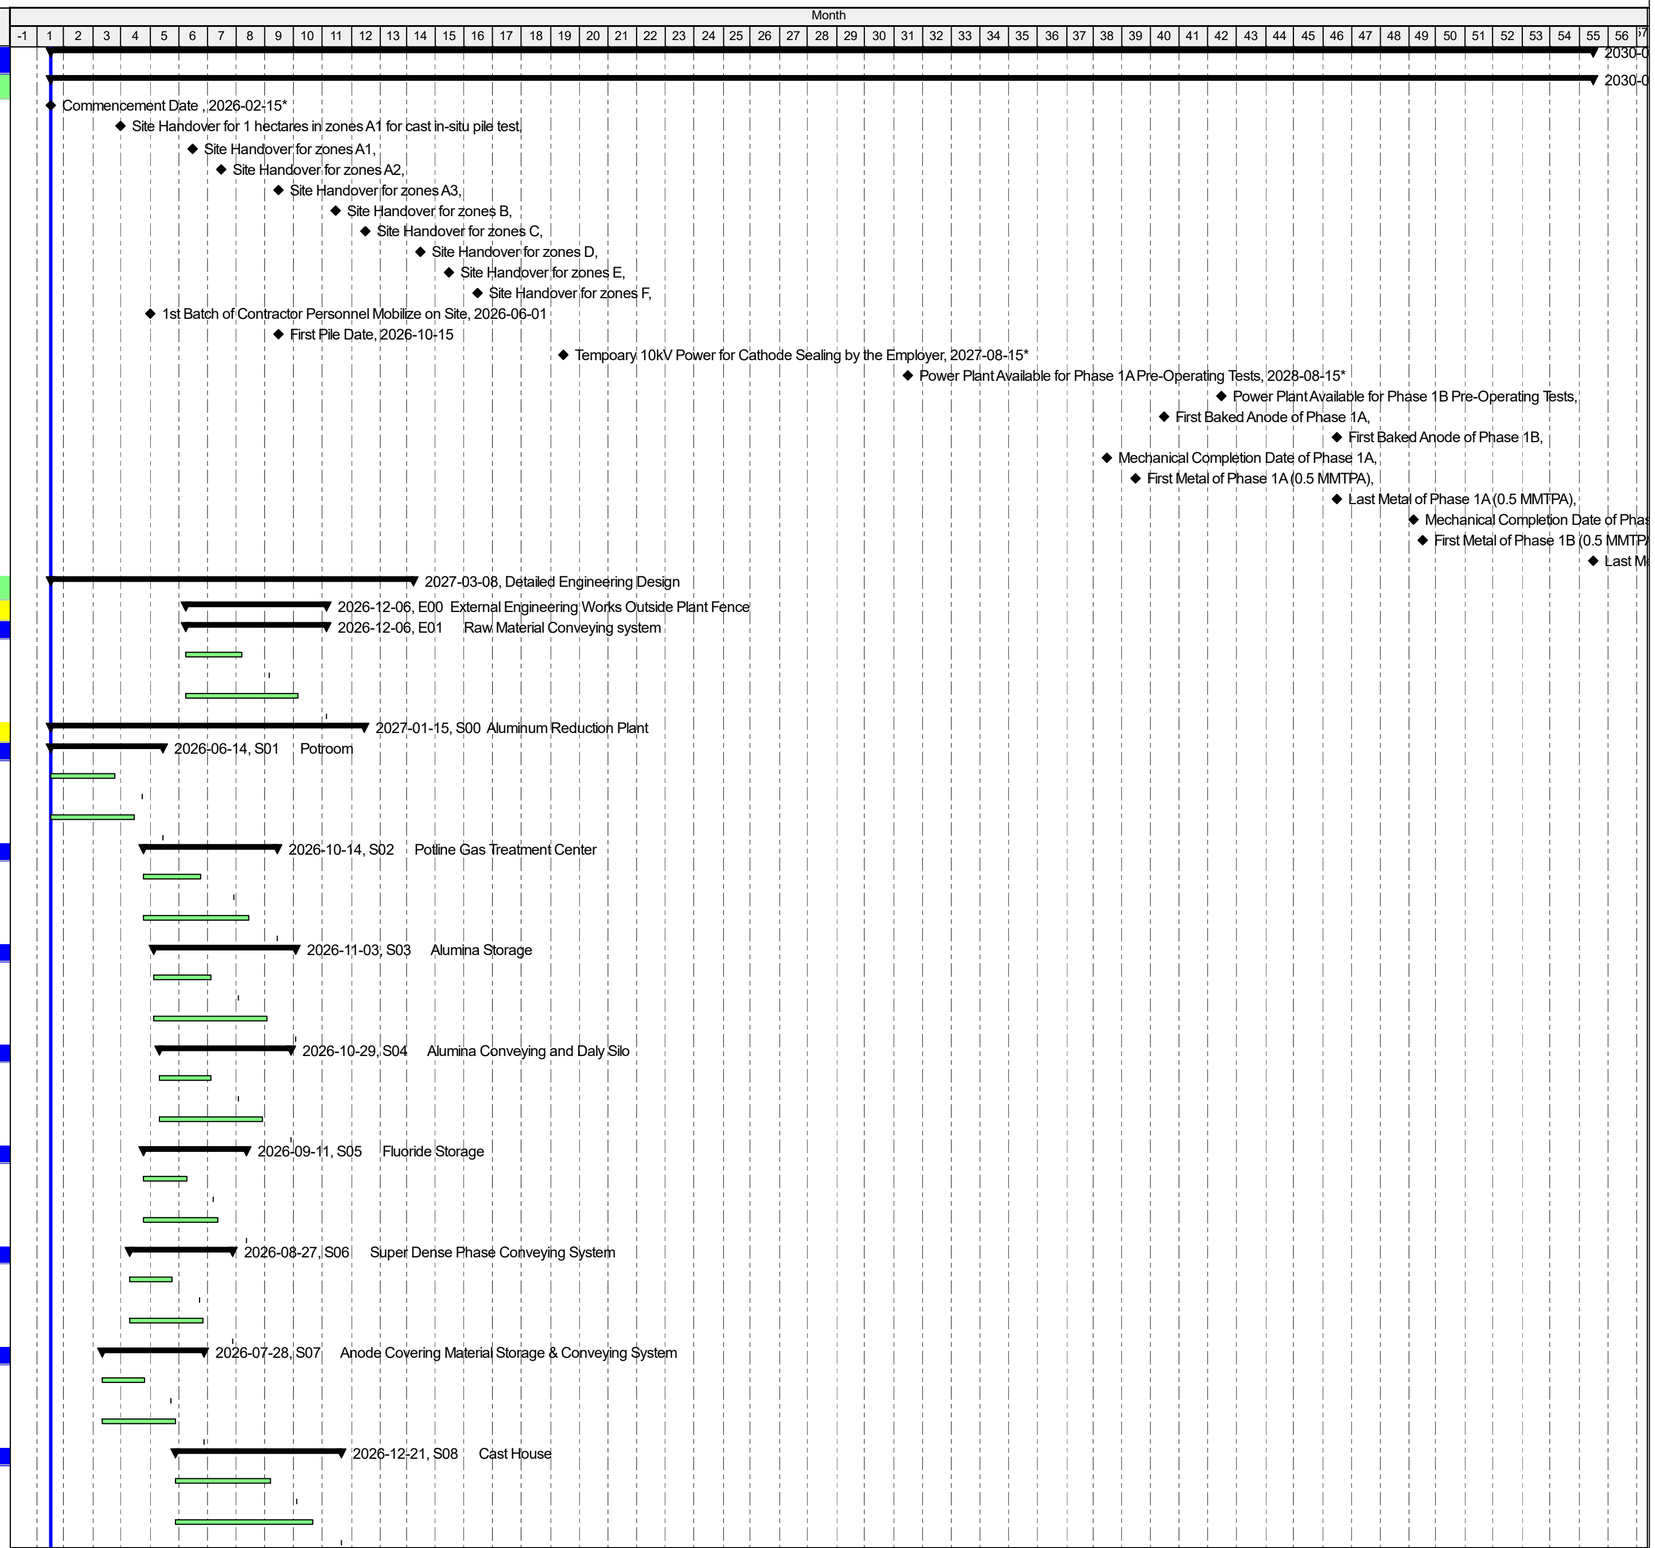

Remaining Level of Effort | Actual Work | Critical Remaining Work | summary
Actual Level of Effort | Remaining Work | Milestone

Project Schedule(Level 3)

Activity ID	Activity Name	Start	Finish
S09	Crucible Cleaning Workshop	2026-07-23	2027-01-15
DD1370	Pile diagram	2026-07-23	2026-10-31
DD1380	Issue pile drawing	2026-11-29	2026-11-29
DD1390	Other professional drawings	2026-07-23	2026-12-15
DD1400	Issue DED drawing	2027-01-15	2027-01-15
S10	Dross Treatment Workshop	2026-06-28	2026-12-21
DD1410	Pile diagram	2026-06-28	2026-10-06
DD1420	Issue pile drawing	2026-11-04	2026-11-04
DD1430	Other professional drawings	2026-06-28	2026-11-20
DD1440	Issue DED drawing	2026-12-21	2026-12-21
S11	Carbon Deposit Treatment Workshop	2026-07-03	2026-10-17
DD1450	Pile diagram	2026-07-03	2026-09-01
DD1460	Issue pile drawing	2026-09-30	2026-09-30
DD1470	Other professional drawings	2026-07-03	2026-09-16
DD1480	Issue DED drawing	2026-10-17	2026-10-17
S12	Aluminium Ingot Yard	2026-07-06	2026-10-20
DD1490	Professional drawings	2026-07-06	2026-09-19
DD1500	Issue DED drawing	2026-10-20	2026-10-20
S13	SPL Temporary Storage	2026-07-03	2026-10-17
DD1510	Pile diagram	2026-07-03	2026-09-01
DD1520	Issue pile drawing	2026-09-30	2026-09-30
DD1530	Other professional drawings	2026-07-03	2026-09-16
DD1540	Issue DED drawing	2026-10-17	2026-10-17
A00	Anode Plant	2026-04-23	2026-12-06
A01	GPC Storage and Conveying	2026-04-23	2026-09-06
DD1550	Pile diagram	2026-04-23	2026-07-07
DD1560	Issue pile drawing	2026-08-05	2026-08-05
DD1570	Other professional drawings	2026-04-23	2026-08-06
DD1580	Issue DED drawing	2026-09-06	2026-09-06
A02	Calcination Shop	2026-06-28	2026-12-06
DD1590	Pile diagram	2026-06-28	2026-09-11
DD1600	Issue pile drawing	2026-10-10	2026-10-10
DD1610	Other professional drawings	2026-06-28	2026-11-05
DD1620	Issue DED drawing	2026-12-06	2026-12-06
A03	Green Anode Shop	2026-05-21	2026-11-09
DD1630	Pile diagram	2026-05-21	2026-07-25
DD1640	Issue pile drawing	2026-08-23	2026-08-23
DD1650	Other professional drawings	2026-05-21	2026-10-09
DD1660	Issue DED drawing	2026-11-09	2026-11-09
A04	Baking Furnace & Anode Transfer Station	2026-05-21	2026-09-24
DD1670	Pile diagram	2026-05-21	2026-07-25
DD1680	Issue pile drawing	2026-08-23	2026-08-23
DD1690	Other professional drawings	2026-05-21	2026-08-24
DD1700	Issue DED drawing	2026-09-24	2026-09-24
A05	Butts Treatment Shop	2026-05-31	2026-11-13
DD1710	Pile diagram	2026-05-31	2026-09-13
DD1720	Issue pile drawing	2026-10-12	2026-10-12
DD1730	Other professional drawings	2026-05-31	2026-10-13
DD1740	Issue DED drawing	2026-11-13	2026-11-13
A06	Solid Pitch Storage	2026-07-03	2026-10-17
DD1750	Pile diagram	2026-07-03	2026-09-01
DD1760	Issue pile drawing	2026-09-30	2026-09-30
DD1770	Other professional drawings	2026-07-03	2026-09-16
DD1780	Issue DED drawing	2026-10-17	2026-10-17
A07	Pitch Melting Shop	2026-06-28	2026-10-27
DD1790	Pile diagram	2026-06-28	2026-08-27
DD1800	Issue pile drawing	2026-09-25	2026-09-25
DD1810	Other professional drawings	2026-06-28	2026-09-26
DD1820	Issue DED drawing	2026-10-27	2026-10-27
A08	Baking Furnace Fume Treatment Center	2026-05-25	2026-10-03
DD1830	Pile diagram	2026-05-25	2026-07-24
DD1840	Issue pile drawing	2026-08-29	2026-08-29
DD1850	Other professional drawings	2026-05-25	2026-09-02
DD1860	Issue DED drawing	2026-10-03	2026-10-03
A09	Calcination Fume Treatment Center	2026-05-25	2026-10-03
DD1870	Pile diagram	2026-05-25	2026-07-24
DD1880	Issue pile drawing	2026-08-29	2026-08-29
DD1890	Other professional drawings	2026-05-25	2026-09-02
DD1900	Issue DED drawing	2026-10-03	2026-10-03
A10	Anode Rodding Shop	2026-05-31	2026-11-28
DD1910	Pile diagram	2026-05-31	2026-09-13
DD1920	Issue pile drawing	2026-10-12	2026-10-12
DD1930	Other professional drawings	2026-05-31	2026-10-28
DD1940	Issue DED drawing	2026-11-28	2026-11-28

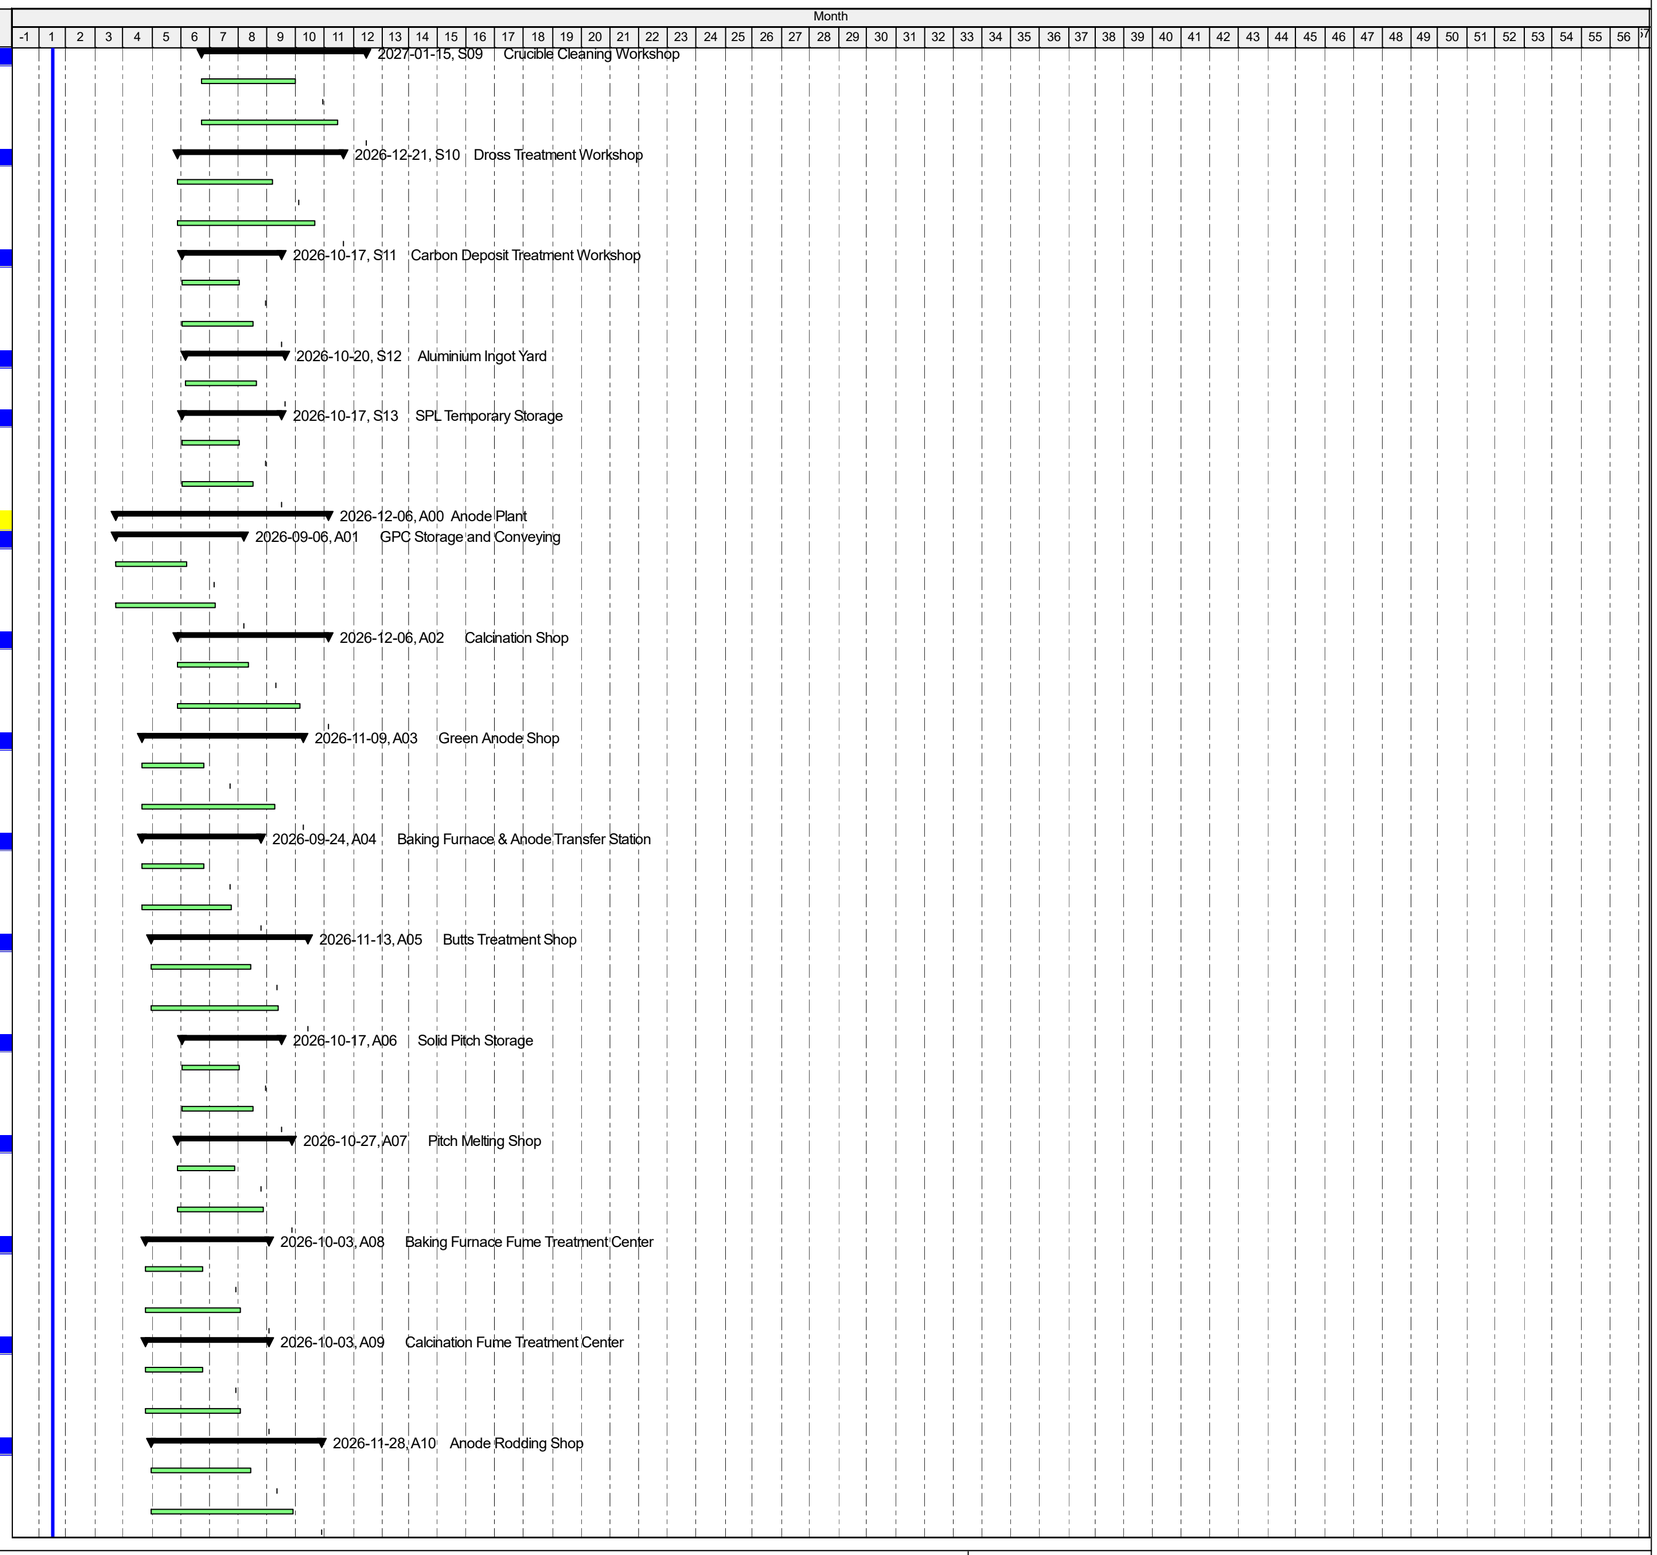

Remaining Level of Effort
Actual Work
Critical Remaining Work
summary
Actual Level of Effort
Remaining Work
Milestone

Project Schedule(Level 3)

Activity ID	Activity Name	Start	Finish
A11	Bath Treatment System	2026-05-31	2026-11-28
DD1950	Pile diagram	2026-05-31	2026-09-13
DD1960	Issue pile drawing	2026-10-12	2026-10-12
DD1970	Other professional drawings	2026-05-31	2026-10-28
DD1980	Issue DED drawing	2026-11-28	2026-11-28
A12	Stem and Stub Repair Workshop	2026-06-23	2026-10-07
DD1990	Pile diagram	2026-06-23	2026-08-22
DD2000	Issue pile drawing	2026-09-20	2026-09-20
DD2010	Other professional drawings	2026-06-23	2026-09-06
DD2020	Issue DED drawing	2026-10-07	2026-10-07
A13	Waste Heat Boiler Room	2026-06-23	2026-11-06
DD2030	Pile diagram	2026-06-23	2026-09-06
DD2040	Issue pile drawing	2026-10-05	2026-10-05
DD2050	Other professional drawings	2026-06-23	2026-10-06
DD2060	Issue DED drawing	2026-11-06	2026-11-06
A14	Heat Transfer Medium Boiler and Pump Room	2026-06-23	2026-11-06
DD2070	Pile diagram	2026-06-23	2026-09-06
DD2080	Issue pile drawing	2026-10-05	2026-10-05
DD2090	Other professional drawings	2026-06-23	2026-10-06
DD2100	Issue DED drawing	2026-11-06	2026-11-06
U00	Utilities	2026-03-10	2027-03-08
U01	330kV Power Distribution Device	2026-06-10	2026-10-14
DD2110	Pile diagram	2026-06-10	2026-08-14
DD2120	Issue pile drawing	2026-09-12	2026-09-12
DD2130	Other professional drawings	2026-06-10	2026-09-13
DD2140	Issue DED drawing	2026-10-14	2026-10-14
U02	330/10.5kV Substation and Center Control Room	2026-06-28	2026-10-17
DD2150	Pile diagram	2026-06-28	2026-08-22
DD2160	Issue pile drawing	2026-09-20	2026-09-20
DD2170	Other professional drawings	2026-06-28	2026-09-16
DD2180	Issue DED drawing	2026-10-17	2026-10-17
U03	Rectifier Station	2026-06-10	2026-10-14
DD2190	Pile diagram	2026-06-10	2026-08-14
DD2200	Issue pile drawing	2026-09-12	2026-09-12
DD2210	Other professional drawings	2026-06-10	2026-09-13
DD2220	Issue DED drawing	2026-10-14	2026-10-14
U05	Emergency Oil Pools and Oil Storage Facilities	2026-08-08	2026-11-23
DD2230	Pile diagram	2026-08-08	2026-09-27
DD2240	Issue pile drawing	2026-10-26	2026-10-26
DD2250	Other professional drawings	2026-08-08	2026-10-23
DD2260	Issue DED drawing	2026-11-23	2026-11-23
U06	11kV Distribution Room in Anode Area	2026-07-08	2026-10-23
DD2270	Pile diagram	2026-07-08	2026-08-27
DD2280	Issue pile drawing	2026-09-25	2026-09-25
DD2290	Other professional drawings	2026-07-08	2026-09-22
DD2300	Issue DED drawing	2026-10-23	2026-10-23
U07	Diesel Generator Room	2026-08-08	2026-11-23
DD2310	Pile diagram	2026-08-08	2026-09-27
DD2320	Issue pile drawing	2026-10-26	2026-10-26
DD2330	Other professional drawings	2026-08-08	2026-10-23
DD2340	Issue DED drawing	2026-11-23	2026-11-23
U09	Compressor Station	2026-08-08	2026-11-23
DD2350	Pile diagram	2026-08-08	2026-09-27
DD2360	Issue pile drawing	2026-10-26	2026-10-26
DD2370	Other professional drawings	2026-08-08	2026-10-23
DD2380	Issue DED drawing	2026-11-23	2026-11-23
U10	Water Supply Pressurized Pump House	2026-07-24	2026-12-07
DD2390	Pile diagram	2026-07-24	2026-10-07
DD2400	Issue pile drawing	2026-11-05	2026-11-05
DD2410	Other professional drawings	2026-07-24	2026-11-06
DD2420	Issue DED drawing	2026-12-07	2026-12-07
U11	Circulating Water System for Cast House	2026-09-23	2027-02-06
DD2430	Pile diagram	2026-09-23	2026-12-07
DD2440	Issue pile drawing	2027-01-05	2027-01-05
DD2450	Other professional drawings	2026-09-23	2027-01-06
DD2460	Issue DED drawing	2027-02-06	2027-02-06
U12	Circulating Water System for Compressor Station	2026-09-23	2027-02-06
DD2470	Pile diagram	2026-09-23	2026-12-07
DD2480	Issue pile drawing	2027-01-05	2027-01-05
DD2490	Other professional drawings	2026-09-23	2027-01-06
DD2500	Issue DED drawing	2027-02-06	2027-02-06
U13	Circulating Water System for Gas Treatment Center	2026-09-07	2027-01-21
DD2510	Pile diagram	2026-09-07	2026-11-21
DD2520	Issue pile drawing	2026-12-20	2026-12-20

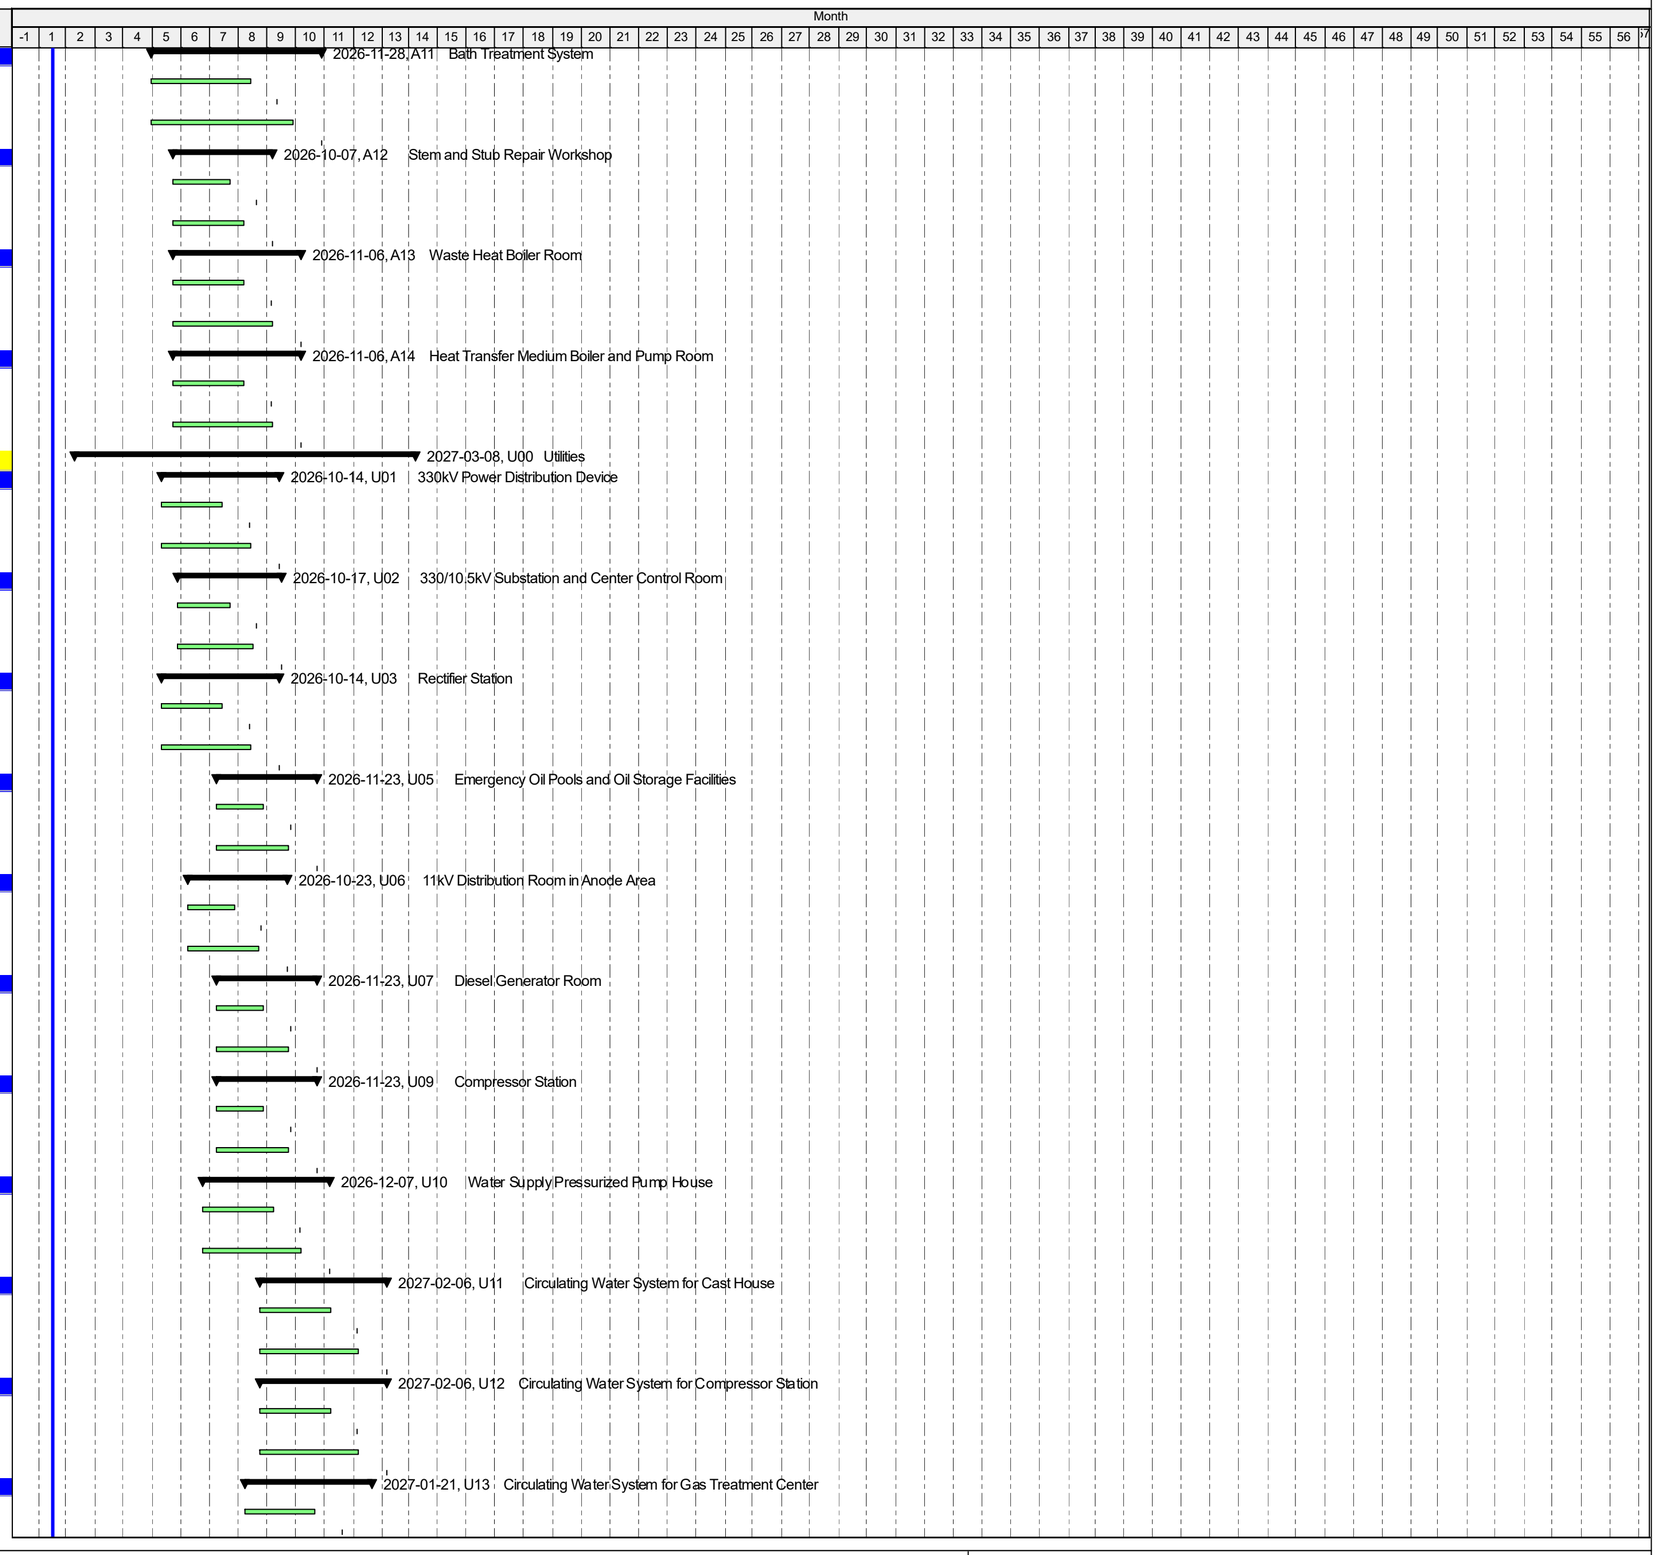

Remaining Level of Effort | Actual Work | Critical Remaining Work | summary
Actual Level of Effort | Remaining Work | Milestone

Project Schedule(Level 3)

Activity ID	Activity Name	Start	Finish
DD2530	Other professional drawings	2026-09-07	2026-12-21
DD2540	Issue DED drawing	2027-01-21	2027-01-21
U14	**Circulating Water System for Calcination Shop**	2026-09-23	2027-02-06
DD2550	Pile diagram	2026-09-23	2026-12-07
DD2560	Issue pile drawing	2027-01-05	2027-01-05
DD2570	Other professional drawings	2026-09-23	2027-01-06
DD2580	Issue DED drawing	2027-02-06	2027-02-06
U15	**Circulating Water System for Green Anode Shop**	2026-09-07	2027-01-21
DD2590	Pile diagram	2026-09-07	2026-11-21
DD2600	Issue pile drawing	2026-12-20	2026-12-20
DD2610	Other professional drawings	2026-09-07	2026-12-21
DD2620	Issue DED drawing	2027-01-21	2027-01-21
U16	**Circulating Water System for Anode Rodding Shop**	2026-09-07	2027-01-21
DD2630	Pile diagram	2026-09-07	2026-11-21
DD2640	Issue pile drawing	2026-12-20	2026-12-20
DD2650	Other professional drawings	2026-09-07	2026-12-21
DD2660	Issue DED drawing	2027-01-21	2027-01-21
U18	**Production Waste Water Treatment Station**	2026-09-23	2027-02-06
DD2670	Pile diagram	2026-09-23	2026-12-07
DD2680	Issue pile drawing	2027-01-05	2027-01-05
DD2690	Other professional drawings	2026-09-23	2027-01-06
DD2700	Issue DED drawing	2027-02-06	2027-02-06
U19	**Domestic Waste Water Treatment Station**	2026-09-23	2027-02-06
DD2710	Pile diagram	2026-09-23	2026-12-07
DD2720	Issue pile drawing	2027-01-05	2027-01-05
DD2730	Other professional drawings	2026-09-23	2027-01-06
DD2740	Issue DED drawing	2027-02-06	2027-02-06
U20	**Rainwater Collecting Pond**	2026-09-23	2027-02-06
DD2750	Pile diagram	2026-09-23	2026-12-07
DD2760	Issue pile drawing	2027-01-05	2027-01-05
DD2770	Other professional drawings	2026-09-23	2027-01-06
DD2780	Issue DED drawing	2027-02-06	2027-02-06
U22	**Comprehensive Maintenance Workshop**	2026-06-23	2026-09-17
DD2790	Pile diagram	2026-06-23	2026-08-02
DD2800	Issue pile drawing	2026-08-31	2026-08-31
DD2810	Other professional drawings	2026-06-23	2026-08-17
DD2820	Issue DED drawing	2026-09-17	2026-09-17
U23	**Reduction Pot Repair Room**	2026-05-26	2026-09-04
DD2830	Pile diagram	2026-05-26	2026-07-25
DD2840	Issue pile drawing	2026-08-23	2026-08-23
DD2850	Other professional drawings	2026-05-26	2026-08-04
DD2860	Issue DED drawing	2026-09-04	2026-09-04
U24	**Carbon Repair Room**	2026-06-23	2026-11-06
DD2870	Pile diagram	2026-06-23	2026-09-06
DD2880	Issue pile drawing	2026-10-05	2026-10-05
DD2890	Other professional drawings	2026-06-23*	2026-10-06
DD2900	Issue DED drawing	2026-11-06*	2026-11-06
U25	**General Warehouse**	2026-06-23	2026-09-17
DD2910	Pile diagram	2026-06-23	2026-08-02
DD2920	Issue pile drawing	2026-08-31	2026-08-31
DD2930	Other professional drawings	2026-06-23	2026-08-17
DD2940	Issue DED drawing	2026-09-17	2026-09-17
U26	**Process Vehicle Garage and Repair Shop**	2026-06-23	2026-11-06
DD2950	Pile diagram	2026-06-23	2026-09-06
DD2960	Issue pile drawing	2026-10-05	2026-10-05
DD2970	Other professional drawings	2026-06-23	2026-10-06
DD2980	Issue DED drawing	2026-11-06	2026-11-06
U27	**Truck Scale**	2026-09-07	2027-01-21
DD2990	Pile diagram	2026-09-07	2026-11-21
DD3000	Issue pile drawing	2026-12-20	2026-12-20
DD3010	Other professional drawings	2026-09-07	2026-12-21
DD3020	Issue DED drawing	2027-01-21	2027-01-21
U29	**General Layout of the Plant**	2026-10-23	2027-03-08
DD3030	General layout of the plant	2026-10-23	2027-02-05
DD3040	Issue final DED drawing	2027-03-08	2027-03-08
U30	**Plant Roadway & Vertical Planning**	2026-10-23	2027-03-08
DD3050	Professional drawings	2026-10-23	2027-02-05
DD3060	Issue final DED drawing	2027-03-08	2027-03-08
U31	**Piping and Cable Tray Network**	2026-10-23	2027-03-08
DD3070	Pile diagram	2026-10-23	2027-01-06
DD3080	Issue pile drawing	2027-02-04	2027-02-04
DD3090	Professional drawings	2026-10-23	2027-02-05
DD3100	Issue final DED drawing	2027-03-08	2027-03-08
U32	**Potroom Trestle and Ramp**	2026-03-10	2026-07-24

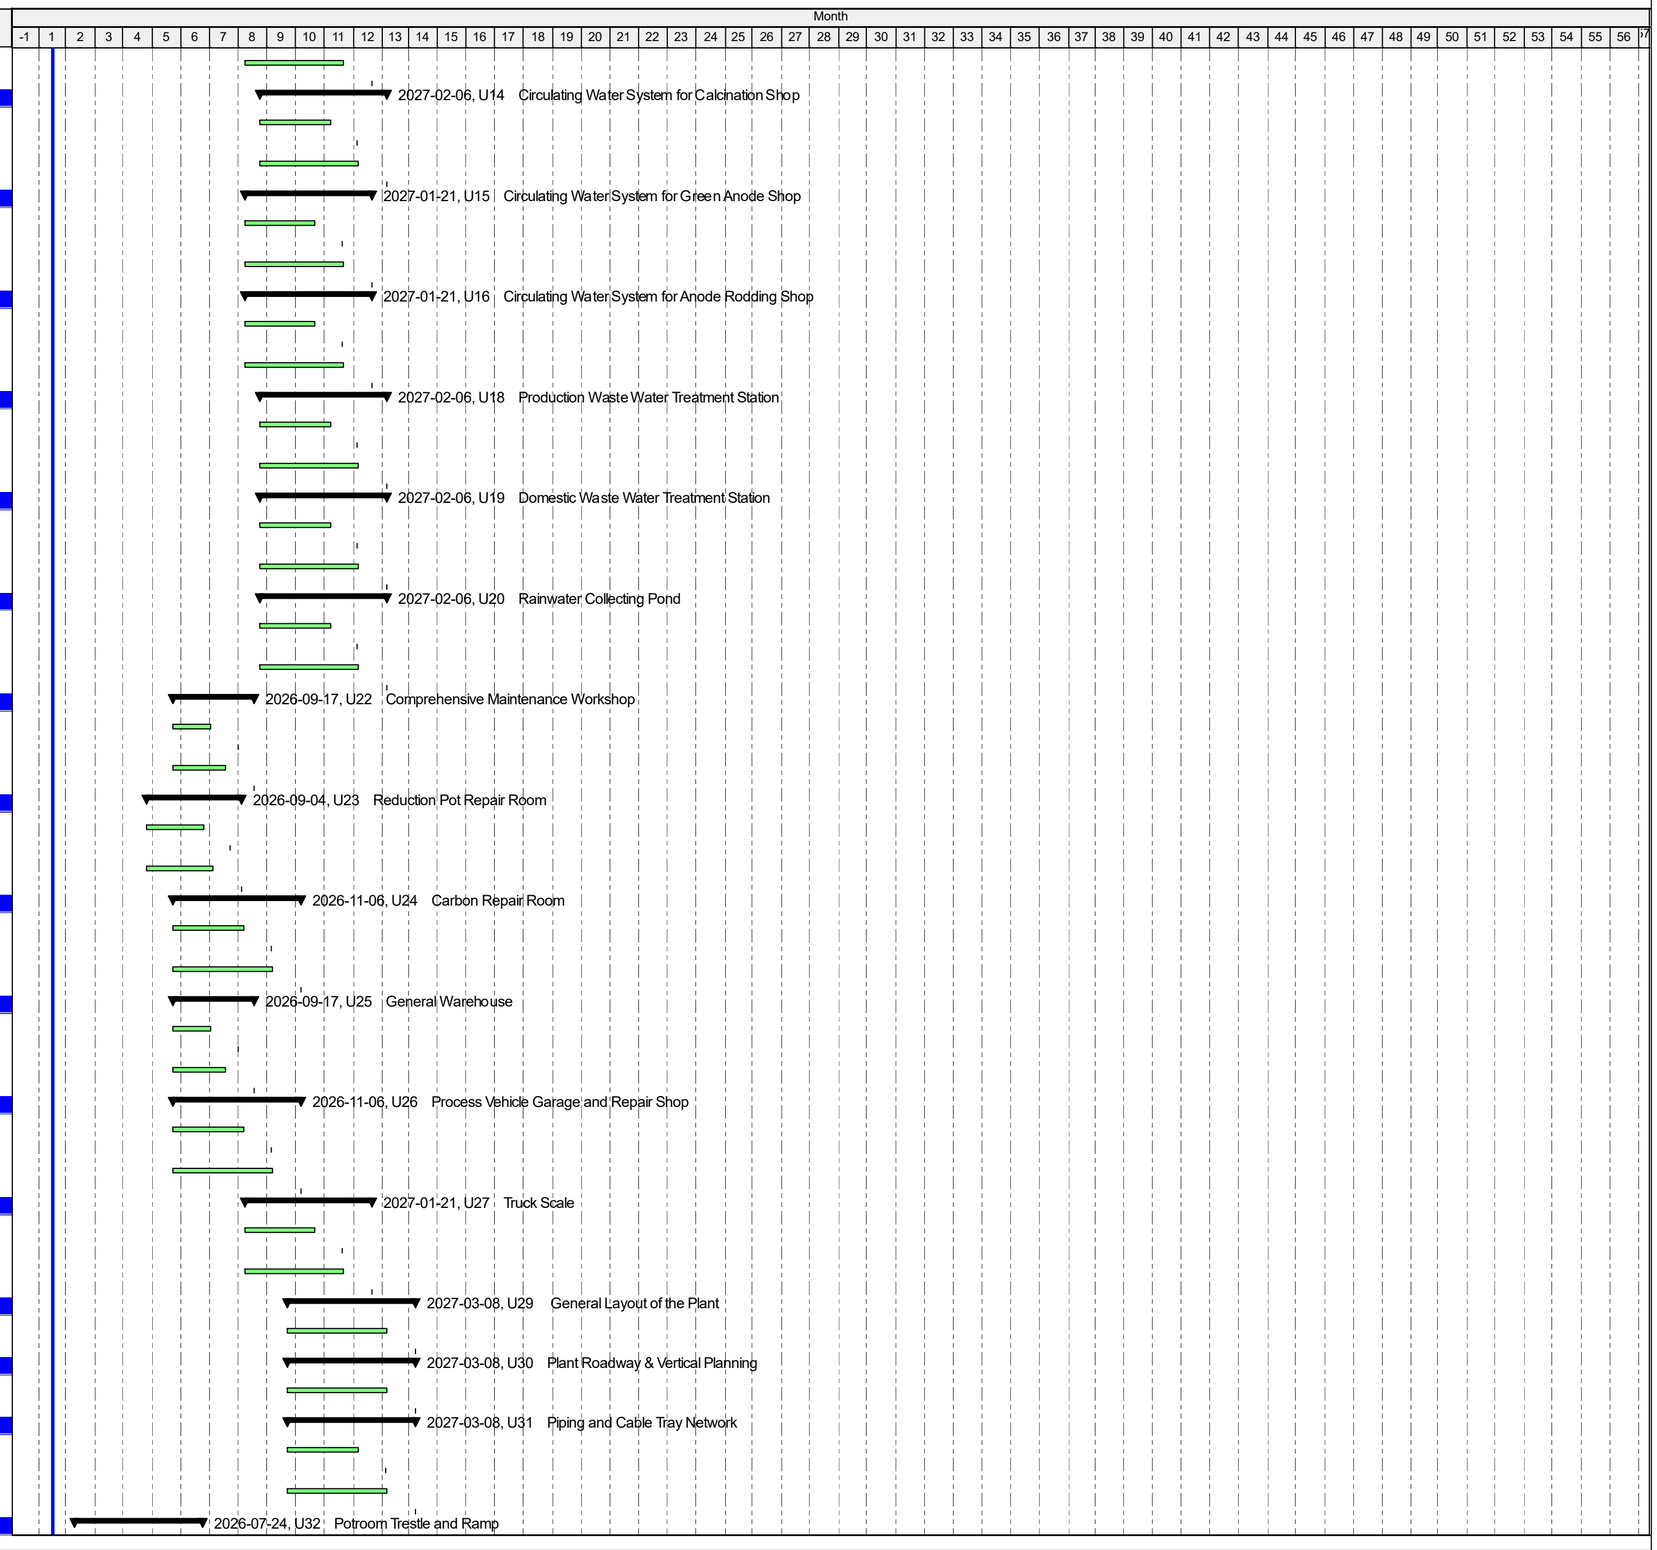

Remaining Level of Effort | Actual Work | Critical Remaining Work | summary
Actual Level of Effort | Remaining Work | Milestone

Project Schedule(Level 3)

Activity ID	Activity Name	Start	Finish
DD3110	Pile diagram	2026-03-10	2026-05-24
DD3120	Issue pile drawing	2026-06-22	2026-06-22
DD3130	Other professional drawings	2026-03-10	2026-06-23
DD3140	Issue DED drawing	2026-07-24	2026-07-24
U33	Natural Gas Press Regulating Station	2026-06-23	2026-11-06
DD3150	Pile diagram	2026-06-23	2026-09-06
DD3160	Issue pile drawing	2026-10-05	2026-10-05
DD3170	Other professional drawings	2026-06-23	2026-10-06
DD3180	Issue DED drawing	2026-11-06	2026-11-06
M00	Management and Welfare Facilities Administration and Welfare Facilities	2026-03-23	2026-11-06
M01	Comprehensive Office Building	2026-05-30	2026-10-13
DD3190	Pile diagram	2026-05-30	2026-08-13
DD3200	Issue pile drawing	2026-09-11	2026-09-11
DD3210	Other professional drawings	2026-05-30	2026-09-12
DD3220	Issue DED drawing	2026-10-13	2026-10-13
M02	Reduction Area Comprehensive Building	2026-05-30	2026-10-13
DD3230	Pile diagram	2026-05-30	2026-08-13
DD3240	Issue pile drawing	2026-09-11	2026-09-11
DD3250	Other professional drawings	2026-05-30	2026-09-12
DD3260	Issue DED drawing	2026-10-13	2026-10-13
M03	Dining Hall	2026-06-23	2026-11-06
DD3270	Pile diagram	2026-06-23	2026-09-06
DD3280	Issue pile drawing	2026-10-05	2026-10-05
DD3290	Other professional drawings	2026-06-23	2026-10-06
DD3300	Issue DED drawing	2026-11-06	2026-11-06
M04	Shower Room	2026-06-23	2026-11-06
DD3310	Pile diagram	2026-06-23	2026-09-06
DD3320	Issue pile drawing	2026-10-05	2026-10-05
DD3330	Other professional drawings	2026-06-23	2026-10-06
DD3340	Issue DED drawing	2026-11-06	2026-11-06
M06	Plant Fence, Gate and Guard Room	2026-03-23	2026-08-06
DD3350	Pile diagram	2026-03-23	2026-06-06
DD3360	Issue pile drawing	2026-07-05	2026-07-05
DD3370	Other professional drawings	2026-03-23	2026-07-06
DD3380	Issue DED drawing	2026-08-06	2026-08-06
Employer Review and Approval		2026-04-25	2027-02-26
DD3390	E00 External Engineering Works Outside Plant Fence	2026-09-07	2026-11-26
DD3400	S00 Aluminum Reduction Plant	2026-04-25	2026-12-11
DD3410	A00 Anode Plant	2026-07-08	2026-11-26
DD3420	U00 Utilities	2026-05-25	2027-02-26
DD3430	M00 Management and Welfare Facilities Administration and Welfare Facil	2026-06-07	2026-10-27
Procurement		2026-02-15	2029-07-14
Installation Temporary Facilities Shipping		2026-05-26	2027-05-23
PR1010	1st Batch Sipping	2026-05-26	2026-09-27
PR1020	2nd Batch Sipping	2026-08-13	2026-12-16
PR1030	3rd Batch Sipping	2026-10-17	2027-02-19
PR1040	Last Batch Sipping	2027-01-18	2027-05-23
Civil Work Material Shiping		2026-10-26	2029-01-16
PR1050	1st Batch Steel Structure Shipping	2026-10-26	2027-02-28
PR1060	Last Batch Civil Material Shipping	2028-09-13	2029-01-16
Process Equipment		2026-02-15	2029-07-14
E00 External Engineering Works Outside Plant Fence		2026-03-30	2028-04-10
E01 Raw Material Conveying system		2026-03-30	2028-04-10
Belt Conveyor		2026-03-30	2028-04-10
PR1070	Bidding	2026-03-30	2026-05-29
PR1080	Manufacturing	2027-04-11	2027-10-08
PR1090	Shipping	2027-12-07	2028-04-10
S00 Aluminum Reduction Plant		2026-02-15	2029-07-14
S01 Potroom		2026-02-15	2029-07-12
Busbar		2026-06-01	2029-03-12
PR1100	Bidding	2026-06-01*	2026-08-30
PR1110	1st Batch Manufacturing	2026-08-31	2027-04-29
PR1120	1st Batch Shipping	2027-05-03	2027-09-05
PR1130	Last Batch Shipping	2028-11-07	2029-03-12
Potshell		2026-07-01	2029-04-27
PR1140	Bidding	2026-07-01	2026-09-30
PR1150	1st Batch Manufacturing	2026-10-01	2027-06-29
PR1160	1st Batch Shipping	2027-07-23*	2027-11-25
PR1170	Last Batch Shipping	2028-12-23	2029-04-27*
SuperStructure		2026-07-01	2029-07-12
PR1180	Bidding	2026-07-01	2026-09-30
PR1190	1st Batch Manufacturing	2026-10-01	2027-06-29
PR1200	1st Batch Shipping	2027-09-23	2028-01-26
PR1210	Last Batch Shipping	2029-03-09	2029-07-12

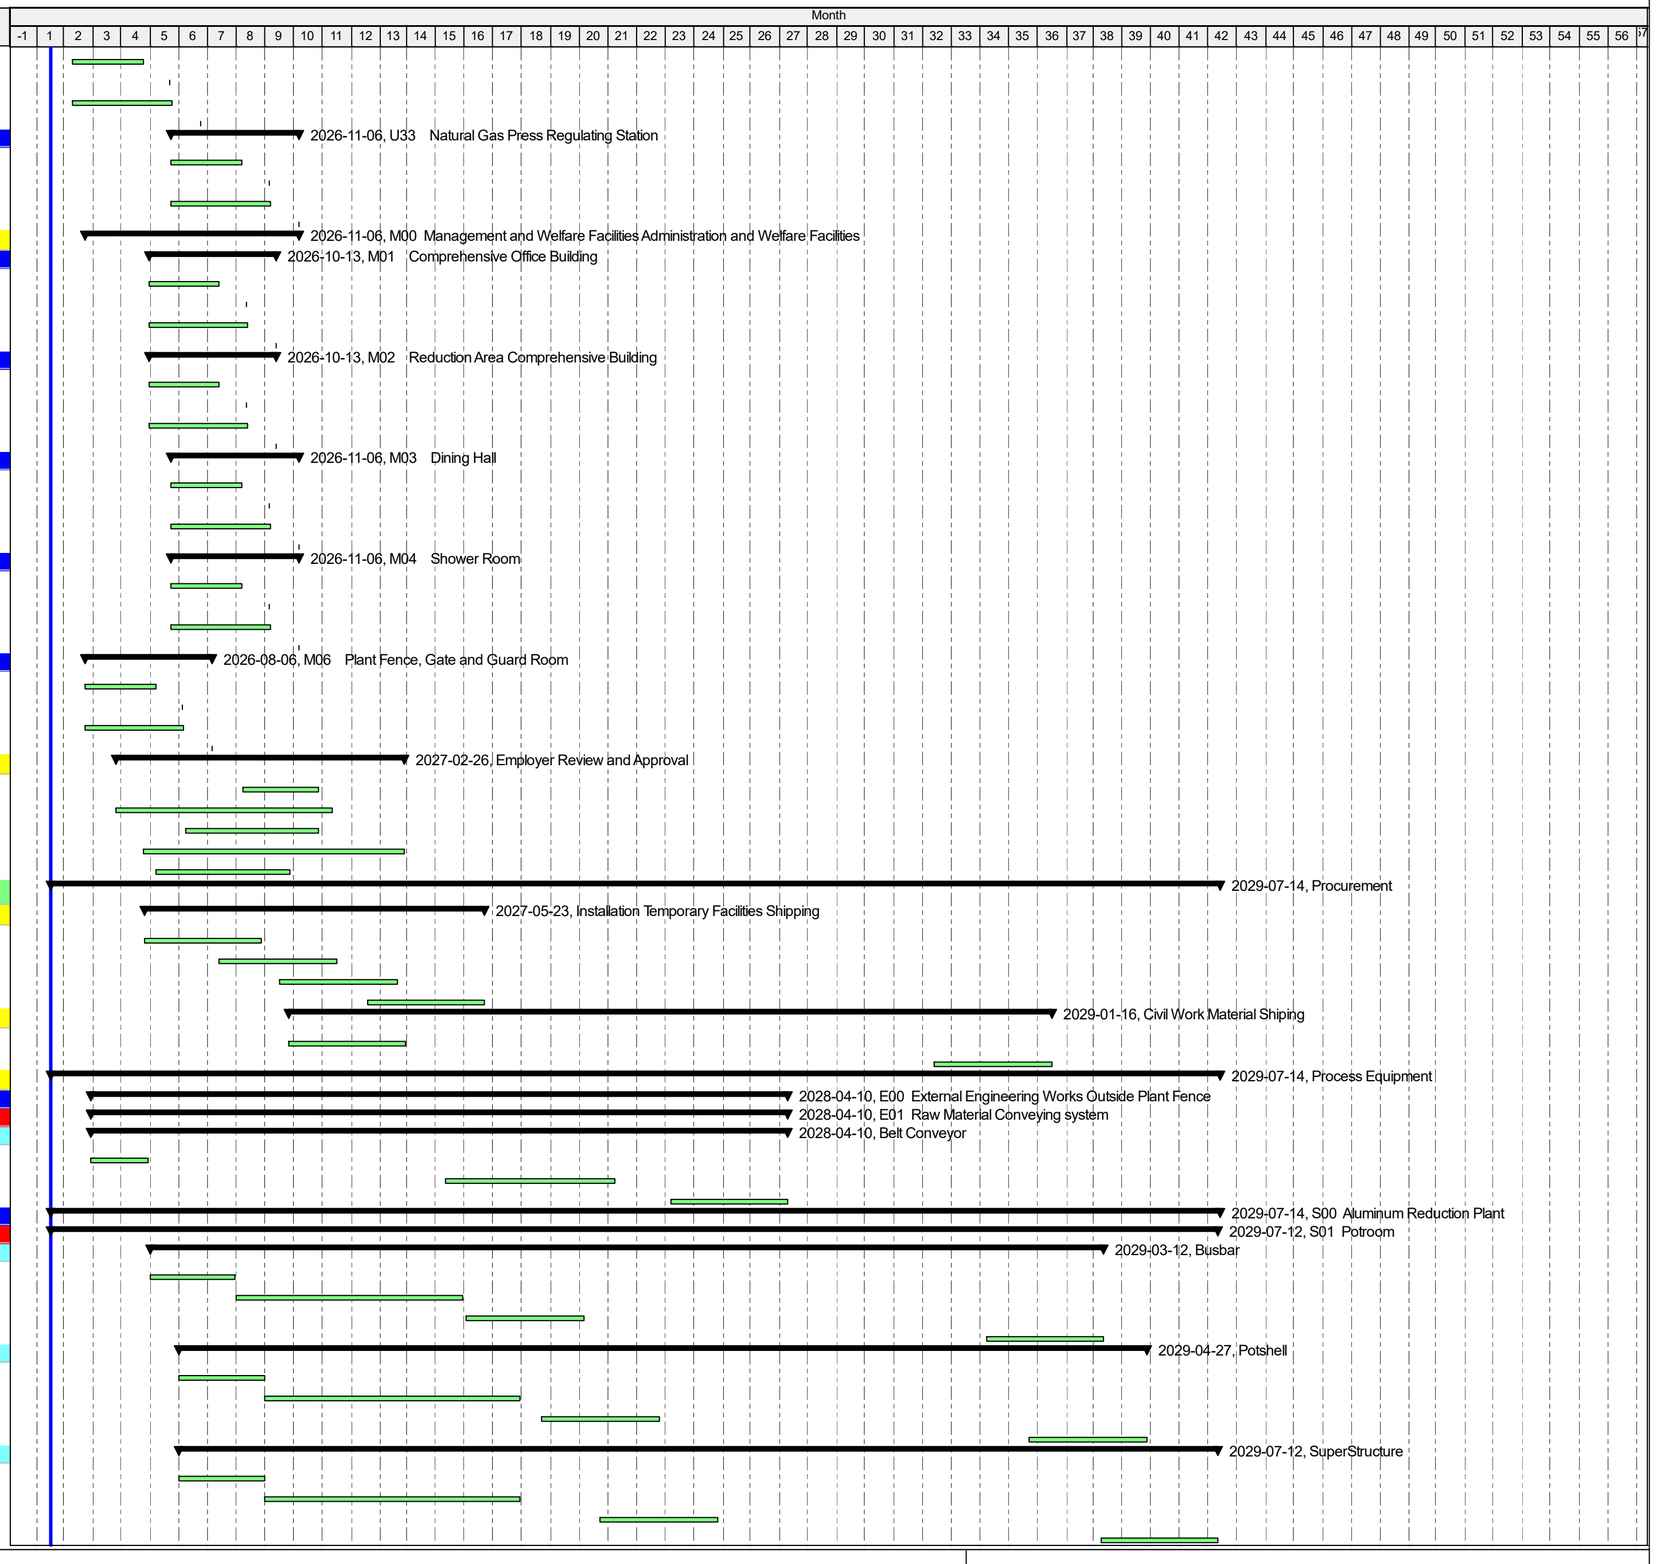

Remaining Level of Effort | Actual Work | Critical Remaining Work | summary
Actual Level of Effort | Remaining Work | Milestone

Project Schedule(Level 3)

Activity ID	Activity Name	Start	Finish
Cathode Block		2026-05-15	2029-06-08
PR1220	Bidding Document Preparation	2026-05-15	2026-06-01
PR1230	Bidding and Tendering	2026-06-02	2026-07-05
PR1240	Contractor Evaluation	2026-07-06	2026-07-25
PR1250	Employer Evaluation and Award	2026-07-26	2026-08-24
PR1260	Signing Subcontract	2026-08-25	2026-09-14
PR1270	Advance Payment	2026-09-15	2026-10-29
PR1280	1st Batch Manufacturing	2026-10-30	2027-05-27
PR1290	1st Batch Shipping	2027-08-07*	2027-11-20
PR1300	Last Batch Shipping	2029-02-23	2029-06-08*
Collector Bar		2026-07-01	2029-06-08
PR1310	Bidding	2026-07-01	2026-09-30
PR1320	1st Batch Manufacturing	2026-10-31	2027-04-28
PR1330	1st Batch Shipping	2027-07-18	2027-11-20
PR1340	Last Batch Shipping	2029-02-03	2029-06-08
Cathode Casting Material, etc.		2026-05-31	2029-06-08
PR1350	Bidding	2026-05-31	2026-08-30
PR1360	1st Batch Manufacturing	2026-09-30	2027-03-28
PR1370	1st Batch Shipping	2027-07-18	2027-11-20
PR1380	Last Batch Shipping	2029-02-03	2029-06-08
Other Lining Material		2026-07-01	2029-06-12
PR1390	Bidding of Material	2026-07-01	2026-09-30
PR1400	1st Batch Manufacturing	2026-10-31	2027-04-28
PR1410	1st Batch Shipping	2027-08-23	2027-12-26
PR1420	Last Batch Shipping	2029-02-07	2029-06-12
PTM		2026-02-15	2029-05-28
PR1430	Bidding	2026-02-15	2026-05-23
PR1440	1st Batch Manufacturing	2026-05-24	2027-06-29
PR1450	1st Batch Shipping	2027-08-12	2027-12-15
PR1460	Last Batch Shipping	2029-01-23	2029-05-28
Pot Control System		2026-07-01	2029-06-17
PR1470	Bidding, Manufacturing and Shipping	2026-07-01	2026-09-30
PR1480	1st Batch Manufacturing	2027-08-14	2027-12-12
PR1490	1st Batch Shipping	2027-12-12	2028-03-26
PR1500	Last Batch Shipping	2029-03-04	2029-06-17
Mobile Equipment and Vehicle		2027-04-09	2029-04-26
PR1510	Bidding	2027-04-09	2027-08-07
PR1520	1st Batch Manufacturing	2027-08-08	2028-02-04
PR1530	1st Batch Shipping	2028-02-05	2028-06-09
PR1540	Last Batch Shipping	2028-12-22	2029-04-26
Material		2026-08-10	2029-07-12
PR1550	Bidding	2026-08-10	2026-11-10
PR1560	1st Batch Manufacturing	2026-12-10	2027-05-09
PR1570	1st Batch Shipping	2027-06-08	2027-10-11*
PR1580	Last Batch Shipping	2029-03-09	2029-07-12
S02 Potline Gas Treatment Center		2026-02-15	2028-09-15
GTC (Include Desulfurization)		2026-02-15	2028-09-15
PR1590	Bidding	2026-02-15	2026-04-10
PR1600	1st Batch Manufacturing	2026-04-11	2026-10-27
PR1610	1st Batch Shipping	2026-12-01	2027-04-05
PR1620	Last Batch Shipping	2028-05-13	2028-09-15
S03 Alumina Storage		2026-03-02	2028-03-27
Steel Silo		2026-03-02	2027-12-11
PR1630	Bidding	2026-03-02	2026-05-01
PR1640	Manufacturing	2026-11-11	2027-07-09
PR1650	Shipping	2027-08-08	2027-12-11
Equipment		2026-03-02	2028-03-27
PR1660	Bidding	2026-03-02	2026-05-01*
PR1670	Manufacturing	2027-04-27	2027-10-24
PR1680	Shipping	2027-11-23	2028-03-27
S04 Alumina Conveying and Daly Silo		2026-03-02	2028-03-26
Steel Silo		2026-03-02	2028-02-19
PR1690	Bidding	2026-03-02	2026-05-01*
PR1700	1st Batch Manufacturing	2026-08-14	2027-01-11
PR1710	1st Batch Shipping	2027-02-10	2027-06-15
PR1720	Last Batch Shipping	2027-10-17	2028-02-19
Equipment		2026-03-02	2028-03-26
PR1730	Bidding	2026-03-02	2026-05-01*
PR1740	Manufacturing	2027-04-26	2027-10-23
PR1750	Shipping	2027-11-22	2028-03-26
S05 Fluoride Storage		2026-06-01	2028-08-05
Hook Bridge Crane and Other Equipment		2026-06-01	2028-08-05
PR1760	Bidding	2026-06-01	2026-08-01
PR1770	Manufacturing	2027-07-22	2028-02-02

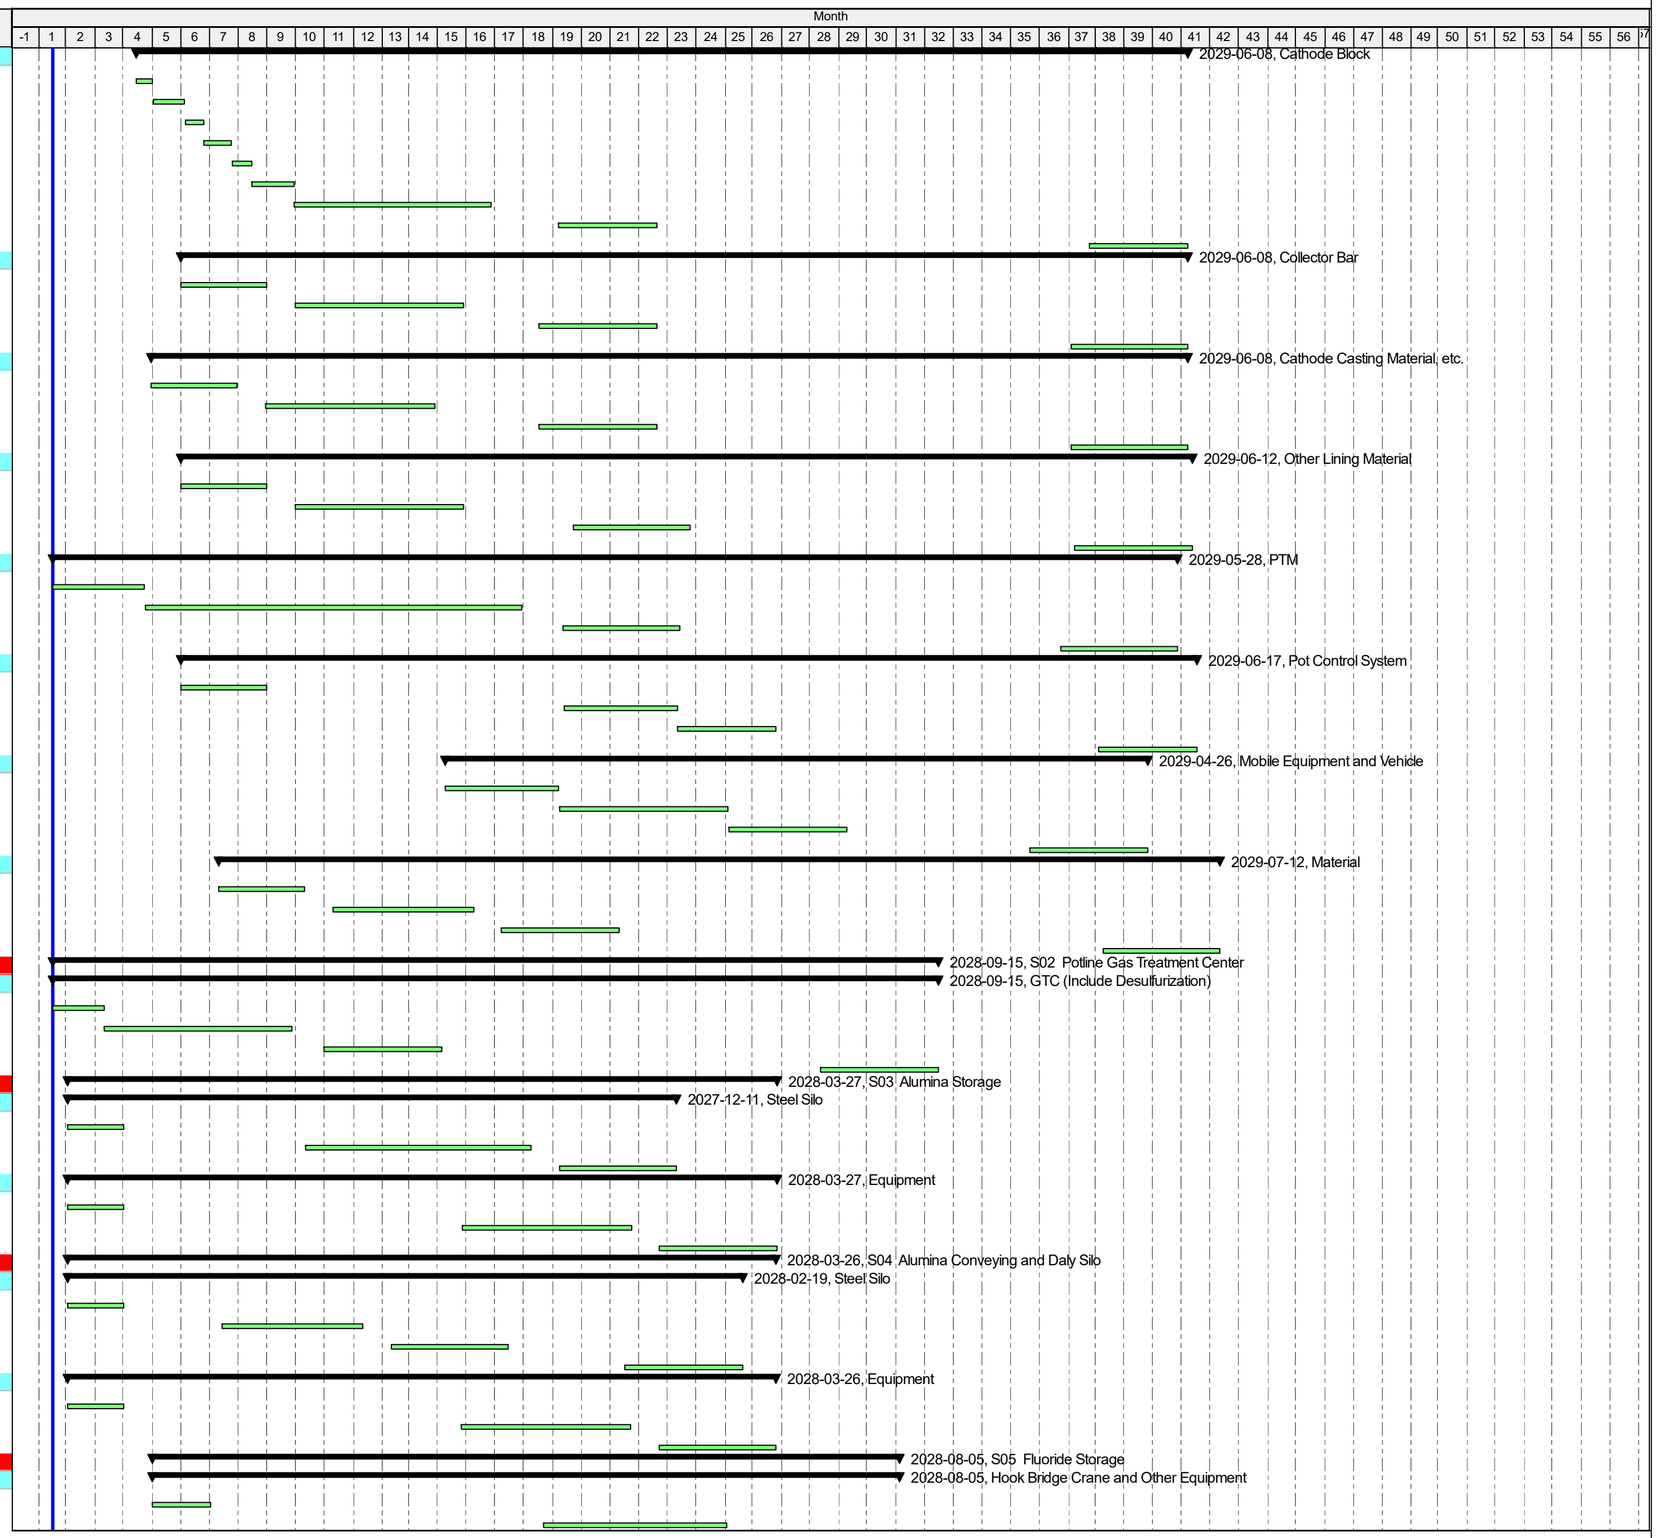

Remaining Level of Effort | Actual Work | Critical Remaining Work | summary
Actual Level of Effort | Remaining Work | Milestone

Project Schedule(Level 3)

Activity ID	Activity Name	Start	Finish
PR1780	Shipping	2028-04-02	2028-08-05
S06	Super Dense Phase Conveying System	2026-03-02	2029-07-14
Steel Silo		2026-03-02	2028-03-26
PR1790	Bidding	2026-03-02	2026-05-01*
PR1800	1st Batch Manufacturing	2026-07-05	2026-12-02
PR1810	1st Batch Shipping	2027-01-01	2027-05-06
PR1820	Last Batch Shipping	2027-11-22	2028-03-26
Equipment		2026-05-15	2029-07-14
PR1830	Bidding	2026-05-15	2026-07-15
PR1840	1st Batch Manufacturing	2026-12-25	2027-04-29
PR1850	1st Batch Shipping	2027-05-29	2027-09-30*
PR1860	Last Batch Shipping	2029-03-12	2029-07-14*
S07	Anode Covering Material Storage & Conveying System	2026-05-15	2028-04-15
Equipment and Material		2026-05-15	2028-04-15
PR1870	Bidding	2026-05-15	2026-07-15
PR1880	1st Batch Manufacturing	2026-09-28	2027-01-27
PR1890	1st Batch Shipping	2027-01-27	2027-06-01
PR1900	Last Batch Shipping	2027-12-12	2028-04-15
S08	Cast House	2026-03-15	2028-05-20
Gas Mixing Furnace		2026-03-15	2028-05-20
PR1910	Bidding	2026-03-15	2026-05-14
PR1920	Manufacturing	2027-03-22	2027-12-17
PR1930	Shipping	2028-01-16	2028-05-20
25kg Ingot Casting Machine		2026-03-15	2028-05-20
PR1940	Bidding	2026-03-15	2026-05-14*
PR1950	Manufacturing	2027-05-21	2027-12-17
PR1960	Shipping	2028-01-16*	2028-05-20
Hook Bridge Crane		2026-06-01	2028-03-20
PR1970	Bidding	2026-06-01	2026-08-01
PR1980	Manufacturing	2027-03-21	2027-10-17
PR1990	Shipping	2027-11-16	2028-03-20
S09	Crucible Cleaning Workshop	2026-04-12	2028-04-15
Hook Bridge Crane		2026-06-01	2028-04-15
PR2000	Bidding	2026-06-01	2026-08-01*
PR2010	Manufacturing	2027-06-15	2027-11-12
PR2020	Shipping	2027-12-12	2028-04-15
Crucible Cleaning Equipment		2026-04-12	2028-04-15
PR2030	Bidding	2026-04-12	2026-06-12
PR2040	Manufacturing	2027-02-15	2027-11-12
PR2050	Shipping	2027-12-12	2028-04-15
S11	Carbon Deposit Treatment Workshop	2026-04-12	2028-07-11
Single Beam Crane		2026-06-01	2028-07-11
PR2120	Bidding	2026-06-01	2026-08-01*
PR2130	Manufacturing	2027-09-10	2028-02-07
PR2140	Shipping	2028-03-08	2028-07-11
Carbon Deposit Treatment Equipment		2026-04-12	2028-07-11
PR2150	Bidding	2026-04-12	2026-06-12
PR2160	Manufacturing	2027-07-22	2028-02-07
PR2170	Shipping	2028-03-08*	2028-07-11
S10	Dross Treatment Workshop	2026-03-15	2028-08-16
Hook Bridge Crane		2026-06-01	2028-08-16
PR2060	Bidding	2026-06-01	2026-08-01*
PR2070	Manufacturing	2027-10-16	2028-03-14
PR2080	Shipping	2028-04-13	2028-08-16
Dross Treatment Equipment		2026-03-15	2028-08-16
PR2090	Bidding	2026-03-15	2026-06-12*
PR2100	Manufacturing	2027-07-18	2028-03-14
PR2110	Shipping	2028-04-13	2028-08-16
S13	SPL Temporary Storage	2026-06-01	2028-09-10
Hook Bridge Crane		2026-06-01	2028-09-10
PR2180	Bidding	2026-06-01	2026-08-01*
PR2190	Manufacturing	2027-11-10	2028-04-08
PR2200	Shipping	2028-05-08	2028-09-10
A00	Anode Plant	2026-02-15	2029-01-05
A01	GPC Storage and Conveying	2026-02-15	2028-02-04
Hook Bridge Crane		2026-05-30	2028-02-04
PR2210	Bidding	2026-05-30	2026-07-29*
PR2220	Manufacturing	2027-02-19	2027-09-02
PR2230	Shipping	2027-10-02	2028-02-04
Other Equipment		2026-02-15	2028-02-04
PR2240	Bidding	2026-02-15	2026-04-16
PR2250	Manufacturing	2027-03-06	2027-09-02
PR2260	Shipping	2027-10-02	2028-02-04
A02	Calcination Shop	2026-03-30	2028-02-20
Equipment (Steel Structure, Conveyor, Feeder, Bucket Elevator, Crusher, etc.)		2026-03-30	2028-01-20

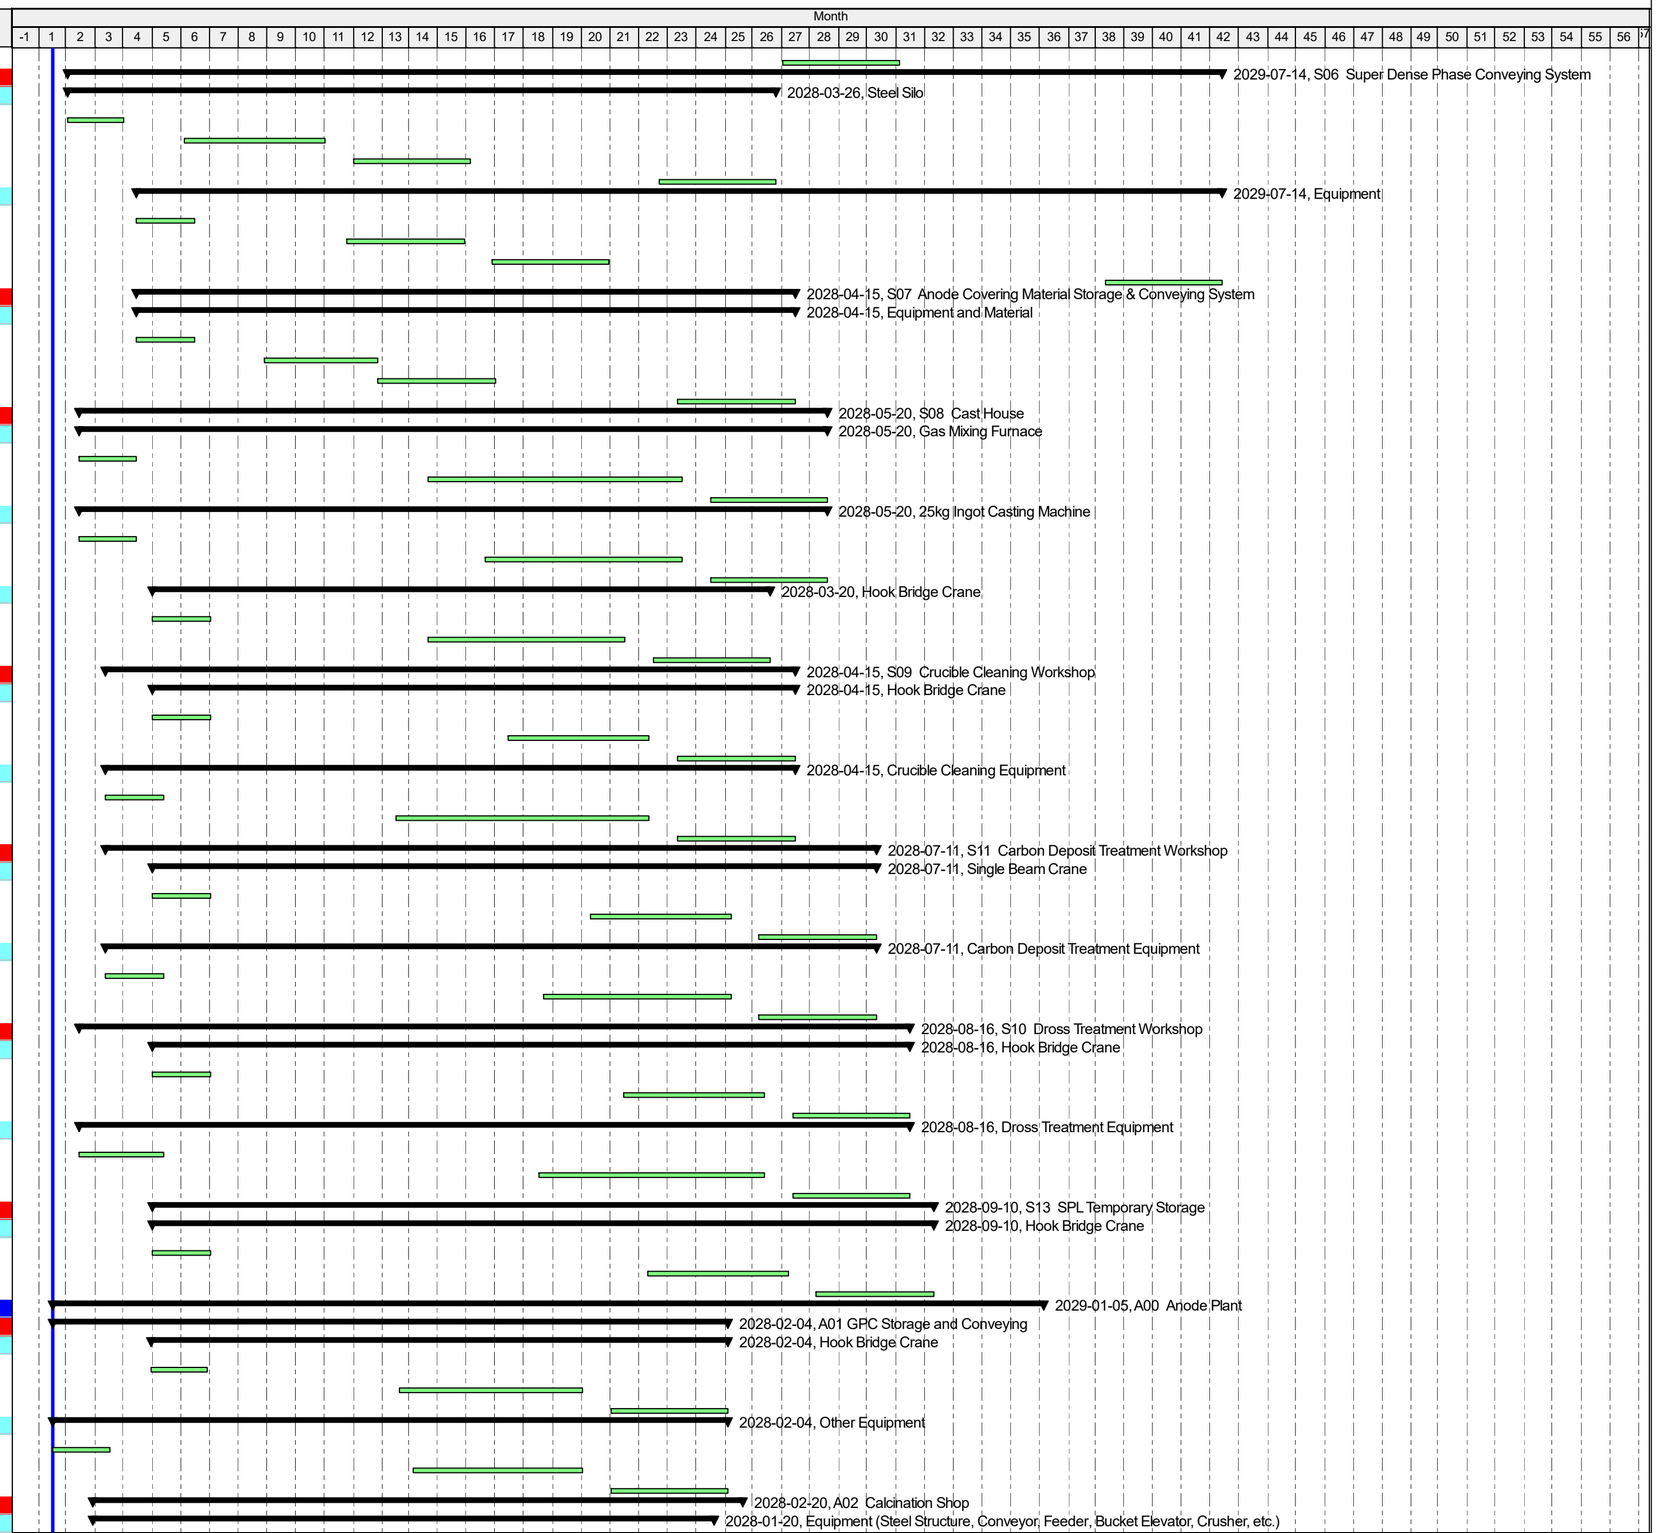

Remaining Level of Effort | Actual Work | Critical Remaining Work | summary
Actual Level of Effort | Remaining Work | Milestone

Project Schedule(Level 3)

Activity ID	Activity Name	Start	Finish
PR2270	Bidding	2026-03-30	2026-05-29
PR2280	1st Batch Manufacturing	2026-09-19	2027-02-16
PR2290	1st Batch Shipping	2027-03-18	2027-07-21
PR2300	Last Batch Shipping	2027-09-17	2028-01-20
Lining Material		2026-03-30	2028-02-20
PR2310	Bidding	2026-03-30	2026-05-29*
PR2320	1st Batch Manufacturing	2026-12-10	2027-05-09
PR2330	1st Batch Shipping	2027-06-08	2027-09-21
PR2340	Last Batch Shipping	2027-11-07	2028-02-20
A03 Green Anode Shop		2026-02-25	2027-10-18
Silo and Bin		2026-02-25	2027-10-18
PR2350	Bidding	2026-02-25	2026-04-26
PR2360	1st Batch Manufacturing	2026-08-20	2027-02-16
PR2370	1st Batch Shipping	2027-03-18	2027-07-21
PR2380	2nd Batch Shipping	2027-06-16	2027-10-18
Preheater, Kneader, and Proportioning System		2026-02-25	2027-09-03
PR2390	Bidding	2026-02-25	2026-04-26*
PR2400	Manufacturing	2026-06-05	2027-04-01*
PR2410	Shipping	2027-05-01	2027-09-03
Vibro Former		2026-02-25	2027-07-21
PR2420	Bidding	2026-02-25	2026-04-26*
PR2430	Manufacturing	2026-06-21*	2027-02-16
PR2440	Shipping	2027-03-18	2027-07-21
Verticle Mill		2026-02-25	2027-07-21
PR2450	Bidding	2026-02-25	2026-04-26*
PR2460	Manufacturing	2026-06-21	2027-02-16*
PR2470	Shipping	2027-03-18	2027-07-21*
A04 Baking Furnace & Anode Transfer Station		2026-02-25	2028-09-17
Stacking Crane		2026-02-25	2028-05-16
PR2480	Bidding	2026-02-25	2026-04-26
PR2490	1st Batch Manufacturing	2026-06-08	2027-05-04
PR2500	1st Batch Shipping	2027-07-03	2027-11-05
PR2510	Last Batch Shipping	2028-01-12	2028-05-16
Furnace Tending Machine		2026-02-25	2028-09-15
PR2520	Bidding	2026-02-25	2026-04-26*
PR2530	1st Batch Manufacturing	2026-10-08	2027-09-03
PR2540	1st Batch Shipping	2027-11-02	2028-03-06
PR2550	Last Batch Shipping	2028-05-13	2028-09-15
Grouping and Cleaning Machine		2026-02-25	2028-09-15
PR2560	Bidding	2026-02-25*	2026-04-26
PR2570	1st Batch Manufacturing	2027-04-06	2027-10-03
PR2580	1st Batch Shipping	2027-11-02	2028-03-06
PR2590	Last Batch Shipping	2028-05-13	2028-09-15
Firing Control Sytem		2026-04-30	2028-06-03
PR2600	Bidding	2026-04-30	2026-06-30
PR2610	Manufacturing	2027-06-04	2027-12-01
PR2620	Shipping	2028-01-30	2028-06-03
Lining Material		2026-04-30	2028-09-17
PR2630	Bidding	2026-04-30	2026-06-30
PR2640	1st Batch Manufacturing	2026-12-09	2027-05-08
PR2650	1st Batch Shipping	2027-06-07	2027-09-20
PR2660	Last Batch Shipping	2028-06-04	2028-09-17
Steel Structure and Duct		2026-12-07	2028-07-31
PR2670	Bidding	2026-12-07	2027-02-20
PR2680	1st Batch Manufacturing	2027-03-22	2027-07-20
PR2690	1st Batch Shipping	2027-09-18	2028-01-21
PR2700	Last Batch Shipping	2028-03-28	2028-07-31
A05 Butts Treatment		2026-03-02	2028-07-31
Hook Bridge Crane		2026-05-30	2028-07-31
PR2710	Bidding	2026-05-30	2026-07-29*
PR2720	1st Batch Manufacturing	2027-02-04	2027-07-04
PR2730	1st Batch Shipping	2027-08-03	2027-12-06
PR2740	Last Batch Shipping	2028-03-28	2028-07-31
Equipment and Silo, etc.		2026-03-02	2028-07-31
PR2750	Bidding	2026-03-02	2026-05-01
PR2760	1st Batch Manufacturing	2027-01-05	2027-07-04
PR2770	1st Batch Shipping	2027-08-03	2027-12-06
PR2780	Last Batch Shipping	2028-03-28	2028-07-31
A06 Solid Pitch Storage		2026-04-09	2028-04-05
Equipment		2026-04-09	2028-04-05
PR2790	Bidding	2026-04-09	2026-06-08
PR2800	Manufacturing	2027-05-06	2027-11-02
PR2810	Shipping	2027-12-02	2028-04-05
A07 Pitch Melting Shop		2026-03-20	2028-02-24
Equipment and Silo, etc.		2026-03-20	2028-02-24

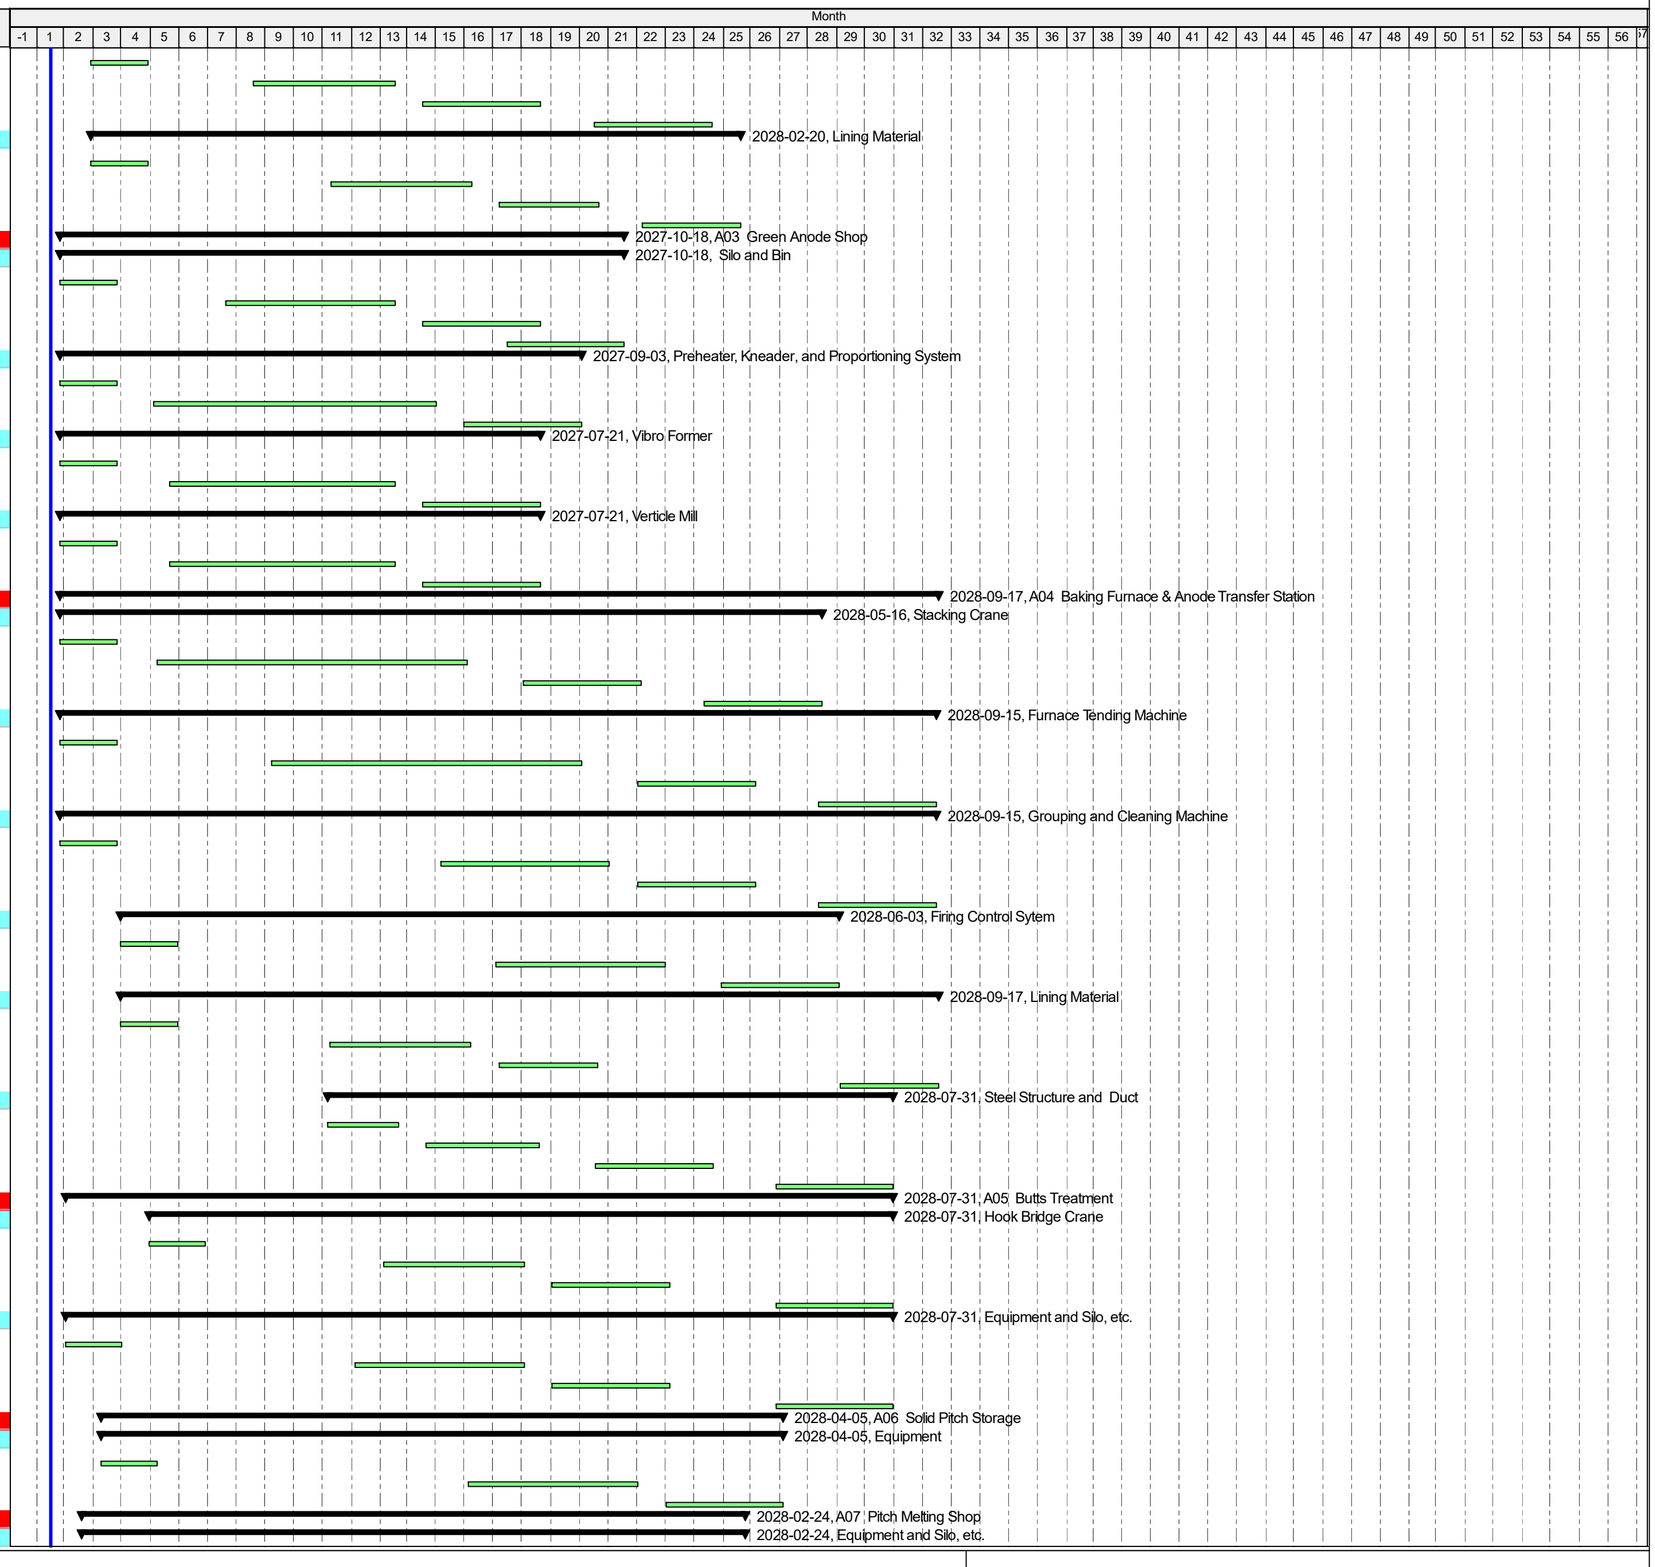

Remaining Level of Effort | Actual Work | Critical Remaining Work | summary
Actual Level of Effort | Remaining Work | Milestone

Project Schedule(Level 3)

Activity ID	Activity Name	Start	Finish
PR2820	Bidding	2026-03-20	2026-05-19
PR2830	Manufacturing	2027-02-24	2027-09-22
PR2840	Shipping	2027-10-22	2028-02-24
A08	Baking Furnace Fume Treatment Center	2026-02-15	2029-01-05
Equipment and Material		2026-02-15	2029-01-05
PR2850	Bidding	2026-02-15	2026-04-10*
PR2860	1st Batch Manufacturing	2026-11-27	2027-08-04
PR2870	1st Batch Shipping	2027-09-03	2028-01-06
PR2880	2nd Batch Shipping	2028-09-02	2029-01-05
A09	Calcination Fume Treatment Center	2026-02-15	2027-11-20
Equipment and Material		2026-02-15	2027-11-20
PR2890	Bidding	2026-02-15	2026-04-10
PR2900	Manufacturing	2026-10-11	2027-06-18
PR2910	Shipping	2027-07-18	2027-11-20
A10	Anode Rodding Shop	2026-03-02	2028-09-30
Overhead Bridge Crane		2026-06-01	2028-09-30
PR2920	Bidding	2026-06-01	2026-08-01*
PR2930	1st Batch Manufacturing	2027-03-01	2027-07-29
PR2940	1st Batch Shipping	2027-08-28	2027-12-31
PR2950	2nd Batch Shipping	2028-05-28	2028-09-30
Frequency Induction Furnace		2026-03-02	2028-09-15
PR2960	Bidding	2026-03-02	2026-05-01
PR2970	1st Batch Manufacturing	2026-12-15	2027-06-13
PR2980	1st Batch Shipping	2027-07-13*	2027-11-15
PR2990	2nd Batch Shipping	2028-05-13	2028-09-15
Other Equipment and Material		2026-03-02	2028-09-30
PR3000	Bidding	2026-03-02	2026-05-01
PR3010	1st Batch Manufacturing	2026-06-02	2027-03-29
PR3020	1st Batch Shipping	2027-04-28	2027-08-31
PR3030	Last Batch Shipping	2028-05-28	2028-09-30
A11	Bath Treatment System	2026-03-02	2028-06-30
Equipment		2026-03-02	2028-06-30
PR3040	Bidding	2026-03-02	2026-05-01
PR3050	1st Batch Manufacturing	2027-01-31	2027-10-28
PR3060	1st Batch Shipping	2027-11-27	2028-03-31
PR3070	2nd Batch Shipping	2028-02-26	2028-06-30
A12	Stem and Stub Repair Workshop	2026-03-30	2028-09-15
Equipment		2026-03-30	2028-09-15
PR3080	Bidding	2026-03-30	2026-05-29
PR3090	1st Batch Manufacturing	2027-08-31	2028-02-27
PR3100	1st Batch Shipping	2028-03-28	2028-07-31
PR3110	2nd Batch Shipping	2028-05-13	2028-09-15
A13	Waste Heat Boiler Room	2026-03-30	2027-11-05
Equipment		2026-03-30	2027-11-05
PR3120	Bidding	2026-03-30	2026-05-29
PR3130	Manufacturing	2026-09-06	2027-06-03
PR3140	Shipping	2027-07-03	2027-11-05
A14	Heat Transfer Medium Boiler and Pump Room	2026-03-30	2028-02-04
Equipment		2026-03-30	2028-02-04
PR3150	Bidding	2026-03-30	2026-05-29
PR3160	Manufacturing	2026-12-06	2027-09-02
PR3170	Shipping	2027-10-02	2028-02-04
U00	Utilities	2026-03-02	2029-06-17
U01	330kV Power Distribution Device	2026-03-02	2028-07-06
Incoming and Feeder Equipment, etc.		2026-03-02	2028-07-06
PR3180	Bidding	2026-03-02	2026-05-01
PR3190	1st Batch Manufacturing	2026-12-22	2027-07-20
PR3200	1st Batch Shipping	2027-08-19	2027-12-22
PR3210	2nd Batch Shipping	2028-03-03	2028-07-06
U02	330/10.5kV Substation and Center Control Room of the Smelter	2026-03-15	2028-07-31
Transformer, Switchgear, etc.		2026-03-15	2028-07-31
PR3220	Bidding	2026-03-15	2026-05-14
PR3230	1st Batch Manufacturing	2026-09-16	2027-05-14
PR3240	1st Batch Shipping	2027-06-13	2027-10-16
PR3250	2nd Batch Shipping	2028-03-28	2028-07-31
U03	Rectifier Station	2026-03-02	2028-09-20
Rectifier & Transformer		2026-03-02	2028-09-20
PR3260	Bidding	2026-03-02	2026-05-01
PR3270	1st Batch Manufacturing	2026-05-02	2027-05-16
PR3280	1st Batch Shipping	2027-07-08	2027-11-10
PR3290	2nd Batch Shipping	2028-05-18	2028-09-20
Capacitor and Harmonic Treatment Device		2026-05-02	2028-09-20
PR3300	Bidding	2026-05-02	2026-07-31
PR3310	1st Batch Manufacturing	2026-12-14	2027-08-11
PR3320	1st Batch Shipping	2027-08-12	2027-11-10

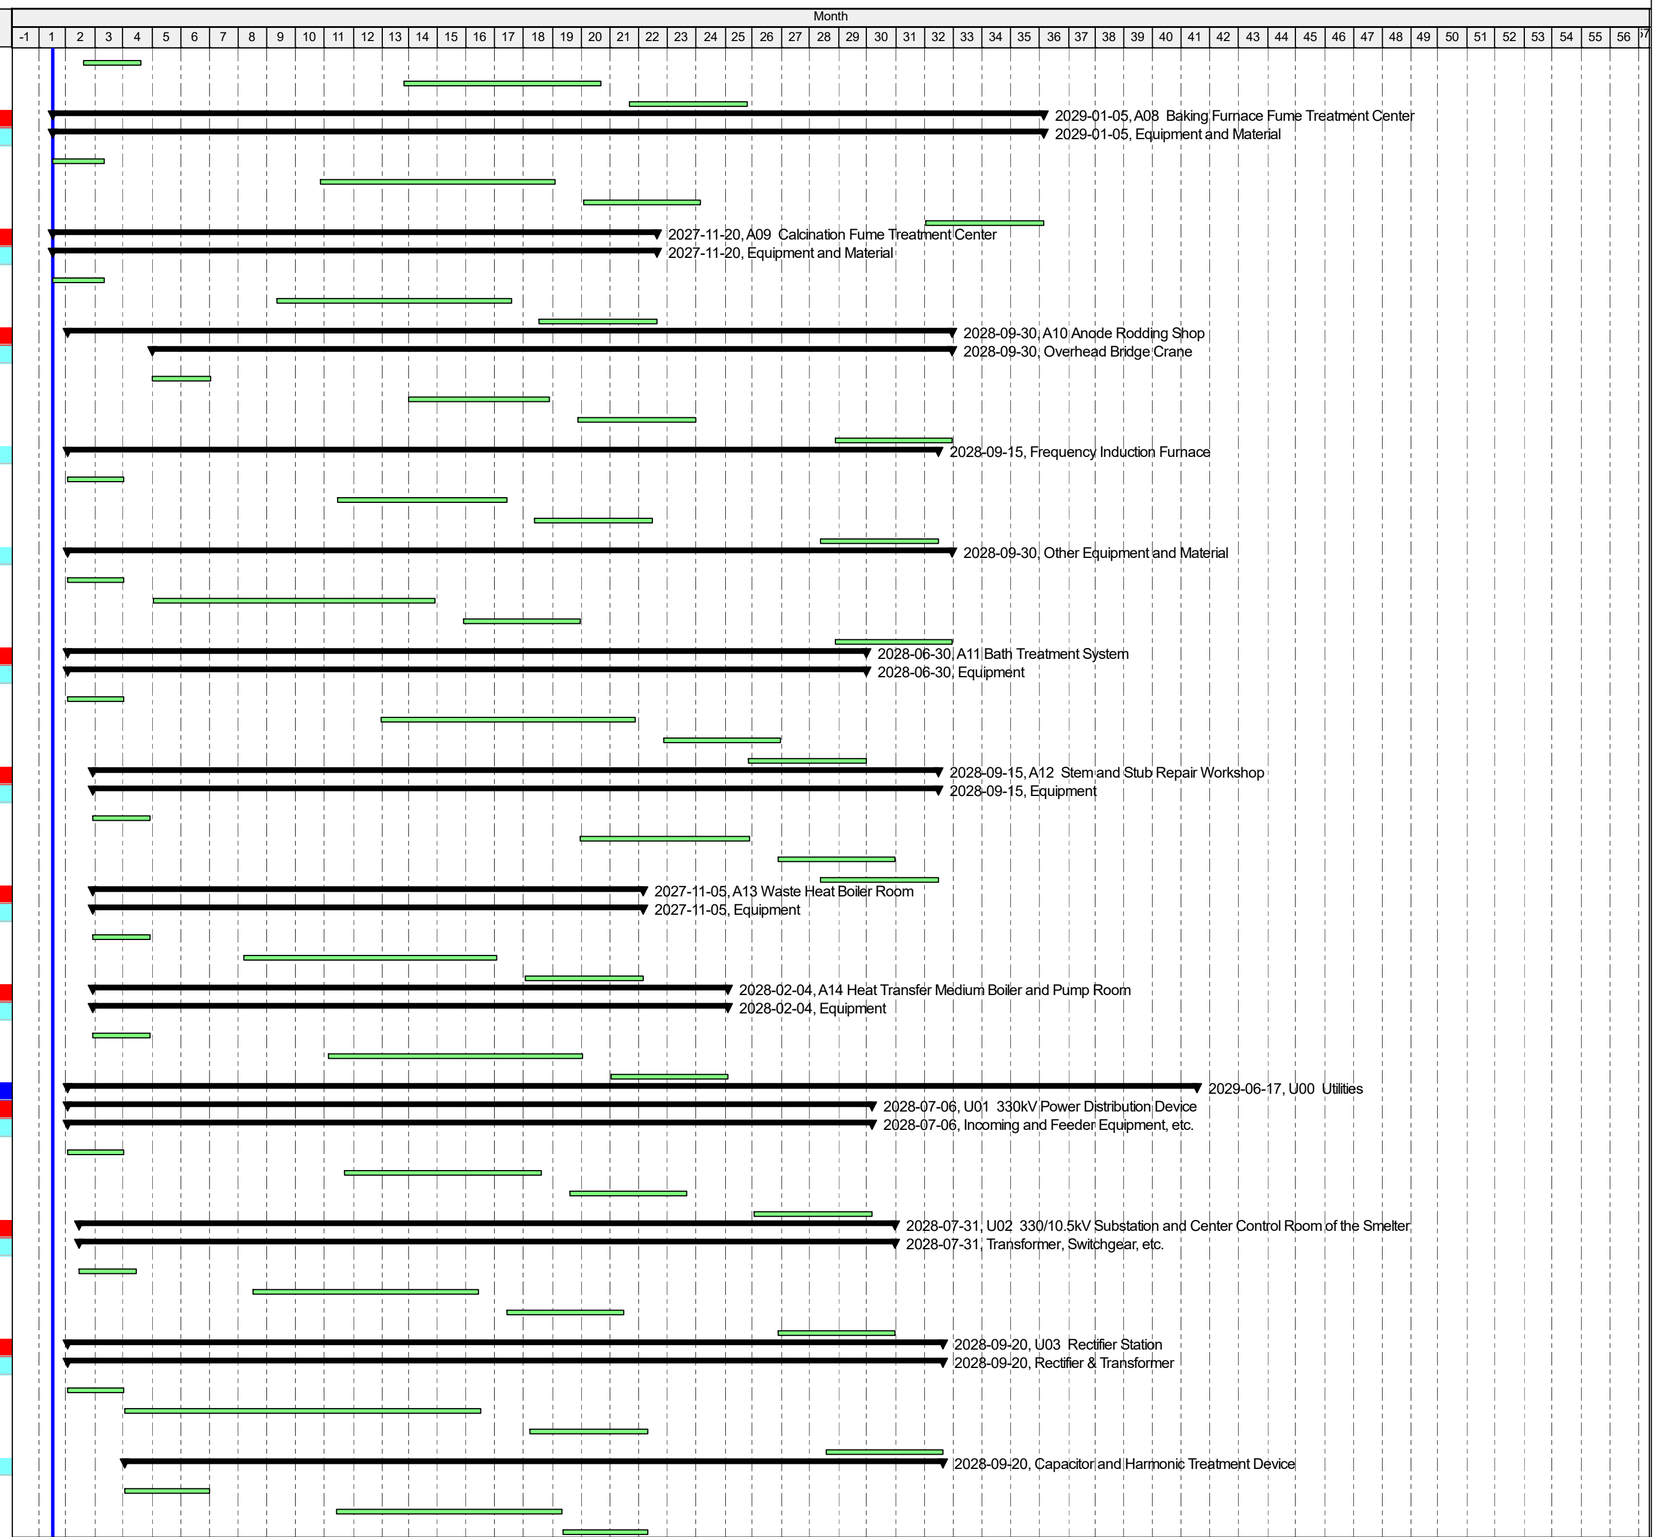

Remaining Level of Effort | Actual Work | Critical Remaining Work | summary
Actual Level of Effort | Remaining Work | Milestone

Project Schedule(Level 3)

Activity ID	Activity Name	Start	Finish
PR3330	2nd Batch Shipping	2028-06-22	2028-09-20
U06	11kV Distribution Room in Anode Area	2026-04-14	2027-11-20
Equipment		2026-04-14	2027-11-20
PR3340	Bidding	2026-04-14	2026-06-15
PR3350	Manufacturing	2027-01-09	2027-07-08
PR3360	Shipping	2027-08-07	2027-11-20
U07	Diesel Generator Room	2026-05-15	2027-10-11
Equipment		2026-05-15	2027-10-11
PR3370	Bidding	2026-05-15	2026-07-14
PR3380	Manufacturing	2026-12-10	2027-05-09
PR3390	Shipping	2027-06-08	2027-10-11
U09	Compressor Station	2026-05-15	2027-11-06
Equipment		2026-05-15	2027-11-06
PR3400	Bidding	2026-05-15	2026-07-14*
PR3410	Manufacturing	2026-10-07	2027-06-04
PR3420	Shipping	2027-07-04	2027-11-06
U10	Water Supply Pressurized Pump House	2026-04-30	2027-12-31
Pump		2026-04-30	2027-12-31
PR3430	Bidding	2026-04-30	2026-06-29
PR3440	Manufacturing	2027-03-01	2027-07-29
PR3450	Shipping	2027-08-28	2027-12-31
Unit U11-U20		2026-05-30	2028-05-31
Pump, Cooling Tower, and Water Treatment Equipment		2026-05-30	2028-05-31
PR3460	1st Batch Bidding	2026-05-30	2026-08-29
PR3470	1st Batch Manufacturing	2027-02-28	2027-07-28
PR3480	1st Batch Shipping	2027-08-28	2027-12-31
PR3490	Last Batch Shipping	2028-01-27	2028-05-31
U22	Comprehensive Maintenance Workshop	2026-03-30	2028-06-25
Equipment		2026-03-30	2028-06-25
PR3500	Bidding	2026-03-30	2026-05-29
PR3510	Manufacturing	2027-07-26	2027-12-23*
PR3520	Shipping	2028-02-21	2028-06-25
U23	Pot Maintenance Shop	2026-03-02	2027-07-21
Equipment (Bridge Crane and Intermediate Frequency Furnace)		2026-03-02	2027-07-21
PR3530	Bidding	2026-03-02	2026-05-01
PR3540	Manufacturing	2026-05-02	2027-01-26
PR3550	Shipping	2027-03-18	2027-07-21
U24	Carbon Repair Room	2026-03-30	2028-05-06
Equipment		2026-03-30	2028-05-06
PR3560	Bidding	2026-03-30	2026-05-29
PR3570	Manufacturing	2027-07-26	2027-12-23
PR3580	Shipping	2028-01-02	2028-05-06*
U25	General Warehouse	2026-03-30	2027-10-17
Equipment		2026-03-30	2027-10-17
PR3590	Bidding	2026-03-30	2026-05-29
PR3600	Manufacturing	2026-12-16	2027-05-15
PR3610	Shipping	2027-06-14	2027-10-17
U27	Truck Scale	2026-06-30	2028-02-25
Equipment		2026-06-30	2028-02-25
PR3620	Bidding	2026-06-30	2026-08-29
PR3630	Manufacturing	2027-05-26	2027-09-23
PR3640	Shipping	2027-10-23	2028-02-25
U31	Piping and Cable Tray Network	2027-02-21	2029-06-17
Material		2027-02-21	2029-06-17
PR3650	Bidding	2027-02-21	2027-04-23
PR3660	1st Batch Manufacturing	2027-04-23	2027-07-22
PR3670	1st Batch Shipping	2027-07-23	2027-11-25
PR3680	Last Batch Shipping	2029-02-12	2029-06-17
U33	Natural Gas Press Regulating Station	2026-06-30	2028-04-20
Equipment		2026-06-30	2028-04-20
PR3690	Bidding	2026-06-30	2026-08-29
PR3700	Manufacturing	2027-05-21	2027-11-17
PR3710	Shipping	2027-12-17	2028-04-20
Process Material		2026-07-01	2029-06-17
PR3720	1st Batch Bidding	2026-07-01	2026-08-31
PR3730	1st Batch Manufacturing	2026-09-01	2026-11-30
PR3740	1st Batch Shipping	2026-12-01	2027-04-05
PR3750	Last Batch Shipping	2029-02-12	2029-06-17
Management and Welfare Facilities		2026-08-23	2028-02-14
Equipment and Material		2026-08-23	2028-02-14
PR3760	1st Batch Bidding	2026-08-23	2026-10-23
PR3770	1st Batch Manufacturing	2026-10-24	2027-02-21
PR3780	1st Batch Shipping	2027-03-23	2027-07-26
PR3790	2nd Batch Shipping	2027-10-12	2028-02-14
Soil Treatment Package by Employer		2026-04-14	2027-05-15

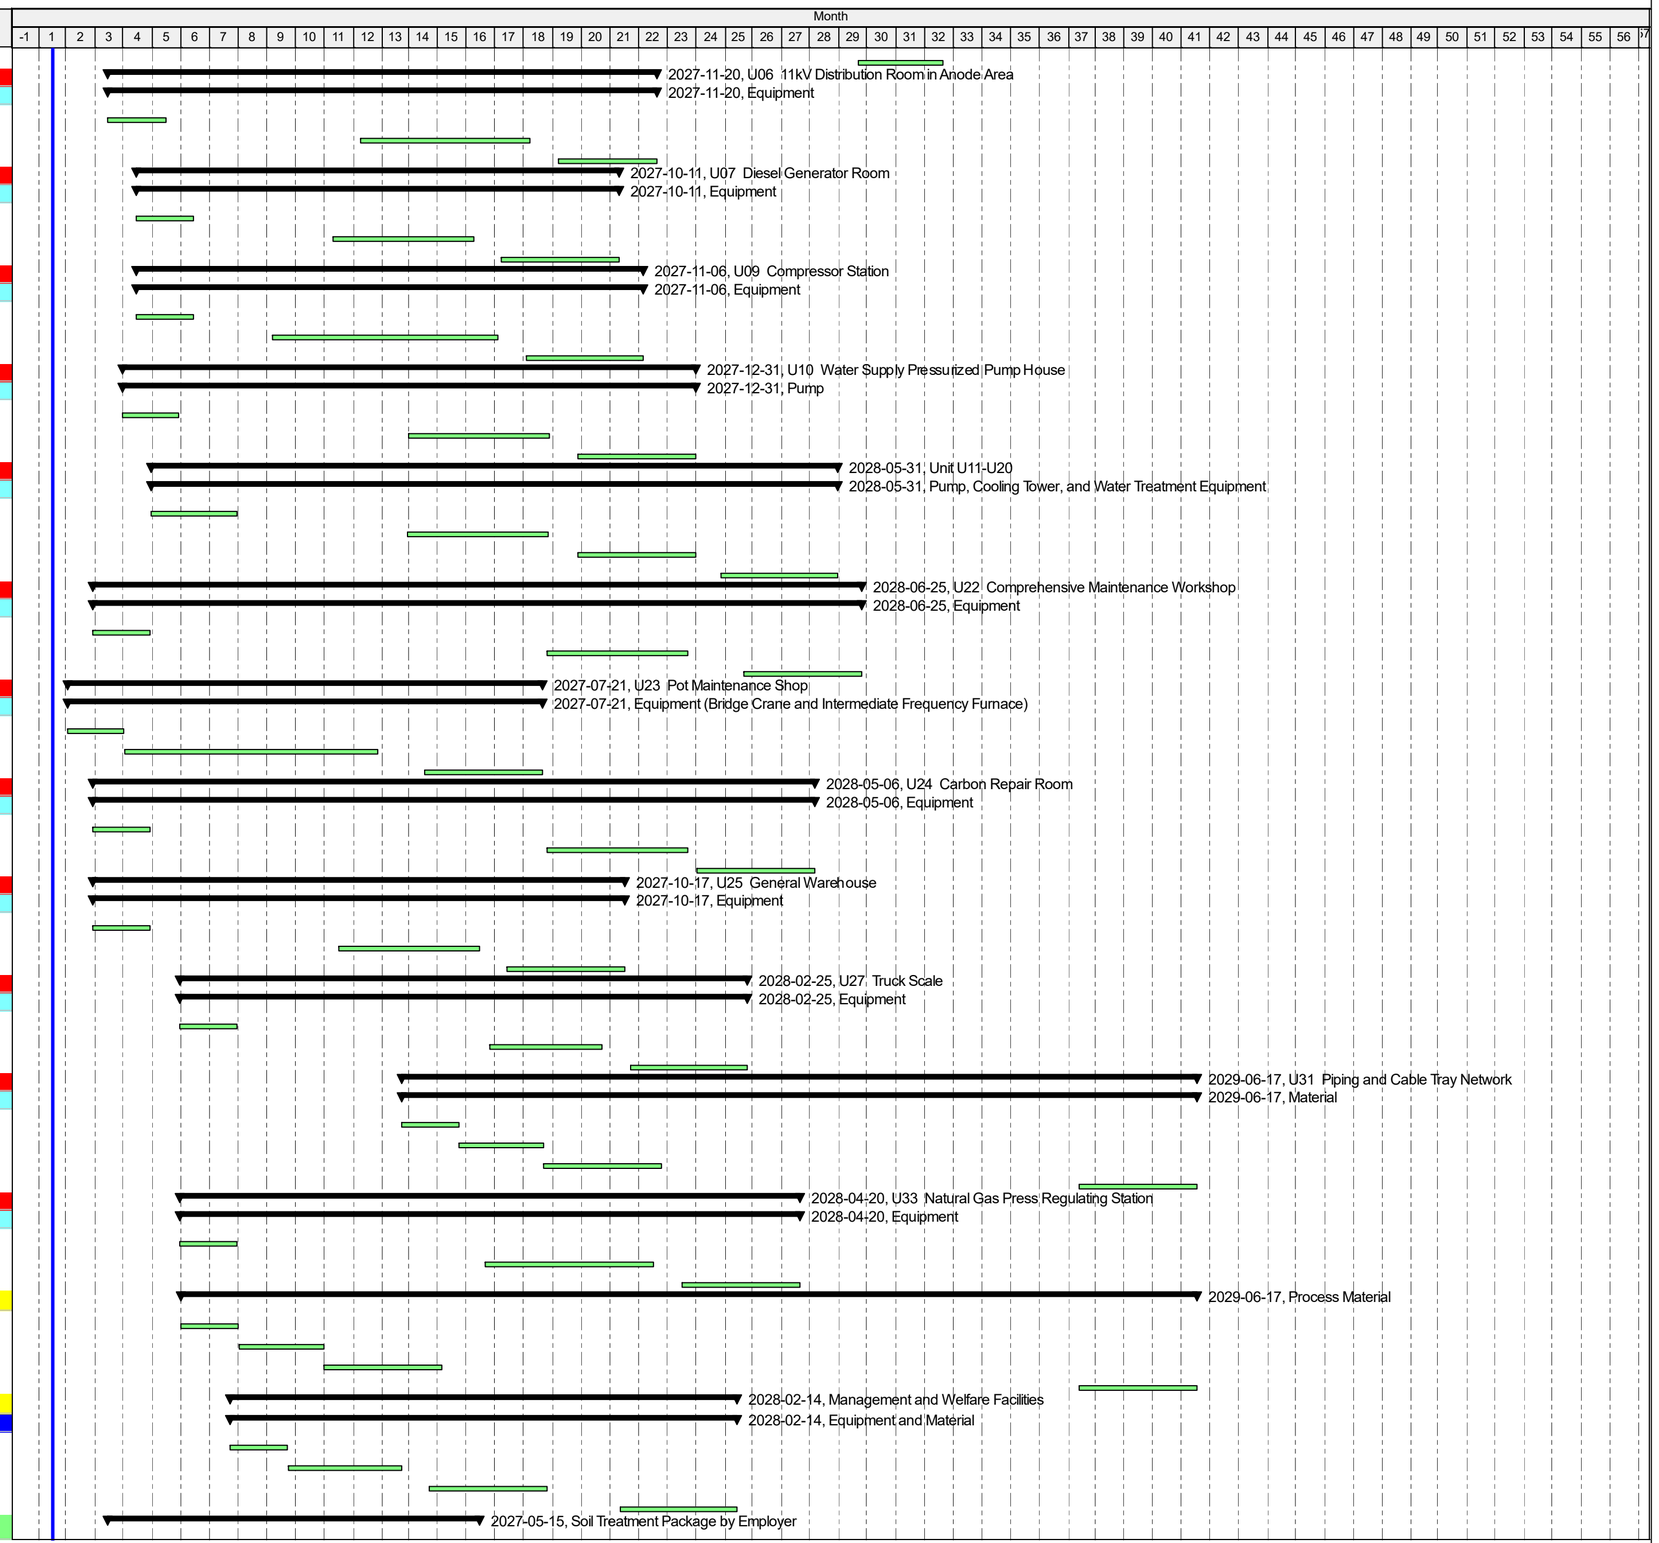

Remaining Level of Effort | Actual Work | Critical Remaining Work | summary
Actual Level of Effort | Remaining Work | Milestone

Project Schedule(Level 3)

Activity ID	Activity Name	Start	Finish
Soil Treatment		2026-04-14	2027-05-15
ST1010	Zone A1 (Utilities: U22, U25, A1201, etc.)	2026-04-14	2026-07-15*
ST1020	Zone A2 (Carbon, Potroom, etc.)	2026-07-16	2026-08-15
ST1030	Zone A3 (Area A04, A08, S11, S13, U23, etc.)	2026-08-17	2026-10-15
ST1040	Zone B (Potroom, Anode Rodding Shop, etc.)	2026-10-16	2026-12-15
ST1050	Zone C (Potroom, Casthouse, Administration)	2026-12-16	2027-01-15
ST1060	Zone D (Potroom, Alumina Silo, Rectifier Station)	2027-01-17	2027-03-15
ST1070	Zone E (Potroom, Laydown Area)	2027-03-16	2027-04-15
ST1080	Zone F (Potroom, Laydown Area)	2027-04-16	2027-05-15
Construction		2026-02-15	2030-02-11
M06 and Temporary Facilities for Installation Package (a)		2026-02-16	2027-12-07
Subcontractors Selection and Award		2026-02-16	2026-04-17
CON7270	Subcontractors Selection and Award	2026-02-16	2026-04-17
Subcontractor Mobilize on Site		2026-04-17	2026-08-14
CON7280	Subcontractor Mobilize on Site	2026-04-17	2026-08-14
Temporary Facilities		2026-08-14	2027-07-09
CON7290	Camp	2026-08-14	2027-02-13
CON7300	Site Office	2027-01-16	2027-03-16
CON7310	Temporary Fence	2026-08-14	2027-07-09
M06 Plant Fence, Gate and Guard Room		2027-09-09	2027-12-07
CON7320	Installation of Equipment	2027-09-09	2027-12-07
Temporary Facilities for Installation Package (b)		2026-05-25	2027-08-20
CON7330	Subcontractors Selection and Award	2026-05-25	2026-09-22
CON7340	Subcontractor Mobilize on Site	2026-09-22	2027-02-19
CON7350	Installation Facilities	2027-02-19	2027-08-20
Batching Plant Operation Service Package (1)		2026-02-20	2029-06-28
BOQ Preparation		2026-02-20	2026-03-12
CON7360	BOQ Preparation	2026-02-20	2026-03-12
Package Selection and Award		2026-03-12	2026-07-10
CON7370	Bidding	2026-03-12	2026-04-16
CON7380	Contractor Evaluation	2026-04-16	2026-05-11
CON7390	Employer Evaluation and Award	2026-05-11	2026-06-10
CON7400	Advance Payment	2026-06-10	2026-07-10
Subcontractor Mobilize on Site		2026-07-10	2026-07-30
CON7410	Service Subcontractor Mobilize on Site	2026-07-10	2026-07-30
Construction and Trial Operation by the Employer		2026-04-16	2026-10-15
CON7420	EPC of the Batching Plant 1 (60+60)	2026-04-16	2026-07-30
CON7430	Batching Plant 1 Trial Operation	2026-07-30	2026-08-14
CON7440	EPC of the Batching Plant 2 (120+120)	2026-06-02	2026-09-30
CON7450	Batching Plant 2 Trial Operation	2026-09-30	2026-10-15
Batching Plant 1 Operation		2026-08-14	2029-06-28
CON7460	Batching Plant 1 Operation	2026-08-14	2029-06-28
Batching Plant 2 Operation		2026-11-01	2028-08-31
CON7470	Batching Plant 2 Operation	2026-11-01	2028-08-31*
Civil Quality Test Service Package (2)		2026-02-17	2029-08-29
BOQ Preparation		2026-02-17	2026-03-09
CON7480	BOQ Preparation	2026-02-17	2026-03-09
Packages Selection and Award		2026-03-09	2026-07-12
CON7490	Bidding	2026-03-09	2026-03-24
CON7500	Tendering	2026-03-24	2026-04-18
CON7510	Contractor Evaluation	2026-04-18	2026-05-13
CON7520	Employer Evaluation and Award	2026-05-13	2026-06-12
CON7530	Advance Payment	2026-06-12	2026-07-12
Mobilize on Site		2026-06-12	2026-10-15
CON7540	Preparation	2026-06-12	2026-07-12
CON7550	Equipment Shipping	2026-07-12	2026-10-15
CON7560	Work Visa and Mobilization	2026-08-11	2026-10-15
Test Laboratory Construction		2026-08-16	2026-10-15
CON7570	Test Laboratory Construction	2026-08-16	2026-10-15
Civil Quality Test Service		2026-10-15	2029-08-29
CON7580	Civil Quality Test Service	2026-10-15	2029-08-29
Unloading on Site Package (c)		2026-03-09	2029-12-10
CON7590	Unloading Subcontractors Selection and Award	2026-03-09	2026-04-26
CON7600	Advance Payment	2026-04-26	2026-05-26
CON7610	Unloading Subcontractor Mobilize on Site	2026-05-26	2026-09-28
CON7620	Unloading on Site	2026-09-28	2029-12-10
Piling Work Package (3), (4), and (5)		2026-02-15	2028-02-29
BOQ Preparation		2026-02-15	2026-03-04
CON7630	BOQ Preparation	2026-02-15	2026-03-04
Bidding		2026-03-05	2026-04-07
CON7640	Bidding	2026-03-05	2026-03-18
CON7650	Tendering	2026-03-19	2026-04-07
Packages Selection and Award		2026-04-08	2026-06-30
CON7660	Contractor Evaluation	2026-04-08	2026-05-01

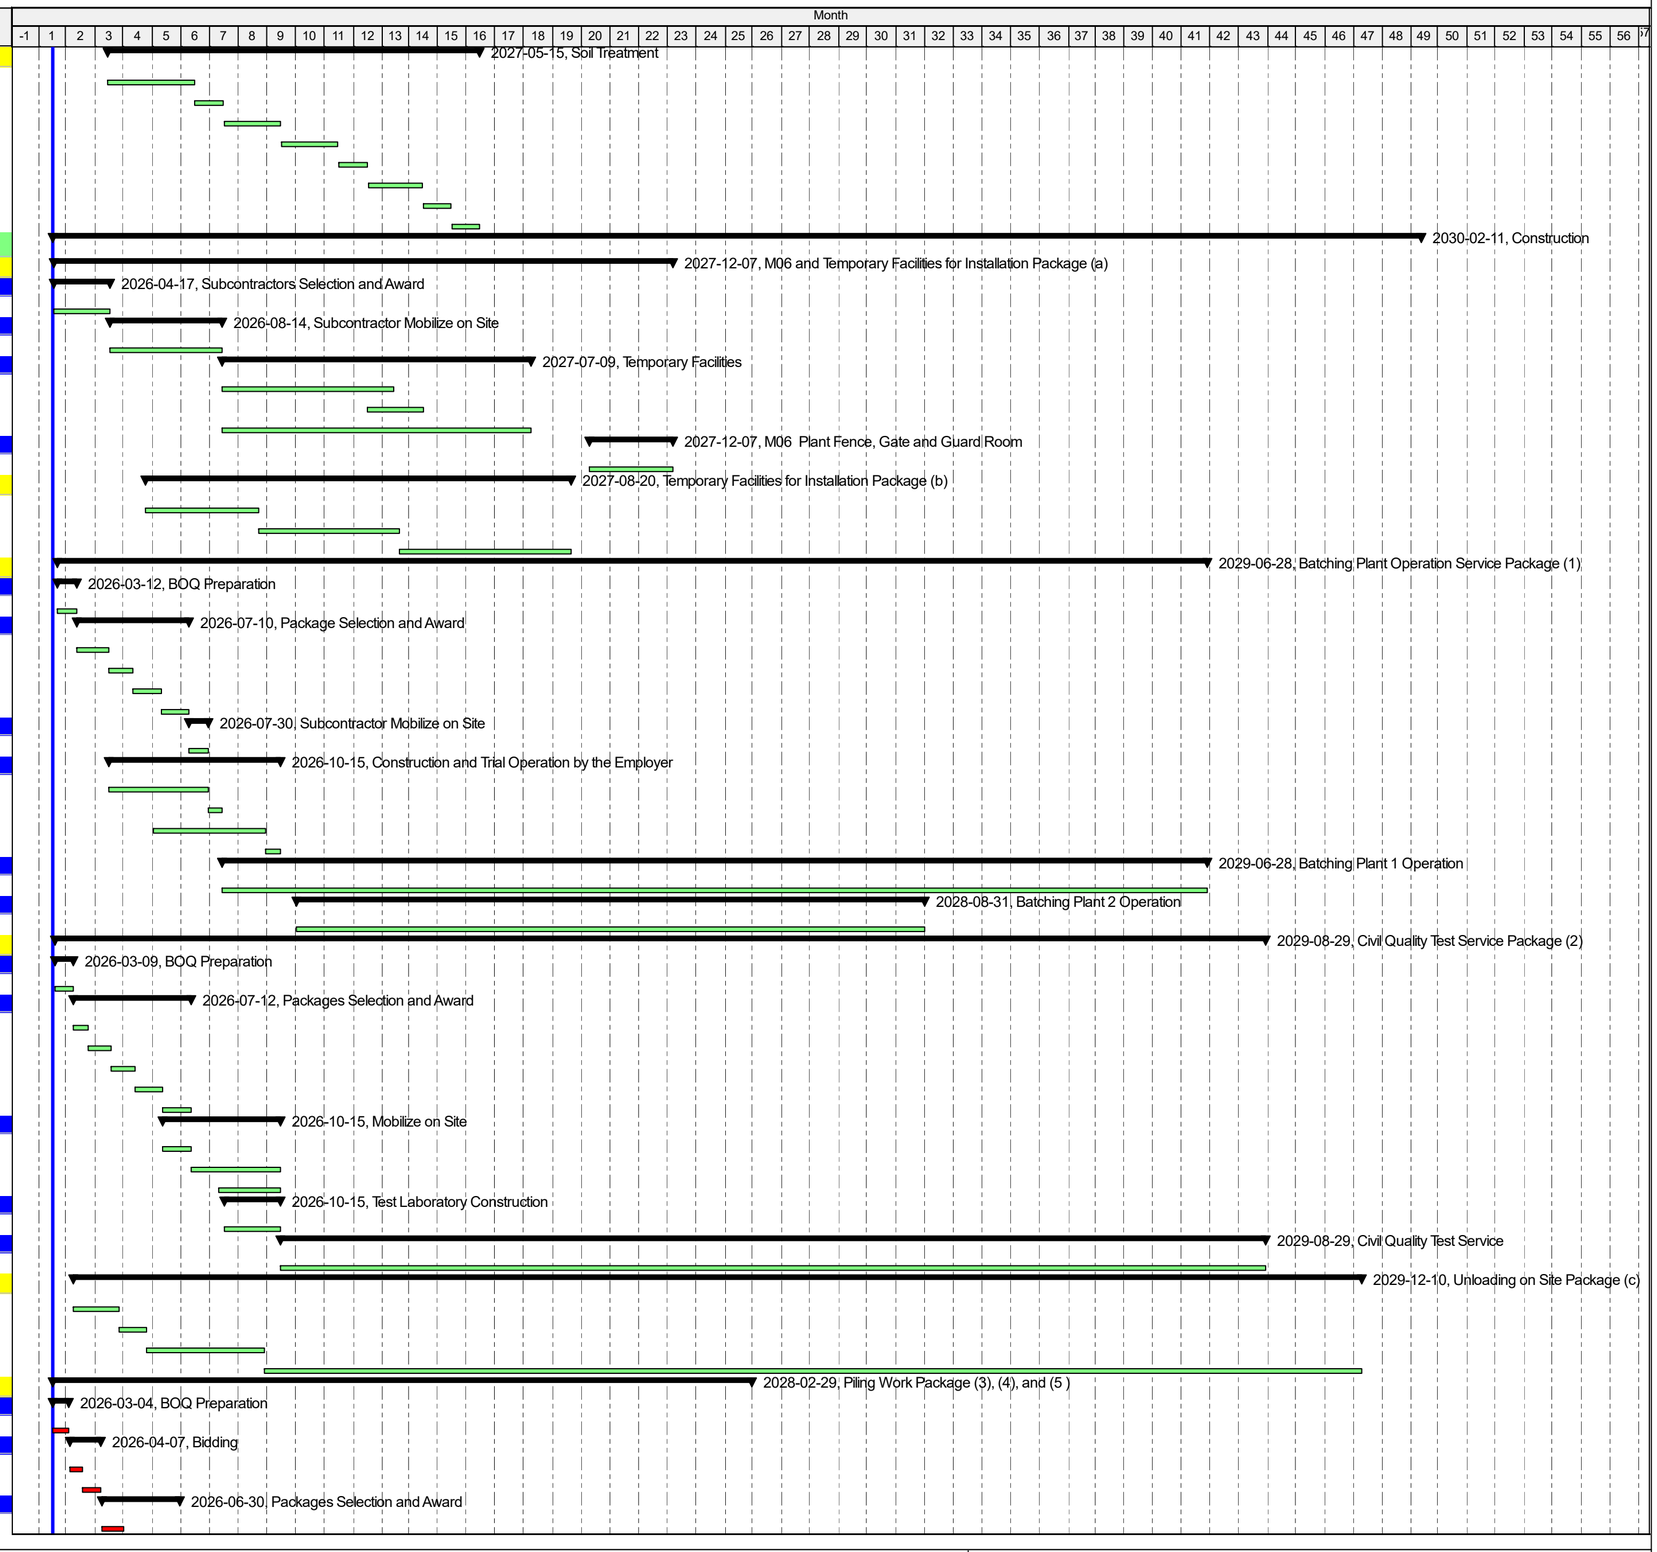

Remaining Level of Effort | Actual Work | Critical Remaining Work | summary
Actual Level of Effort | Remaining Work | Milestone

Project Schedule(Level 3)

Activity ID	Activity Name	Start	Finish
CON7670	Employer Evaluation and Award	2026-05-02	2026-05-31
CON7680	Advance Payment	2026-06-01	2026-06-30
Mobilize on Site		2026-06-01	2026-10-14
CON7690	Preparation	2026-06-01	2026-07-01
CON7700	Equipment Shipping	2026-06-17	2026-10-14
CON7710	Work Visa and Mobilization	2026-07-02	2026-09-24
Cast In-situ Pile Test		2026-06-01	2026-08-04
CON7720	Preparation	2026-06-01	2026-06-20
CON7730	Cast In-situ Pile Test	2026-06-21	2026-08-04
Piling Construction		2026-09-25	2028-02-29
CON7740	Construction Preparation	2026-09-25	2026-10-14
Piling Package 1		2026-10-15	2028-02-29
S01 Potroom		2026-10-15	2028-02-29
CON7750	A-2 Zone	2026-10-15	2027-01-30
CON7760	B Zone	2027-01-01	2027-03-30
CON7770	C Zone	2027-02-01	2027-04-30
CON7780	D Zone	2027-04-01	2027-11-30
CON7790	E Zone	2027-05-01	2028-01-30
CON7800	F Zone	2027-05-31	2028-02-29
S02 Potline Gas Treatment Center		2026-10-15	2027-06-30
CON7810	A-2 Zone	2026-10-15	2026-11-30
CON7820	B Zone	2027-01-01	2027-03-01
CON7830	C Zone	2027-02-01	2027-02-28
CON7840	D Zone	2027-04-01	2027-04-30
CON7850	E Zone	2027-05-01	2027-05-30
CON7860	F Zone	2027-06-01	2027-06-30
S04 Alumina Conveying and Daly Silo		2026-11-01	2027-06-30
CON7870	A-2 Zone	2026-11-01	2027-01-30
CON7880	B Zone	2027-01-01	2027-01-30
CON7890	D Zone	2027-04-01	2027-05-30
CON7900	E Zone	2027-05-01	2027-05-30
CON7910	F Zone	2027-06-01	2027-06-30
S06 Super Dense Phase Conveying System		2026-11-01	2027-06-30
CON7920	A-2 Zone	2026-11-01	2026-11-30
CON7930	B Zone	2027-01-01	2027-01-30
CON7940	D Zone	2027-04-01	2027-04-30
CON7950	E Zone	2027-05-01	2027-05-30
CON7960	F Zone	2027-06-01	2027-06-30
S07 Anode Covering Material Storage & Conveying System		2027-01-01	2028-02-29
CON7970	A-2 Zone	2027-01-01	2027-01-30
CON7980	B Zone	2027-05-01	2027-05-30
CON7990	C Zone	2027-09-01	2027-09-30
CON8000	D Zone	2027-10-01	2027-10-30
CON8010	E Zone	2027-12-01	2027-12-30
CON8020	F Zone	2028-02-01	2028-02-29
U13 Circulating Water System for Gas Treatment Center		2026-10-15	2027-06-30
CON8030	A-2 Zone	2026-10-15	2026-10-30
CON8040	B Zone	2027-01-01	2027-01-30
CON8050	C Zone	2027-02-01	2027-03-02
CON8060	D Zone	2027-04-01	2027-04-30
CON8070	E Zone	2027-05-01	2027-05-30
CON8080	F Zone	2027-06-01	2027-06-30
U32 Potroom Trestle and Ramp		2026-12-01	2028-02-29
CON8090	A-2 Zone	2026-12-01	2027-01-30
CON8100	B Zone	2027-04-01	2027-05-30
CON8110	C Zone	2027-10-01	2027-10-30
CON8120	D Zone	2027-11-01	2027-11-30
CON8130	E Zone	2027-12-01	2028-01-30
CON8140	F Zone	2028-02-01	2028-02-29
U20 Rainwater Collecting Pond		2027-04-01	2027-09-30
CON8150	D Zone	2027-04-01	2027-04-30
CON8160	F Zone	2027-09-01	2027-09-30
U27 Truck Scale		2027-06-01	2027-06-30
CON8170	F Zone	2027-06-01	2027-06-30
M06 Gate and Guard Room		2027-06-01	2027-06-30
CON8180	F Zone	2027-06-01	2027-06-30
Piling Package 2		2026-10-15	2027-12-30
U0301 Rectifier Station		2026-10-15	2026-11-30
CON8190	A-2 Zone	2026-10-15	2026-11-30
A03 Green Anode Shop		2026-10-15	2027-01-30
CON8200	A-2 Zone	2026-10-15	2027-01-30
A0201 Calcination Shop		2026-11-01	2026-12-30
CON8210	A-2 Zone	2026-11-01	2026-12-30
A0202 Calcination Shop		2027-01-01	2027-02-28
CON8220	A-2 Zone	2027-01-01	2027-02-28

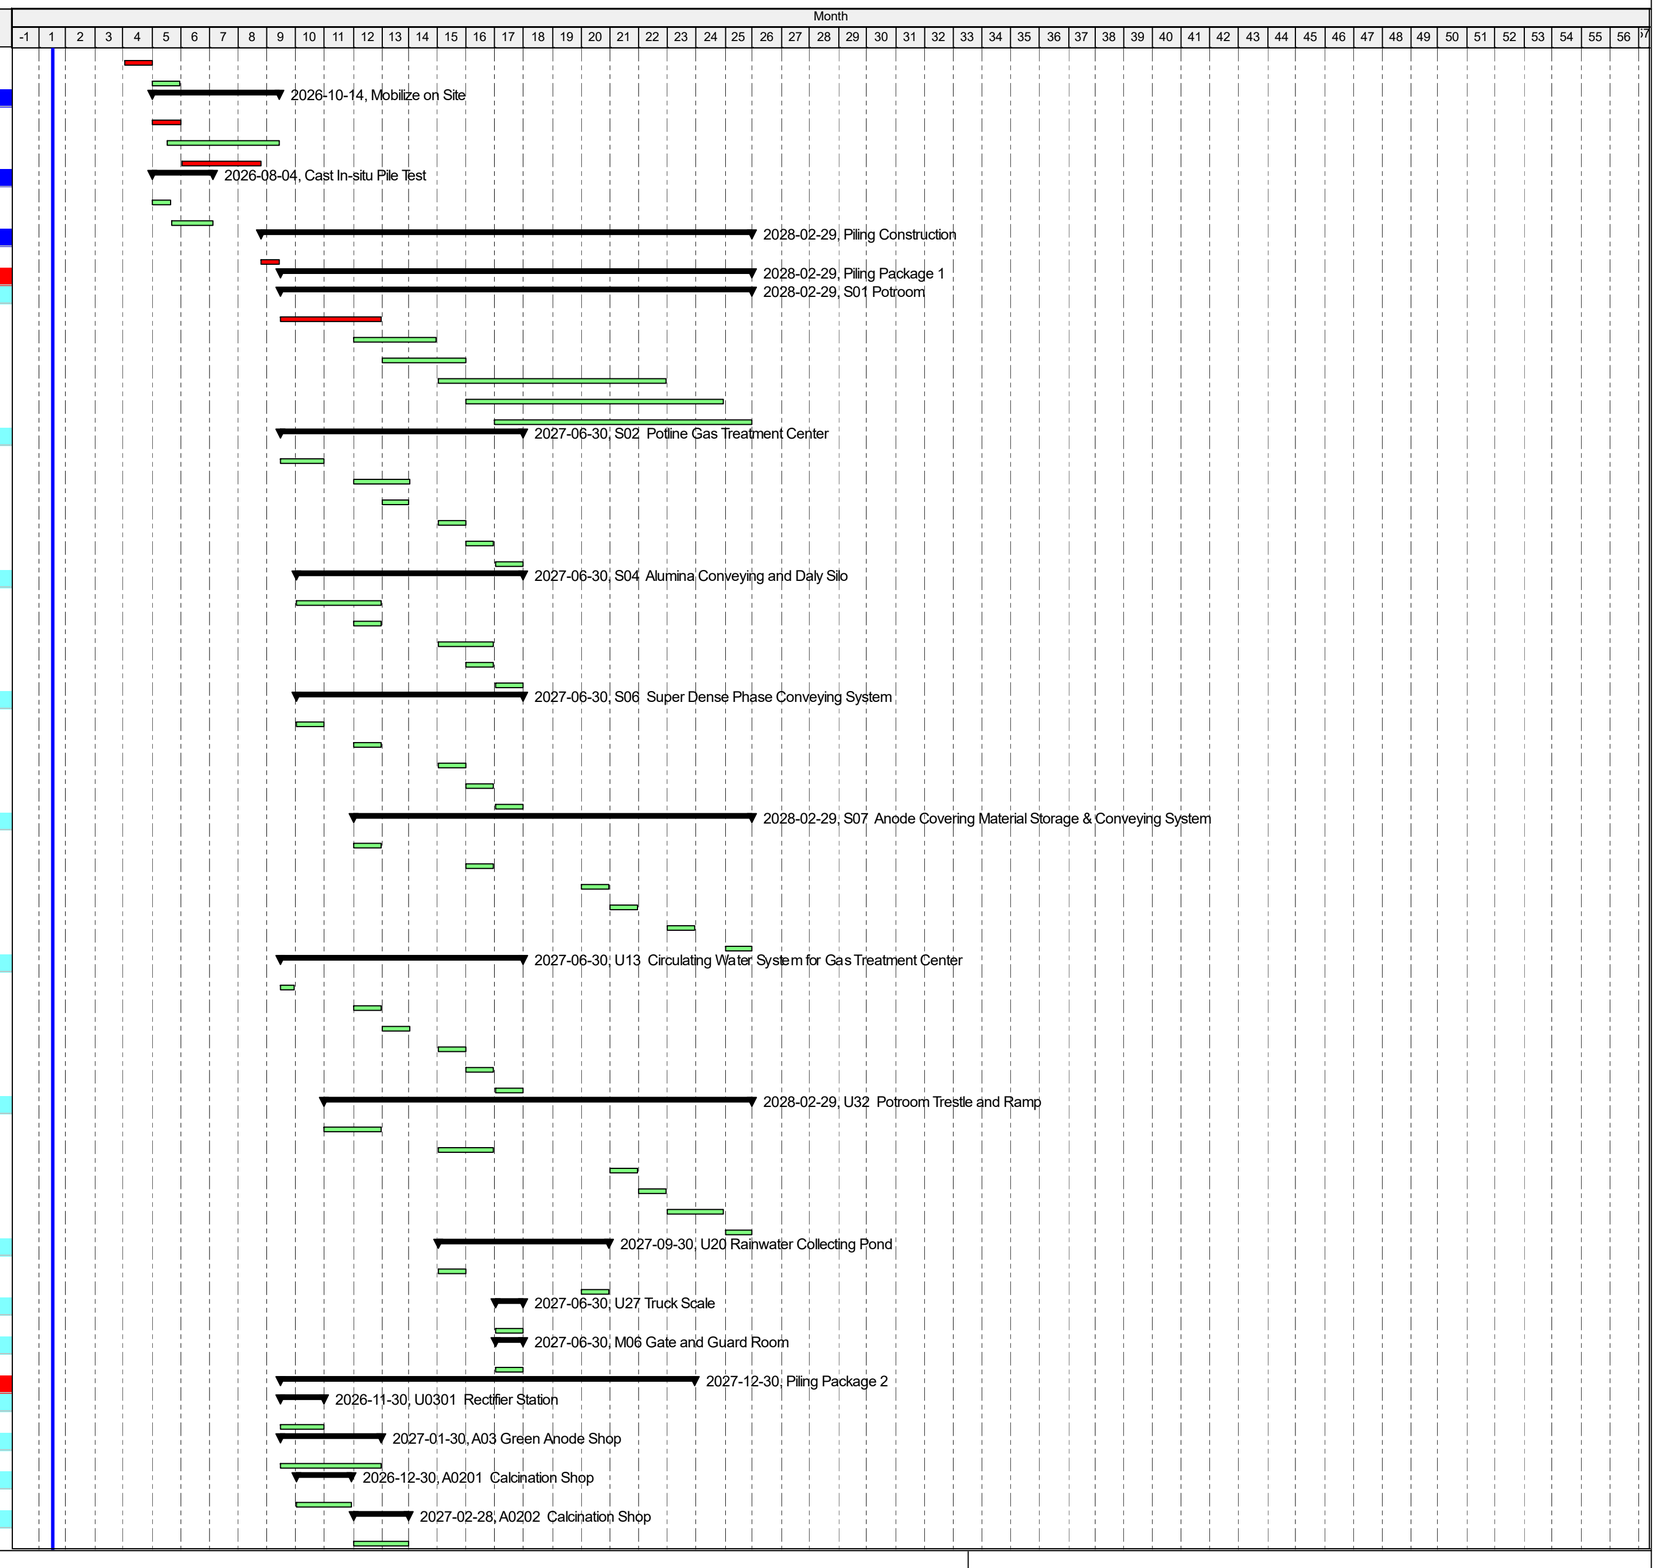

Remaining Level of Effort | Actual Work | Critical Remaining Work | summary
Actual Level of Effort | Remaining Work | Milestone

Project Schedule(Level 3)

Activity ID	Activity Name	Start	Finish
A01 GPC Storage and Conveying		2026-12-01	2027-02-28
CON8230	A-2 Zone	2026-12-01	2027-02-28
A06 Solid Pitch Storage		2027-01-01	2027-01-30
CON8240	A-2 Zone	2027-01-01	2027-01-30
A07 Pitch Melting Shop		2027-01-01	2027-02-28
CON8250	A-2 Zone	2027-01-01	2027-02-28
A09 Calcination Fume Treatment Center		2027-01-01	2027-02-28
CON8260	A-2 Zone	2027-01-01	2027-02-28
A14 Heat Transfer Medium Boiler and Pump Room		2027-02-01	2027-03-15
CON8270	A-2 Zone	2027-02-01	2027-03-15
A13, S05, U14, U24, U06, and U16		2027-03-01	2027-03-15
CON8280	A-2 Zone	2027-03-01	2027-03-15
A1001 Anode Rodding Shop		2026-10-15	2027-02-28
CON8290	A-2 Zone	2026-10-15	2027-02-28
A0501, A1101, and U15		2027-02-01	2027-02-28
CON8300	A-2 Zone	2027-02-01	2027-02-28
E01 Raw Material Conveying system		2027-03-01	2027-06-30
CON8310	D Zone	2027-03-01	2027-06-30
S03 Alumina Storage		2027-04-01	2027-06-30
CON8320	D Zone	2027-04-01	2027-06-30
U0101 330kV Power Distribution Device		2027-04-01	2027-06-30
CON8330	D Zone	2027-04-01	2027-06-30
U0201 330/10.5kV Substation and Center Control Room		2027-04-01	2027-05-30
CON8340	D Zone	2027-04-01	2027-05-30
U26 and M06		2027-04-01	2027-04-30
CON8350	D Zone	2027-04-01	2027-04-30
U05 Emergency Oil Pools and Oil Storage Facilities		2027-05-01	2027-05-30
CON8360	D Zone	2027-05-01	2027-05-30
U0102 330kV Power Distribution Device		2027-07-01	2027-12-30
CON8370	D Zone	2027-07-01	2027-12-30
U0202 330/10.5kV Substation and Center Control Room		2027-07-01	2027-12-30
CON8380	D Zone	2027-07-01	2027-12-30
U0302 Rectifier Station		2027-07-01	2027-12-30
CON8390	D Zone	2027-07-01	2027-12-30
A1201, U22, and U25		2027-02-01	2027-03-15
CON8400	A-1 Zone	2027-02-01	2027-03-15
U10 and U18		2027-03-01	2027-05-30
CON8410	A-1 Zone	2027-03-01	2027-05-30
U19 and U26		2027-03-01	2027-06-30
CON8420	A-1 Zone	2027-03-01	2027-06-30
Piling Package 3		2026-11-15	2027-09-30
U23 Reduction Pot Repair Room		2026-11-15	2027-02-28
CON8430	A-3 Zone	2026-11-15	2027-02-28
A0401 Baking Furnace & Anode Transfer Station		2026-11-15	2027-03-30
CON8440	A-3 Zone	2026-11-15	2027-03-30
A08 Baking Furnace Fume Treatment Center		2026-11-15	2027-04-30
CON8450	A-3 Zone	2026-11-15	2027-04-30
A0402 Baking Furnace & Anode Transfer Station		2027-04-01	2027-09-30
CON8460	A-3 Zone	2027-04-01	2027-09-30
S11 and S13		2027-02-01	2027-03-30
CON8470	A-3 Zone	2027-02-01*	2027-03-30
A1002 Anode Rodding Shop		2027-01-01	2027-09-30
CON8480	B Zone	2027-01-01	2027-09-30
A0502, U09, U11, U12, and A1102		2027-04-01	2027-05-30
CON8490	B Zone	2027-04-01	2027-05-30
M06 Gate and Guard Room		2027-02-01	2027-03-02
CON8510	C Zone	2027-02-01	2027-03-02
S08 Cast House		2027-04-01	2027-09-30
CON8520	C Zone	2027-04-01	2027-09-30
A1202 Stem and Stub Repair Workshop		2027-04-01	2027-05-30
CON8530	C Zone	2027-04-01	2027-05-30
S09 and S10		2027-05-01	2027-06-30
CON8540	C Zone	2027-05-01	2027-06-30
M01, M02, M03, and M04		2027-05-01	2027-09-30
CON8550	C Zone	2027-05-01	2027-09-30
S00 Aluminum Reduction Plant Civil Work Package (6) and (7)		2026-03-12	2028-09-08
BOQ Preparation		2026-03-12	2026-04-13
CON8560	BOQ Preparation	2026-03-12	2026-04-13
Bidding		2026-04-14	2026-06-08
CON8570	Bidding	2026-04-14	2026-05-04
CON8580	Tendering and Bid Clarification Meeting	2026-05-05	2026-06-08
Civil Subcontractors Selection and Award		2026-06-09	2026-09-24
CON8590	Contractor Evaluation	2026-06-09	2026-07-09
CON8600	Employer Evaluation and Award	2026-07-09	2026-08-08
CON8610	Advance Payment	2026-08-09	2026-09-24
Civil Subcontractor Mobilize on Site		2026-09-25	2027-01-24
CON8620	Civil Subcontractor Mobilize on Site	2026-09-25	2027-01-24

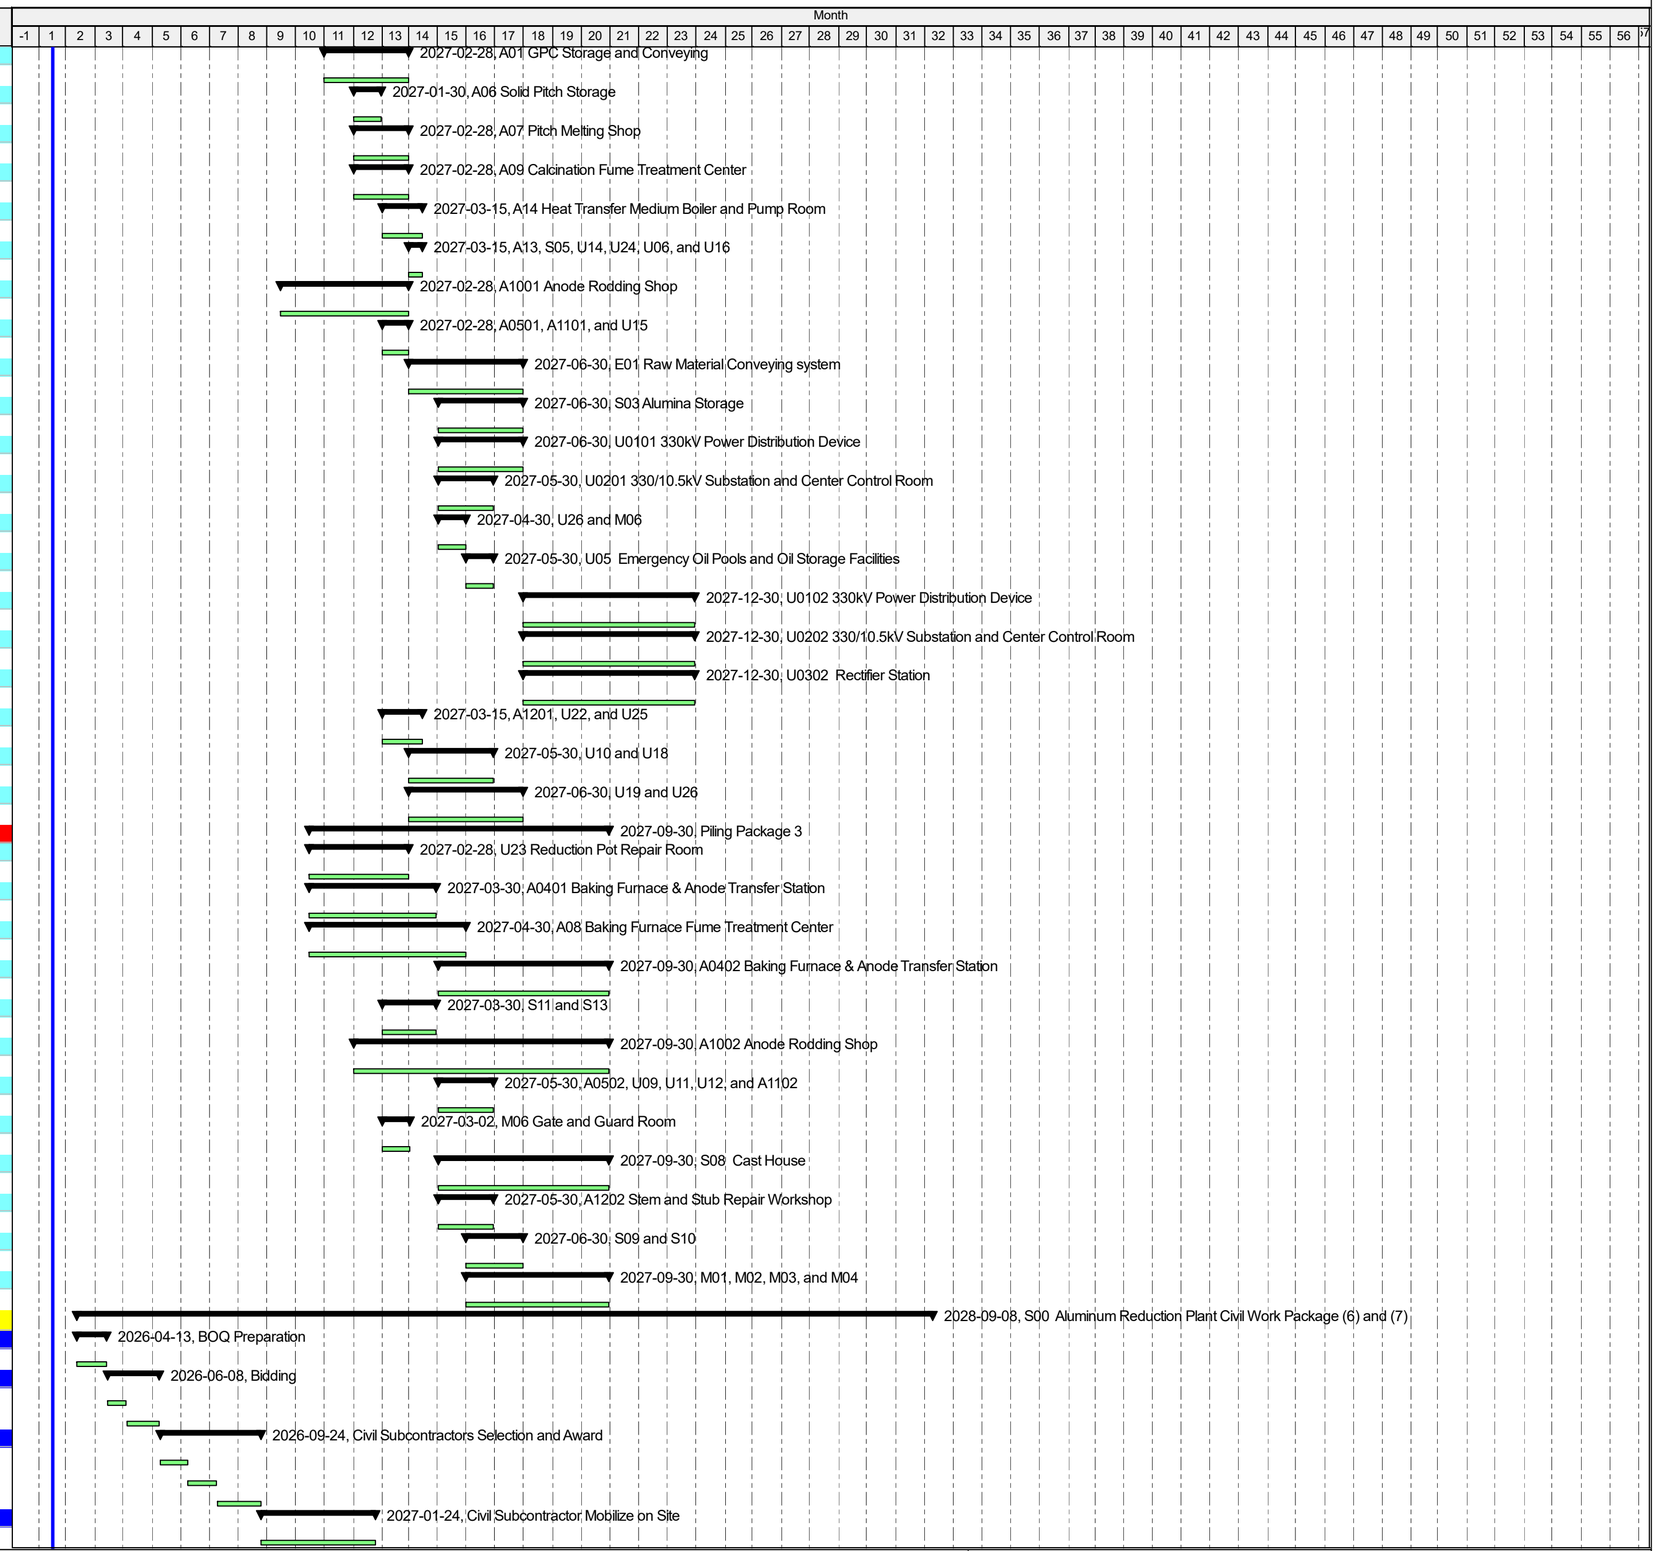

Remaining Level of Effort | Actual Work | Critical Remaining Work | summary
Actual Level of Effort | Remaining Work | Milestone

Project Schedule(Level 3)

Activity ID	Activity Name	Start	Finish
	Civil Construction	2027-01-25	2028-09-08
	S0101 Potroom	2027-01-25	2028-09-08
	Civil Work and Steel Structure	2027-01-25	2028-09-08
	Construction Preparation	2027-01-25	2027-02-24
CON8630	Construction Preparation	2027-01-25	2027-02-24
	Potroom Foundation	2027-02-25	2028-01-03
CON8640	Potroom Foundation (Zone A)	2027-02-25	2027-07-04
CON8650	Potroom Foundation (Zone B)	2027-07-05	2027-11-24
CON8660	Potroom Foundation (Zone C)	2027-11-25	2028-01-03
	Construction	2027-03-30	2028-09-08
CON8670	Steel Structure/Component Assembling	2027-03-30	2028-02-24
CON8680	Steel Structure Erection	2027-04-04	2028-02-29
CON8690	Concrete Platform	2027-05-05	2028-05-14
CON8700	Cladding of Roof and Wall, and Decoration	2027-06-04	2028-06-03
CON8710	Foundation of Pot and Busbar	2027-06-04	2028-06-03
CON8720	Concrete Floor	2027-08-04	2028-07-04
CON8730	Crane Rail Installation	2027-08-04	2028-05-04
CON8740	Water and Electricity Facilties Installation	2028-01-04	2028-08-03
CON8750	Completion of Outdoor Civil Work	2028-05-25	2028-09-08
	S0201 Potline Gas Treatment Center	2027-02-24	2028-05-15
	S020101 GTC	2027-02-24	2027-12-19
	Civil Work	2027-02-24	2027-12-19
CON8760	Construction Preparation	2027-02-24	2027-03-19
CON8770	Plant and Duct Bracket Foundation	2027-03-20	2027-05-04
CON8780	Steel Structure/Component Assembling	2027-04-20	2027-05-29
CON8790	Erection of Steel Column, Beam, and Roof Truss	2027-04-25	2027-06-24
CON8800	Foundation of Chimney ,Fan, Desulfurization system	2027-03-20	2027-05-19
CON8810	Distribution Room and Cable Trench	2027-05-05	2027-06-18
CON8820	Completion of Outdoor Civil Work	2027-11-20	2027-12-19
	S020102 GTC	2027-07-16	2028-04-04
	Civil Work	2027-07-16	2028-04-04
CON8830	Plant and Duct Bracket Foundation	2027-07-16	2027-09-30
CON8840	Steel Structure/Component Assembling	2027-08-16	2027-10-30
CON8850	Erection of Steel Column, Beam, and Roof Truss	2027-08-21	2027-11-04
CON8860	Foundation of Chimney ,Fan, Desulfurization system	2027-07-16	2027-10-15
CON8870	Distribution Room and Cable Trench	2027-10-01	2027-12-15
CON8880	Completion of Outdoor Civil Work	2028-03-07	2028-04-04
	S020103 GTC	2027-09-21	2028-05-15
	Civil Work	2027-09-21	2028-05-15
CON1010	Plant and Duct Bracket Foundation	2027-09-21	2027-11-04
CON1020	Steel Structure/Component Assembling	2027-10-21	2027-12-05
CON1030	Erection of Steel Column, Beam, and Roof Truss	2027-10-26	2027-12-10
CON1040	Foundation of Chimney ,Fan, Desulfurization system	2027-09-21	2027-11-20
CON1050	Distribution Room and Cable Trench	2027-11-05	2028-01-04
CON1060	Completion of Outdoor Civil Work	2028-04-16	2028-05-15
	S0401 Alumina Conveying System and Daly Silo	2027-04-20	2028-07-14
CON1070	Construction Preparation	2027-04-20	2027-05-19
	Foundation and Structure	2027-05-20	2027-12-20
CON1080	Daly Silo 1-1	2027-05-20	2027-07-29
CON1090	Daly Silo 1-2	2027-09-16	2027-11-14
CON1100	Daly Silo 1-3	2027-11-05	2027-12-20
	Chute Steel Structure along Potrrom	2028-04-14	2028-07-14
CON1110	steel structure 1-1	2028-05-25	2028-06-24
CON1120	steel structure 1-2	2028-06-14	2028-07-14
CON1130	steel structure 1-3	2028-04-14	2028-06-03
	S0601 Super Dense Phase Conveying System	2027-04-30	2028-06-03
	Civil Work and Steel Structure	2027-04-30	2028-06-03
	Foundation and Structure of Reacted Alumina Silo	2027-04-30	2027-11-25
CON1140	Reacted Alumina Silo 1-1	2027-04-30	2027-06-18
CON1150	Reacted Alumina Silo 1-2	2027-08-16	2027-10-05
CON1160	Reacted Alumina Silo 1-3	2027-10-06	2027-11-25
	Platform for Chute	2027-09-25	2028-06-03
CON1170	Platform for Chute 1-1	2027-09-25	2027-11-13
CON1180	Platform for Chute 1-2	2028-01-14	2028-03-05
CON1190	Platform for Chute 1-3	2028-04-14	2028-06-03
	S0701 Anode Covering Material Storage & Conveying System	2027-03-30	2028-04-14
	Civil Work and Steel Structure	2027-03-30	2028-04-14
CON1200	Foundation 1 & 2	2027-03-30	2027-04-29
CON1210	Foundation 3 & 4	2027-05-05	2027-06-03
CON1220	Foundation 5 & 6	2027-10-05	2027-11-03
CON1230	Foundation 7 & 8	2027-12-05	2028-01-03
CON1240	Installation of Steel Frame and Platform 1,2,3 & 4	2027-05-25	2027-07-15
CON1250	Installation of Steel Frame and Platform 5 & 6	2027-11-05	2027-12-25
CON1260	Installation of Steel Frame and Platform 7 & 8	2028-02-21	2028-04-14
	S1203 Aluminium Ingot Yard	2027-06-05	2027-10-20

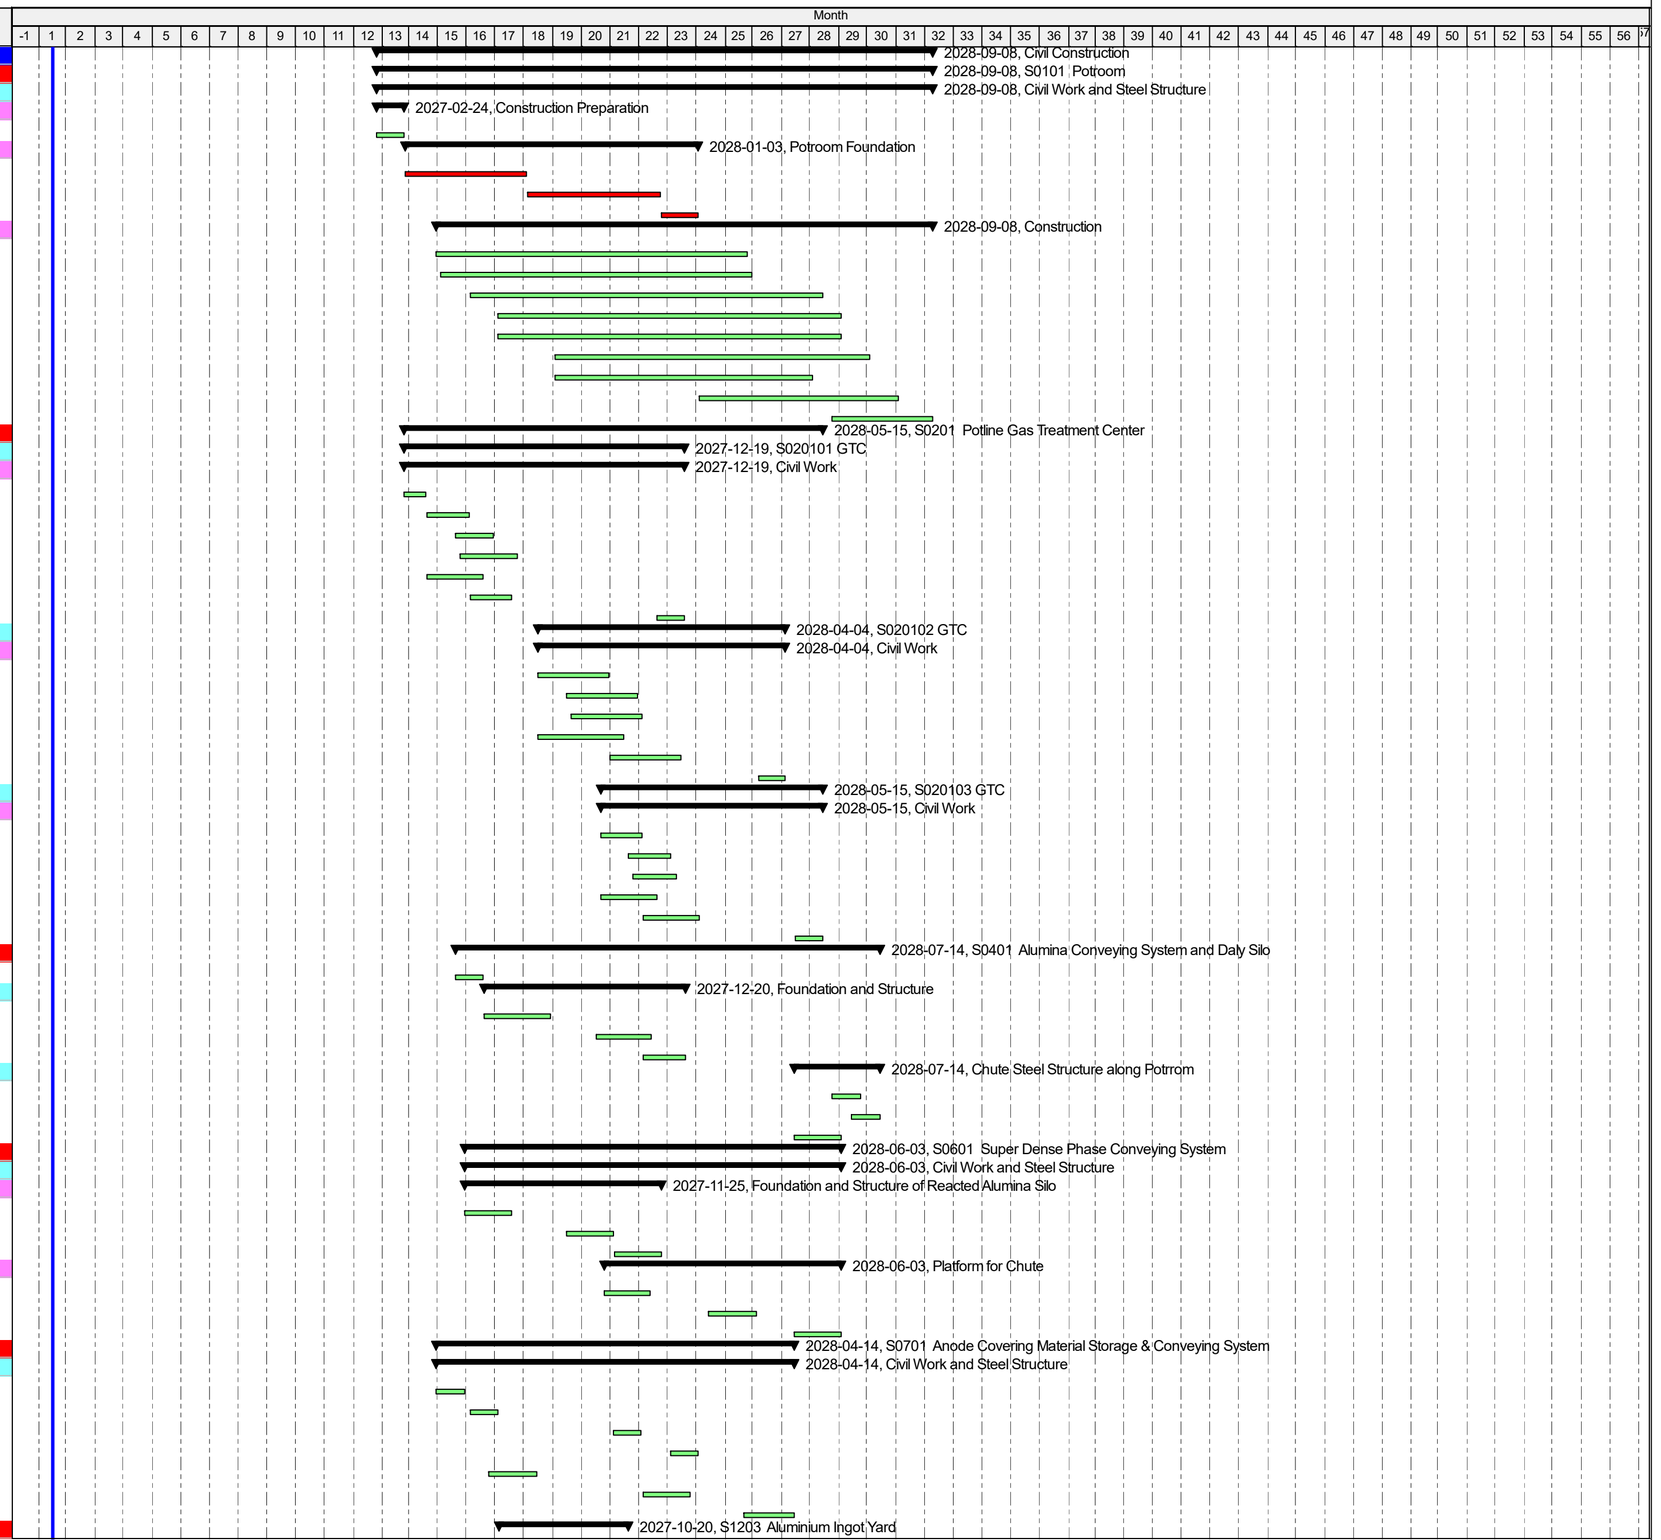

Remaining Level of Effort | Actual Work | Critical Remaining Work | summary
Actual Level of Effort | Remaining Work | Milestone

Project Schedule(Level 3)

Activity ID	Activity Name	Start	Finish
CON1270	Aluminium Ingot Yard	2027-06-05	2027-10-20
U1301 Circulating Water System for Gas Treatment Center		2028-03-01	2028-04-29
CON1280	Civil Work and Steel Structure	2028-03-01	2028-04-29
U20 Rainwater Collecting Pond		2027-06-20	2028-04-03
CON1290	U20 Rainwater Collecting Pond 1	2027-06-20	2027-10-19
CON1300	U20 Rainwater Collecting Pond 2	2027-12-15	2028-04-03
U27 Truck Scale		2028-03-11	2028-04-24
CON1310	Civil Work and Steel Structure	2028-03-11	2028-04-24
U3201 Potroom Trestle and Ramp		2027-06-04	2028-07-15
CON1320	Potroom Trestle and Ramp 1-1	2027-06-04	2027-07-19
CON1330	Potroom Trestle and Ramp 1-2	2027-10-10	2027-11-24
CON1340	Potroom Trestle and Ramp 1-3	2028-03-02	2028-04-14
CON1350	Potroom Trestle and Ramp 1-4	2028-05-31	2028-07-15
S00 Aluminum Reduction Plant Civil Work Package (8) and (9)		2027-03-15	2029-07-19
CON1360	BOQ Preparation	2027-03-15	2027-04-09
CON1370	Bidding	2027-04-09	2027-05-09
CON1380	Contractor Evaluation	2027-05-09	2027-06-03
CON1390	Employer Evaluation and Award	2027-06-03	2027-07-03
CON1400	Advance Payment	2027-07-03	2027-08-02
CON1410	Civil Subcontractor Mobilize on Site	2027-08-02	2027-12-05
Civil Construction		2027-12-05	2029-07-19
CON1420	Construction Preparation	2027-12-05	2028-01-04
S0102 Potroom		2028-01-04	2029-07-19
Civil Work and Steel Structure		2028-01-04	2029-07-19
CON1430	Potroom Foundation	2028-01-04*	2028-11-03
CON1440	Steel Structure/Component Assembling	2028-02-04	2029-01-03
CON1450	Steel Structure Erection	2028-02-09*	2029-01-08
CON1460	Concrete Platform	2028-03-11	2029-03-19
CON1470	Cladding of Roof and Wall, and Decoration	2028-04-14	2029-04-13
CON1480	Foundation of Pot and Busbar	2028-04-14	2029-04-13
CON1490	Concrete Floor	2028-06-14	2029-05-14
CON1500	Crane Rail Installation	2028-06-14	2029-03-16
CON1510	Water and Electricity Facilities Installation	2028-11-14	2029-06-13
CON1520	Completion of Outdoor Civil Work	2029-04-04	2029-07-19
S0202 Potline Gas Treatment Center		2028-01-20	2029-04-24
S020201 GTC		2028-01-20	2028-11-18
Civil Work		2028-01-20	2028-11-18
CON1530	Construction Preparation	2028-01-20	2028-02-18
CON1540	Plant and Duct Bracket Foundation	2028-02-20	2028-04-03
CON1550	Steel Structure/Component Assembling	2028-03-20	2028-05-04
CON1560	Erection of Steel Column, Beam, and Roof Truss	2028-03-25	2028-05-09
CON1570	Foundation of Chimney ,Fan, Desulfurization system	2028-02-20	2028-04-18
CON1580	Distribution Room and Cable Trench	2028-04-04	2028-05-19
CON1590	Completion of Outdoor Civil Work	2028-10-20	2028-11-18
S020202 GTC		2028-05-10	2029-01-24
Civil Work		2028-05-10	2029-01-24
CON1600	Plant and Duct Bracket Foundation	2028-05-10	2028-07-24
CON1610	Steel Structure/Component Assembling	2028-06-09	2028-07-29
CON1620	Erection of Steel Column, Beam, and Roof Truss	2028-06-14	2028-08-13
CON1630	Foundation of Chimney ,Fan, Desulfurization system	2028-05-10	2028-07-24
CON1640	Distribution Room and Cable Trench	2028-07-25	2028-09-24
CON1650	Completion of Outdoor Civil Work	2028-12-25	2029-01-24
S020203 GTC		2028-07-25	2029-04-24
Civil Work		2028-07-25	2029-04-24
CON1660	Plant and Duct Bracket Foundation	2028-07-25	2028-10-09
CON1670	Steel Structure/Component Assembling	2028-08-25	2028-11-08
CON1680	Erection of Steel Column, Beam, and Roof Truss	2028-08-30	2028-11-13
CON1690	Foundation of Chimney ,Fan, Desulfurization system	2028-07-25	2028-10-29
CON1700	Distribution Room and Cable Trench	2028-10-10	2028-12-09
CON1710	Completion of Outdoor Civil Work	2029-03-30	2029-04-24
S0402 Alumina Conveying system and Daly Silo		2028-01-20	2029-04-13
CON1720	Construction Preparation	2028-01-20	2028-02-19
Foundation and Structure		2028-02-20	2028-11-29
CON1730	Daly Silo 2-1	2028-02-20	2028-04-03
CON1740	Daly Silo 2-2	2028-04-09*	2028-05-24
CON1750	Daly Silo 2-3	2028-10-10	2028-11-29
Chute Steel Structure along Potrrom		2028-03-01	2029-04-13
CON1760	steel structure to Alumina Silo	2028-03-01	2028-05-24
CON1770	steel structure 2-1	2028-05-05	2028-07-04
CON1780	steel structure 2-2	2028-07-30	2028-09-29
CON1790	steel structure 3-3	2029-01-30	2029-04-13
S0602 Super Dense Phase Conveying System		2028-03-25	2029-04-13
Civil Work and Steel Structure		2028-03-25	2029-04-13
Foundation and Structure of Reacted Alumina Silo		2028-03-25	2028-09-24
CON1800	Reacted Alumina Silo 1-1	2028-03-25	2028-05-09

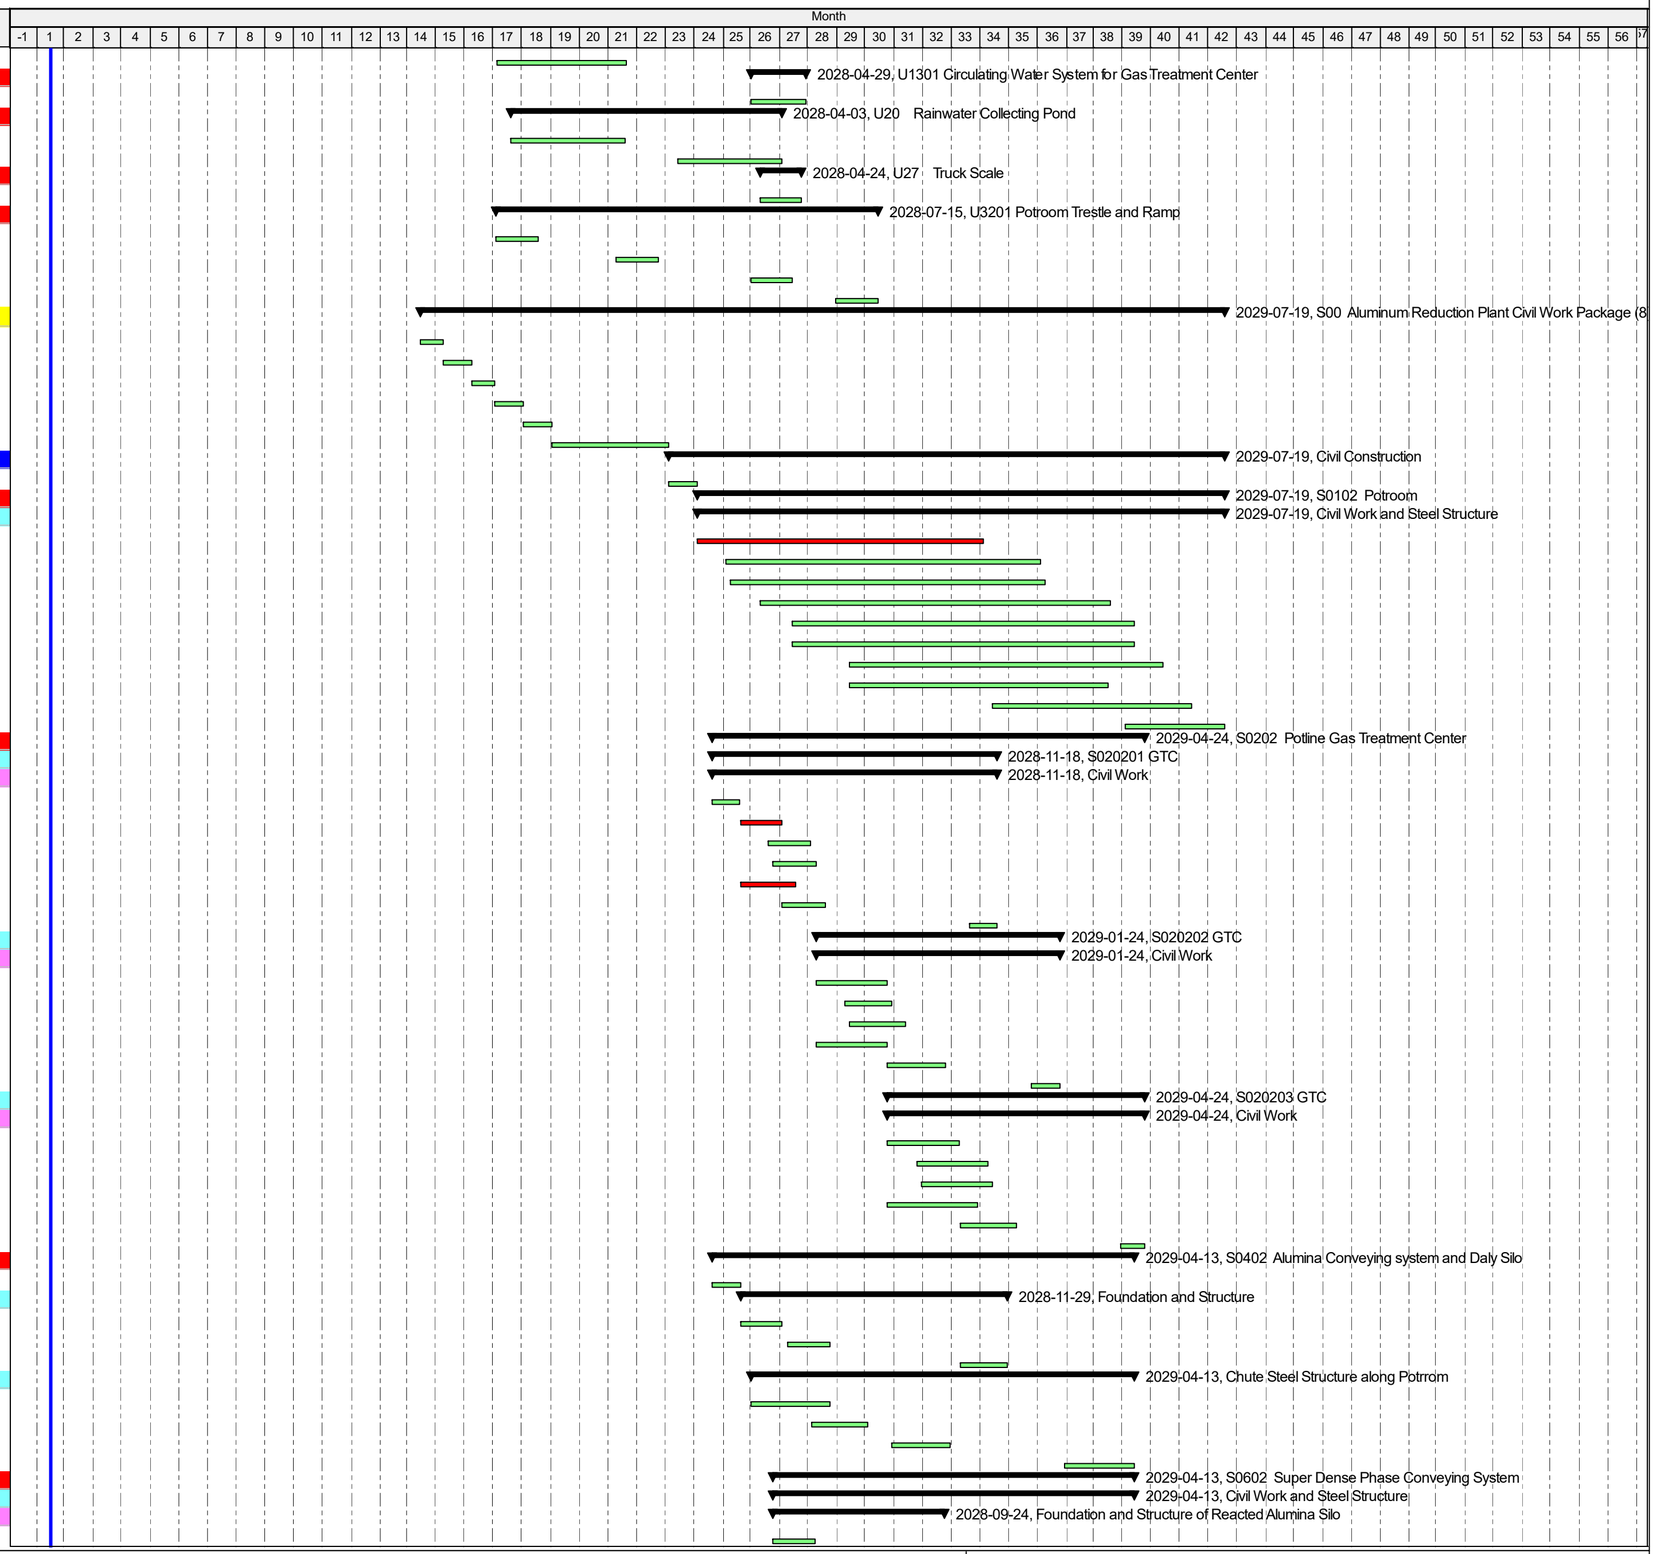

Remaining Level of Effort | Actual Work | Critical Remaining Work | summary
Actual Level of Effort | Remaining Work | Milestone

Project Schedule(Level 3)

Activity ID	Activity Name	Start	Finish
CON1810	Reacted Alumina Silo 1-2	2028-05-25	2028-07-19
CON1820	Reacted Alumina Silo 1-3	2028-07-25	2028-09-24
Platform for Chute		2028-07-15	2029-04-13
CON1830	Platform for Chute 1-1	2028-07-15	2028-09-13
CON1840	Platform for Chute 1-2	2028-11-03	2028-12-19
CON1850	Platform for Chute 1-3	2029-03-02	2029-04-13
S0702 Anode Covering Material Storage & Conveying System		2028-02-04	2029-02-24
Civil Work and Steel Structure		2028-02-04	2029-02-24
CON1860	Foundation 1 & 2	2028-02-04	2028-03-05
CON1870	Foundation 3 & 4	2028-03-25	2028-04-24
CON1880	Foundation 5 & 6	2028-08-14	2028-09-24
CON1890	Foundation 7 & 8	2028-10-10	2028-11-08
CON1900	Installation of Steel Frame and Platform 1,2,3 & 4	2028-04-04	2028-05-29
CON1910	Installation of Steel Frame and Platform 5 & 6	2028-09-25	2028-11-08
CON1920	Installation of Steel Frame and Platform 7 & 8	2029-01-20	2029-02-24
U1302 Circulating Water System for Gas Treatment Center		2029-01-09	2029-03-11
CON1930	Civil Work and Steel Structure	2029-01-09	2029-03-11
U3202 Potroom Trestle and Ramp		2028-04-14	2029-06-13
CON1940	Potroom Trestle and Ramp 2-1	2028-04-14	2028-05-29
CON1950	Potroom Trestle and Ramp 2-2	2028-09-09	2028-10-24
CON1960	Potroom Trestle and Ramp 2-3	2029-01-14	2029-03-01
CON1970	Potroom Trestle and Ramp 2-4	2029-04-30	2029-06-13
S00 Aluminum Reduction Plant (Potroom, SDPC, ACMS) Installation Package (d) and (e)		2026-07-26	2030-02-11
CON1980	Installation Subcontractors Selection and Award	2026-07-26	2026-10-24
CON1990	Advance Payment	2026-10-24	2026-12-08
CON2000	Installation Subcontractor Mobilize on Site	2026-12-08	2027-05-07
Mechanical and E&I Installation		2027-07-15	2030-02-11
S0101 Potroom		2027-10-05	2029-03-31
CON2010	Installation Temporary Overhead Crane	2027-10-05	2028-02-03
Installation		2027-10-20	2029-03-31
CON2020	Busbar Fixure Fabrication	2027-10-20	2027-11-09
CON2030	Busbar Pre-assembling in Workshop	2027-11-09	2027-11-24
CON2040	Busbar	2027-11-25	2028-08-24
CON2050	Pot shell	2028-01-09	2028-09-24
CON2060	Pot Lining	2028-02-09	2028-11-08
CON2070	Superstructure	2028-03-11	2028-12-09
CON2080	PTM	2028-02-13	2028-11-13
CON2090	PTM Test	2028-04-13	2029-01-13
CON2100	Pot Control System	2028-05-10	2028-12-14
CON2110	No Load Interlocking Test	2028-08-09	2029-03-15
CON2120	Issue Phase 1A MC Certificate	2029-03-31	2029-03-31
S0102 Potroom		2028-08-14	2030-02-11
CON2130	Installation Temporary Overhead Crane	2028-08-14	2028-12-14
Installation		2028-10-25	2030-02-11
CON2140	Busbar	2028-10-25	2029-07-24
CON2150	Pot shell	2028-12-10	2029-08-24
CON2160	Pot Lining	2029-01-09	2029-10-09
CON2170	Superstructure	2029-02-09	2029-11-08
CON2180	PTM	2028-12-25	2029-09-24
CON2190	Pot Control System	2029-04-09	2029-11-13
CON2200	No Load Interlocking Test	2029-06-25	2030-02-05
CON2210	Issue Phase 1B MC Certificate	2030-02-11	2030-02-11
S0601 Super Dense Phase Conveying System (without reacted silo)		2027-11-14	2028-12-14
Installation		2027-11-14	2028-12-14
Main Chute and Air Pipe		2027-11-14	2028-07-19
CON2220	Main Chute and Air Pipe 1-1	2027-11-14	2027-12-29
CON2230	Main Chute and Air Pipe 1-2	2028-03-06	2028-04-18
CON2240	Main Chute and Air Pipe 1-3	2028-06-04	2028-07-19
Fan, Electrical Equipment and Instrumentation		2027-11-14	2028-08-03
CON2250	MEI 1-1	2027-11-14	2028-01-13
CON2260	MEI 1-2	2028-03-06	2028-05-04
CON2270	MEI 1-2	2028-06-04	2028-08-03
Installation		2028-02-14	2028-12-14
CON2280	Chute on Superstructure	2028-05-15	2028-12-14
CON2290	No Load Test	2028-02-14	2028-11-14
S0602 Super Dense Phase Conveying System (without reacted silo)		2028-09-14	2029-11-13
Installation		2028-09-14	2029-11-13
Main Chute and Air Pipe		2028-09-14	2029-05-29
CON2300	Main Chute and Air Pipe 2-1	2028-09-14	2028-11-18
CON2310	Main Chute and Air Pipe 2-2	2028-12-20	2029-02-03
CON2320	Main Chute and Air Pipe 2-3	2029-04-14	2029-05-29
Fan, Electrical Equipment and Instrumentation		2028-09-14	2029-06-13
CON2330	MEI 1-1	2028-09-14	2028-11-13
CON2340	MEI 1-2	2028-12-20	2029-02-18
CON2350	MEI 1-3	2029-04-14	2029-06-13

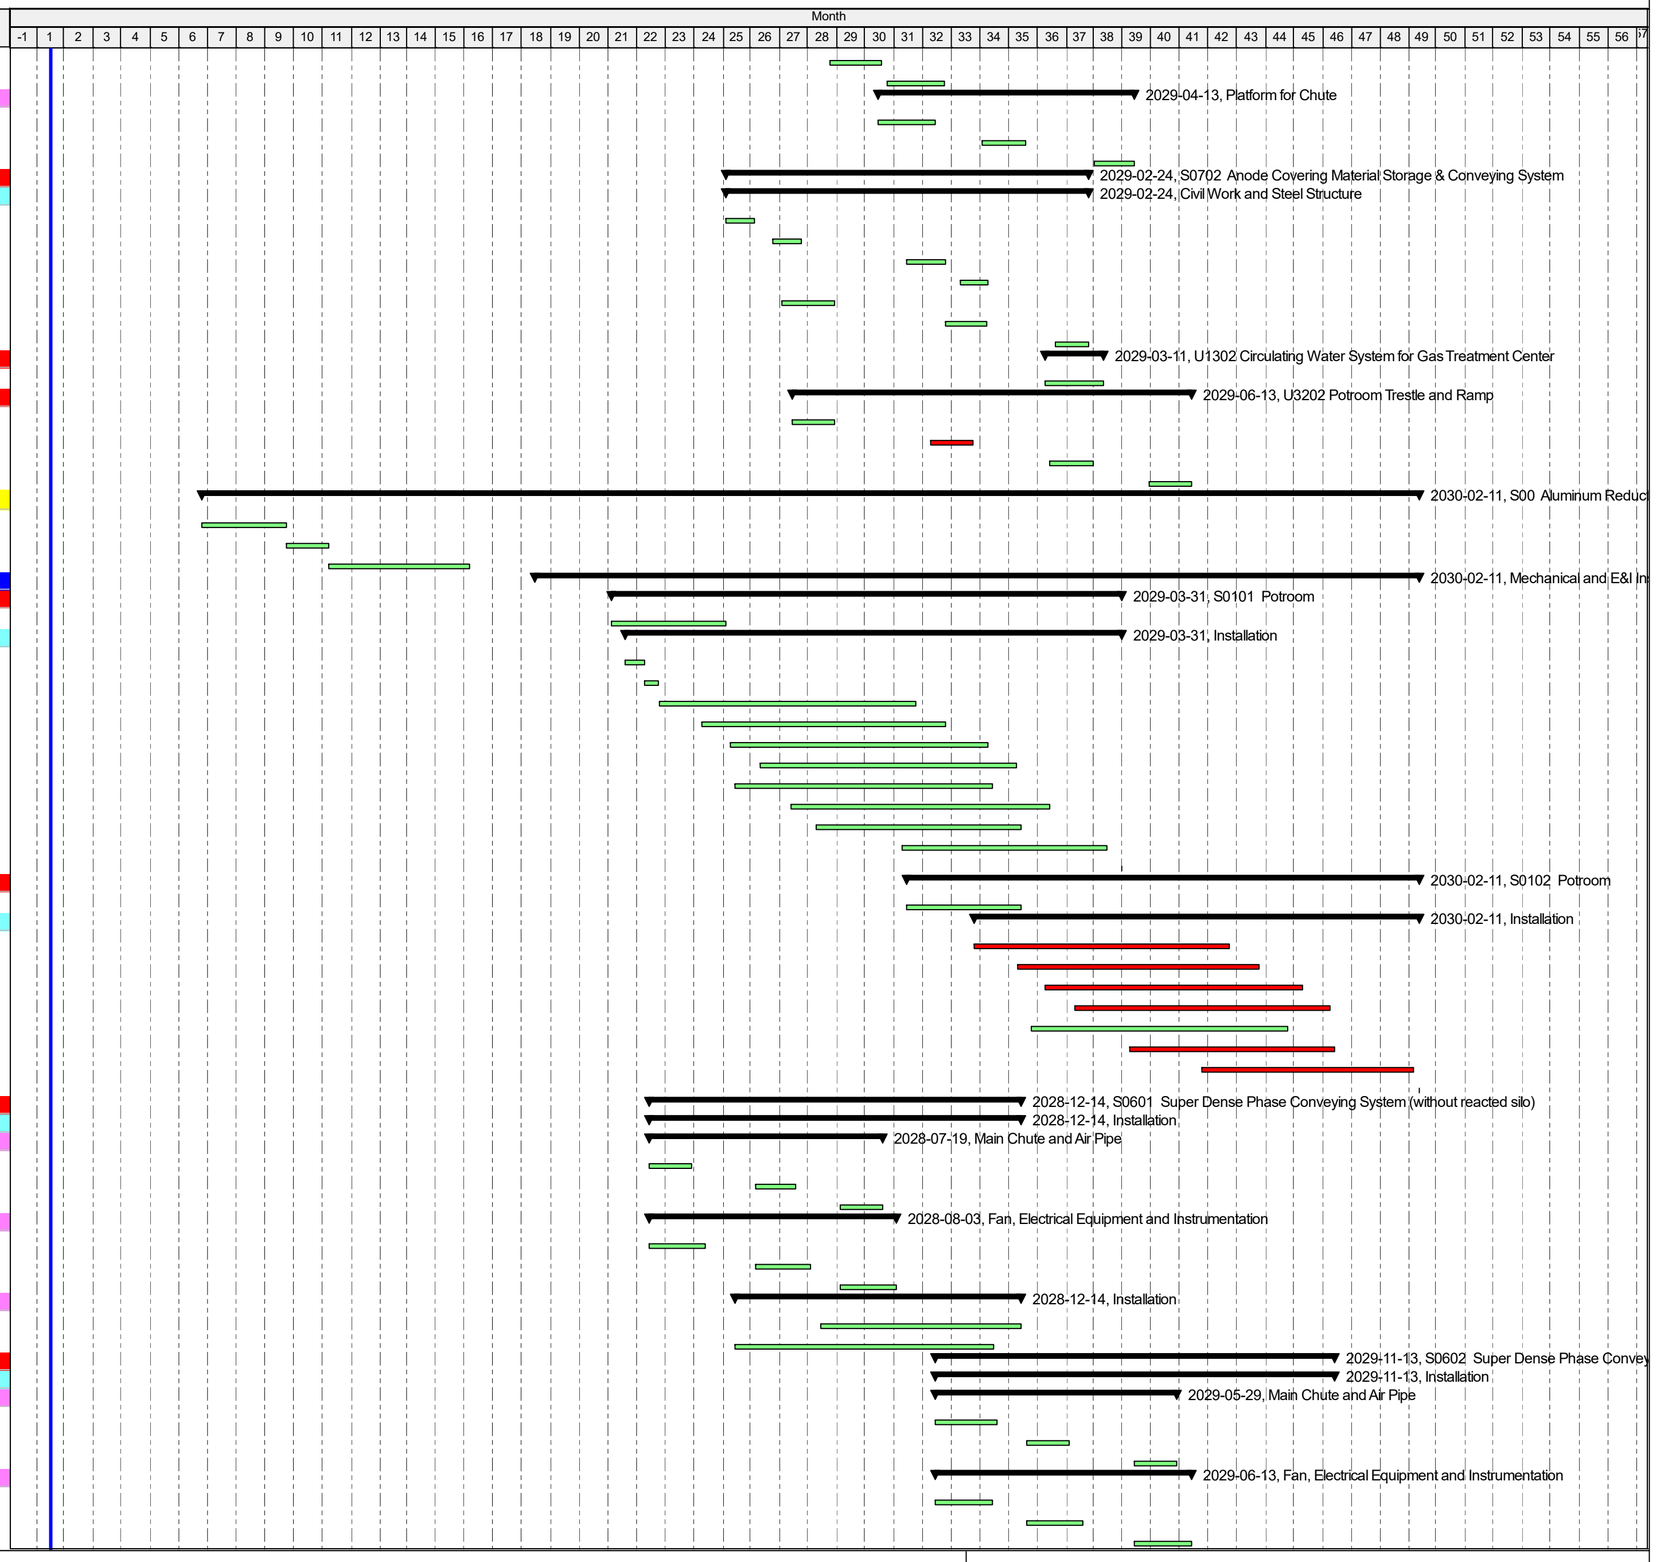

Remaining Level of Effort | Actual Work | Critical Remaining Work | summary
Actual Level of Effort | Remaining Work | Milestone

Project Schedule(Level 3)

Activity ID	Activity Name	Start	Finish
	Installation	2028-12-15	2029-11-13
CON2360	Chute on Superstructure	2029-04-20	2029-11-13
CON2370	No Load Test	2028-12-15	2029-10-14
	S0701 Anode Covering Material Storage & Conveying System	2027-07-15	2028-05-30
	Installation	2027-07-15	2028-05-30
CON2380	High Level Silo 1,2,3 & 4	2027-07-15	2027-08-18
CON2390	High Level Silo 5 & 6	2027-12-26	2028-01-09
CON2400	High Level Silo 7 & 8	2028-04-16	2028-04-30
CON2410	Bucket Lifting Equipment 1,2,3 & 4	2027-08-20	2027-10-09
CON2420	Bucket Lifting Equipment 5 & 6	2028-01-10	2028-03-01
CON2430	Bucket Lifting Equipment 7 & 8	2028-05-01	2028-05-30
	S0702 Anode Covering Material Storage & Conveying System	2028-05-30	2029-04-29
	Installation	2028-05-30	2029-04-29
CON2440	High Level Silo 1,2,3 & 4	2028-05-30	2028-07-04
CON2450	High Level Silo 5 & 6	2028-11-09	2028-11-24
CON2460	High Level Silo 7 & 8	2029-02-25	2029-03-16
CON2470	Bucket Lifting Equipment 1,2,3 & 4	2028-07-05	2028-09-08
CON2480	Bucket Lifting Equipment 5 & 6	2028-11-25	2029-01-13
CON2490	Bucket Lifting Equipment 7 & 8	2029-03-17	2029-04-29
	S1203 Aluminium Ingot Yard	2027-10-21	2027-11-10
CON2500	Installation (Cabling and Lighting)	2027-10-21	2027-11-10
	U20 Rainwater Collecting Pond (pump, etc.)	2027-10-20	2028-04-23
CON2510	Installation Pond 1 (Pump and Cabling)	2027-10-20	2027-11-08
CON2520	Installation Pond 2 (Pump and Cabling)	2028-04-04	2028-04-23
	U27 Truck Scale	2028-04-25	2028-05-29
CON2530	Installation and Test of Equipment	2028-04-25	2028-05-29
	S00 Aluminum Reduction Plant (Alumina Conveying System) Installation Package (f)	2026-07-26	2029-08-13
CON2540	Installation Subcontractors Selection and Award	2026-07-26	2026-10-24
CON2550	Advance Payment	2026-10-24	2026-12-08
CON2560	Installation Subcontractor Mobilize on Site	2026-12-08	2027-05-07
	Mechanical and E&I Installation	2027-06-20	2029-08-13
	E01 Raw Material Conveying system	2028-05-25	2028-10-24
CON2570	Equipment Installation and Test	2028-05-25*	2028-09-24
CON2580	No Load Test	2028-09-25	2028-10-24
	S03 Alumina Storage	2028-02-09	2028-10-24
CON2590	Silo Erection	2028-02-09	2028-07-24
CON2600	Installation and Test of Mechanical/Electrical Equipment and Instrumentatic	2028-06-25	2028-09-24
CON2610	No Load Test	2028-09-25	2028-10-24
	S0401 Alumina Conveying System and Daly Silo	2027-07-30	2028-10-14
	Steel Silo Erection	2027-07-30	2028-02-20
CON2620	Daly Silo 1-1	2027-07-30	2027-10-09
CON2630	Daly Silo 1-2	2027-11-16	2028-01-14
CON2640	Daly Silo 1-3	2027-12-21	2028-02-20
	Installation and Test of Mechanical/Electrical Equipment and Instrumentation System	2028-06-04	2028-08-13
CON2650	chute and Equipment 1-1	2028-06-25	2028-07-24
CON2660	chute and Equipment 1-2	2028-07-15	2028-08-13
CON2670	chute and Equipment 1-3	2028-06-04	2028-07-19
	No Load Test	2028-08-25	2028-10-14
CON2680	No Load Test	2028-08-25	2028-10-14
	S0402 Alumina Conveying System and Daly Silo	2028-04-04	2029-08-13
	Steel Silo Erection	2028-04-04	2029-01-29
1230	Daly Silo 2-1	2028-04-04	2028-06-03
1231	Daly Silo 2-2	2028-05-25	2028-08-18
1232	Daly Silo 2-3	2028-11-30	2029-01-29
	Installation and Test of Mechanical/Electrical Equipment and Instrumentation System	2028-05-25	2029-06-13
1234	Chute and Equipment to Alumina Silo	2028-05-25	2028-08-24
1235	chute and Equipment 2-1	2028-07-05	2028-08-03
1236	chute and Equipment 2-2	2028-09-30	2028-10-30
1237	chute and Equipment 2-3	2029-04-14	2029-06-13
	No Load Test	2029-06-14	2029-08-13
1238	No Load Test	2029-06-14	2029-08-13
	S0601 Super Dense Phase Conveying System (Reacted silo installation)	2027-06-20	2028-01-25
	Installation	2027-06-20	2028-01-25
	Reacted Alumina Silo	2027-06-20	2028-01-25
CON2690	Reacted Alumina Silo 1-1	2027-06-20	2027-08-18
CON2700	Reacted Alumina Silo 1-2	2027-10-06	2027-12-05
CON2710	Reacted Alumina Silo 1-3	2027-11-26	2028-01-25
	S0602 Super Dense Phase Conveying System (Reacted silo installation)	2028-05-10	2028-11-29
	Installation	2028-05-10	2028-11-29
	Reacted Alumina Silo	2028-05-10	2028-11-29
CON2720	Reacted Alumina Silo 2-1	2028-05-10	2028-07-19
CON2730	Reacted Alumina Silo 2-2	2028-07-20	2028-09-29
CON2740	Reacted Alumina Silo 2-3	2028-09-25	2028-11-29
	GTC, FTC, and CTC Installation Package (g)	2026-11-21	2029-07-19
CON2750	Mechanical Subcontractor Mobilize on Site	2026-11-21	2027-04-20

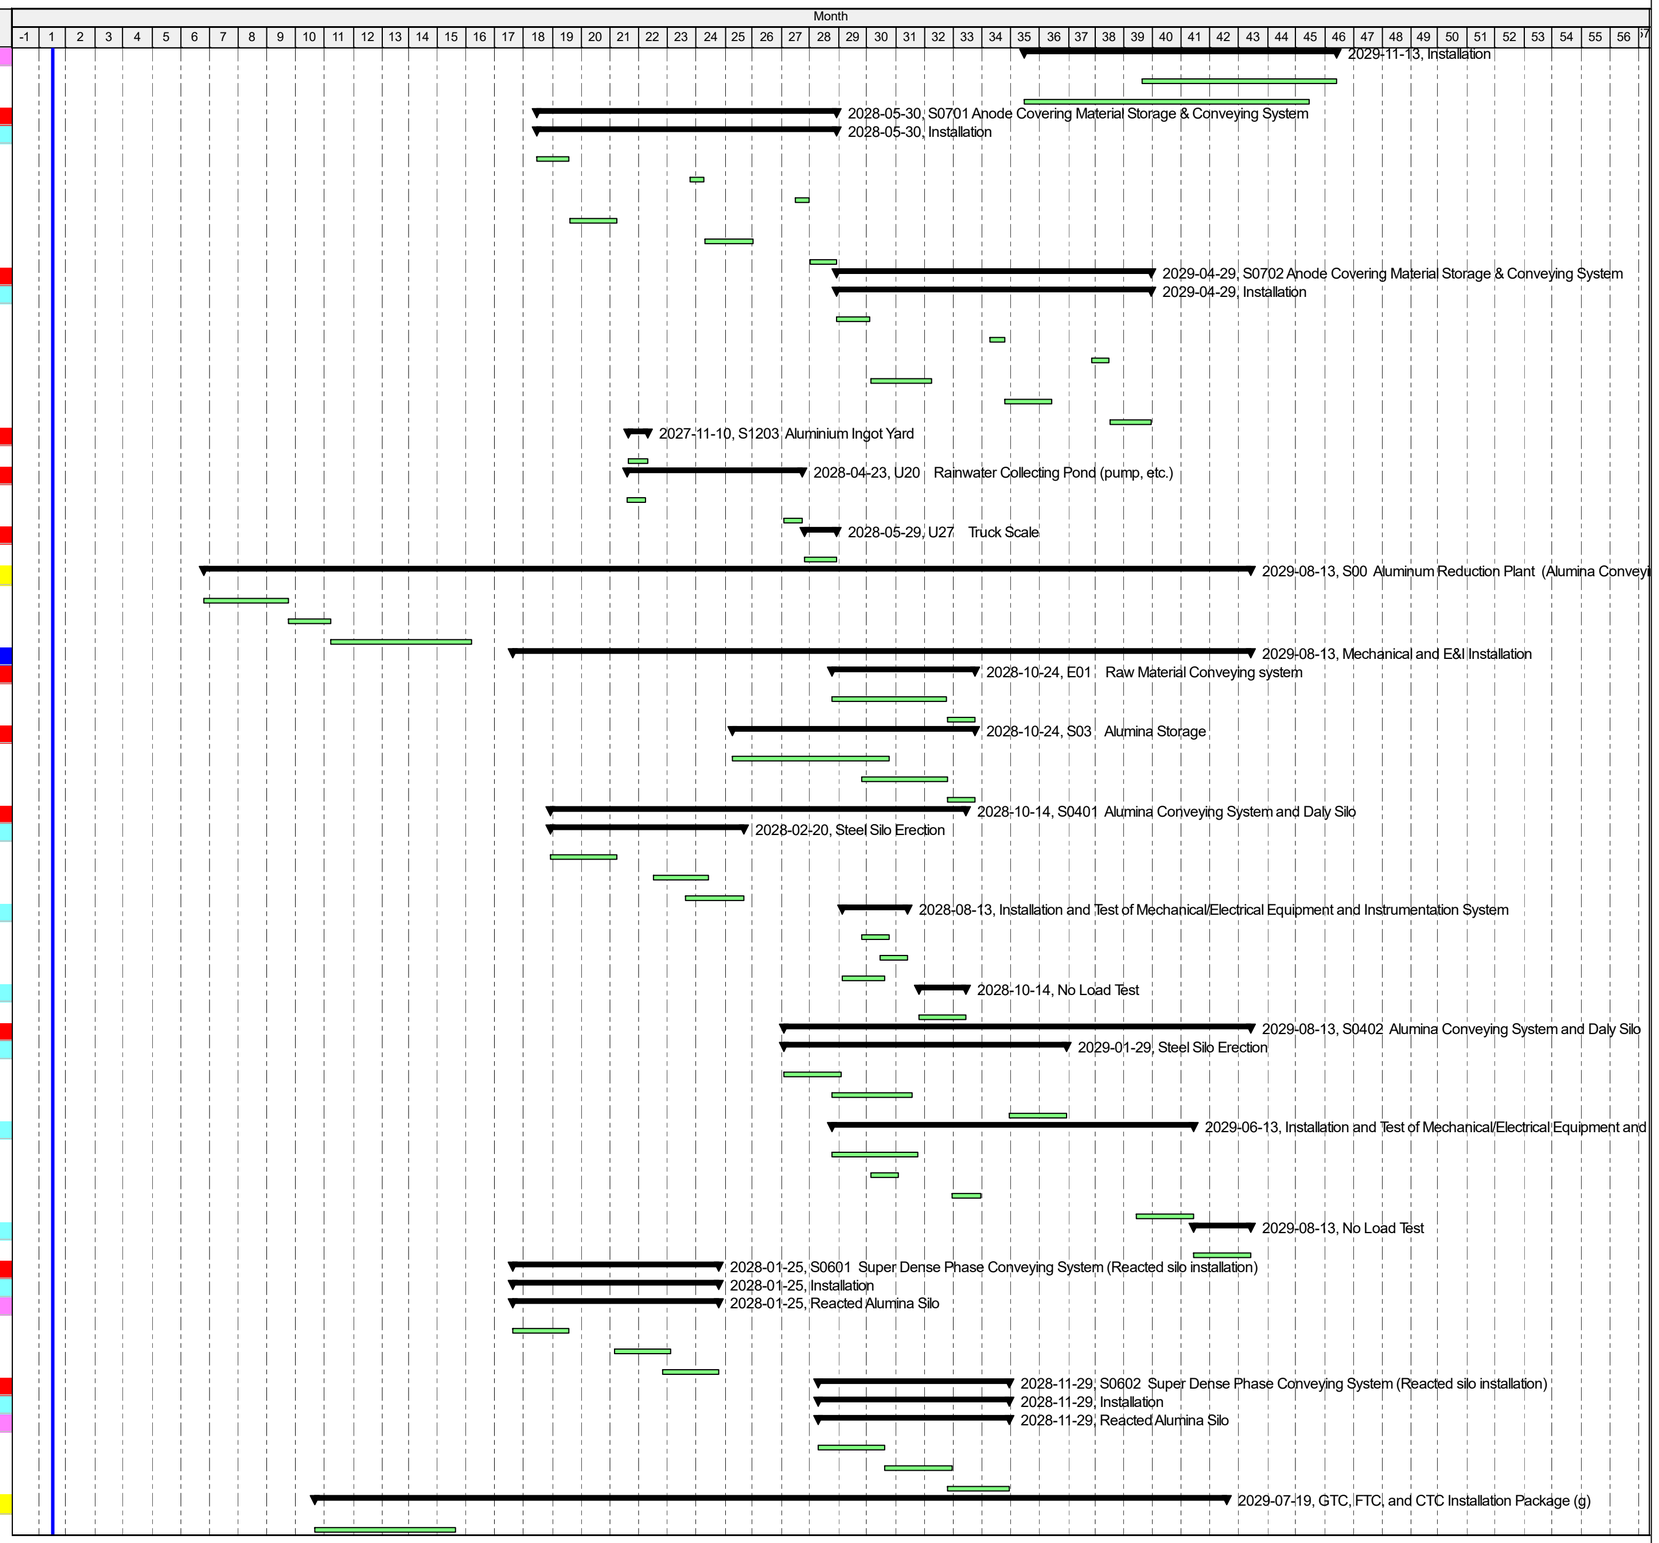

Remaining Level of Effort | Actual Work | Critical Remaining Work | summary
Actual Level of Effort | Remaining Work | Milestone

Project Schedule(Level 3)

Activity ID	Activity Name	Start	Finish
	Mechanical and E&I Installation	2027-05-20	2029-07-19
	S0201 Potline Gas Treatment Center	2027-05-20	2028-07-10
	S020101 Installation	2027-05-20	2028-03-15
CON2760	Chimney	2027-05-20	2027-07-19
CON2770	Installation of Bag Filter	2027-06-20	2027-08-18
CON2780	Fabrication of Duct	2027-08-09	2027-09-08
CON2790	Installation of Duct	2027-08-20	2027-09-18
CON2800	Installation of Desulfurization System	2027-05-20	2027-10-19
CON2810	Installation of Equipment and Pipe	2027-07-20	2027-10-19
CON2820	Installation of Power Distribution System	2027-09-20	2027-12-19
CON2830	No Load Test	2028-01-20	2028-03-15
	S020102 Installation	2027-09-20	2028-05-30
CON2840	Chimney	2028-01-05	2028-03-01
CON2850	Installation of Bag Filter	2027-09-20	2027-12-05
CON2860	Fabrication of Duct	2027-11-26	2027-12-25
CON2870	Installation of Duct	2027-12-06	2028-01-04
CON2880	Installation of Desulfurization System	2027-10-16	2028-01-25
CON2890	Installation of Equipment and Pipe	2027-10-21	2028-02-04
CON2900	Installation of Power Distribution System	2028-01-05	2028-04-04
CON2910	No Load Test	2028-04-05	2028-05-30
	S020103 Installation	2027-11-21	2028-07-10
CON2920	Chimney	2028-03-02	2028-04-30
CON2930	Installation of Bag Filter	2027-11-26	2028-01-25
CON2940	Fabrication of Duct	2028-01-16	2028-02-14
CON2950	Installation of Duct	2028-01-26	2028-02-25
CON2960	Installation of Desulfurization System	2027-11-21	2028-03-01
CON2970	Installation of Equipment and Pipe	2027-12-26	2028-04-04
CON2980	Installation of Power Distribution System	2028-02-16	2028-05-15
CON2990	No Load Test	2028-05-16	2028-07-10
	S0202 Potline Gas Treatment Center	2028-04-20	2029-06-24
	S020201 Installation	2028-04-20	2029-01-18
CON3000	Chimney	2028-04-20	2028-06-18
CON3010	Installation of Bag Filter	2028-05-20	2028-07-19
CON3020	Fabrication of Duct	2028-07-10	2028-08-08
CON3030	Installation of Duct	2028-07-20	2028-08-18
CON3040	Installation of Desulfurization System	2028-04-20	2028-07-29
CON3050	Installation of Equipment and Pipe	2028-05-20	2028-09-18
CON3060	Installation of Power Distribution System	2028-08-20	2028-11-18
CON3070	No Load Test	2028-11-20	2029-01-18
	S020202 Installation	2028-07-15	2029-03-24
CON3080	Chimney	2028-11-14	2029-01-13
CON3090	Installation of Bag Filter	2028-07-15	2028-09-29
CON3100	Fabrication of Duct	2028-09-20	2028-11-03
CON3110	Installation of Duct	2028-09-30	2028-11-13
CON3120	Installation of Desulfurization System	2028-07-25	2028-12-09
CON3130	Installation of Equipment and Pipe	2028-08-30	2028-12-14
CON3140	Installation of Power Distribution System	2028-10-25	2029-01-24
CON3150	No Load Test	2029-01-25	2029-03-24
	S020203 Installation	2028-09-30	2029-06-24
CON3160	Chimney	2029-02-09	2029-04-08
CON3170	Installation of Bag Filter	2028-09-30	2028-11-29
CON3180	Fabrication of Duct	2028-11-20	2028-12-19
CON3190	Installation of Duct	2028-11-30	2028-12-29
CON3200	Installation of Desulfurization System	2028-10-30	2029-02-08
CON3210	Installation of Equipment and Pipe	2028-11-30	2029-03-01
CON3220	Installation of Power Distribution System	2029-01-25	2029-04-24
CON3230	No Load Test	2029-04-25	2029-06-24
	A08 Baking Furnace Fume Treatment Center	2028-02-20	2029-07-19
CON3240	Chimney Erection (Phase 1A)	2028-02-20	2028-04-18
CON3250	Chimney Erection (Phase 1B)	2028-08-14	2028-11-13
CON3260	Installation and Test of Dust Collector, Fume Duct, and Equipment (1A)	2028-03-20	2028-11-03
CON3270	Installation and Test of Dust Collector, Fume Duct, and Equipment (Phase	2028-10-15	2029-06-03
CON3280	No Load Test (1A)	2028-11-04	2028-12-04
CON3290	No Load Test (1B)	2029-06-04	2029-07-19
	A09 Calcination Fume Treatment Center	2028-01-04	2028-10-09
CON3300	Equipment and Duct Installation	2028-01-04	2028-08-08
CON3310	E&I Installation	2028-03-06	2028-09-08
CON3320	No Load Test	2028-08-09	2028-10-09
	U1301 Circulating Water System for Gas Treatment Center	2028-04-30	2028-07-19
CON3330	MEI Installation	2028-04-30	2028-06-29
CON3340	No Load Test	2028-06-30	2028-07-19
	U1302 Circulating Water System for Gas Treatment Center	2029-03-12	2029-05-29
CON3350	MEI Installation	2029-03-12	2029-05-09
CON3360	No Load Test	2029-05-10	2029-05-29

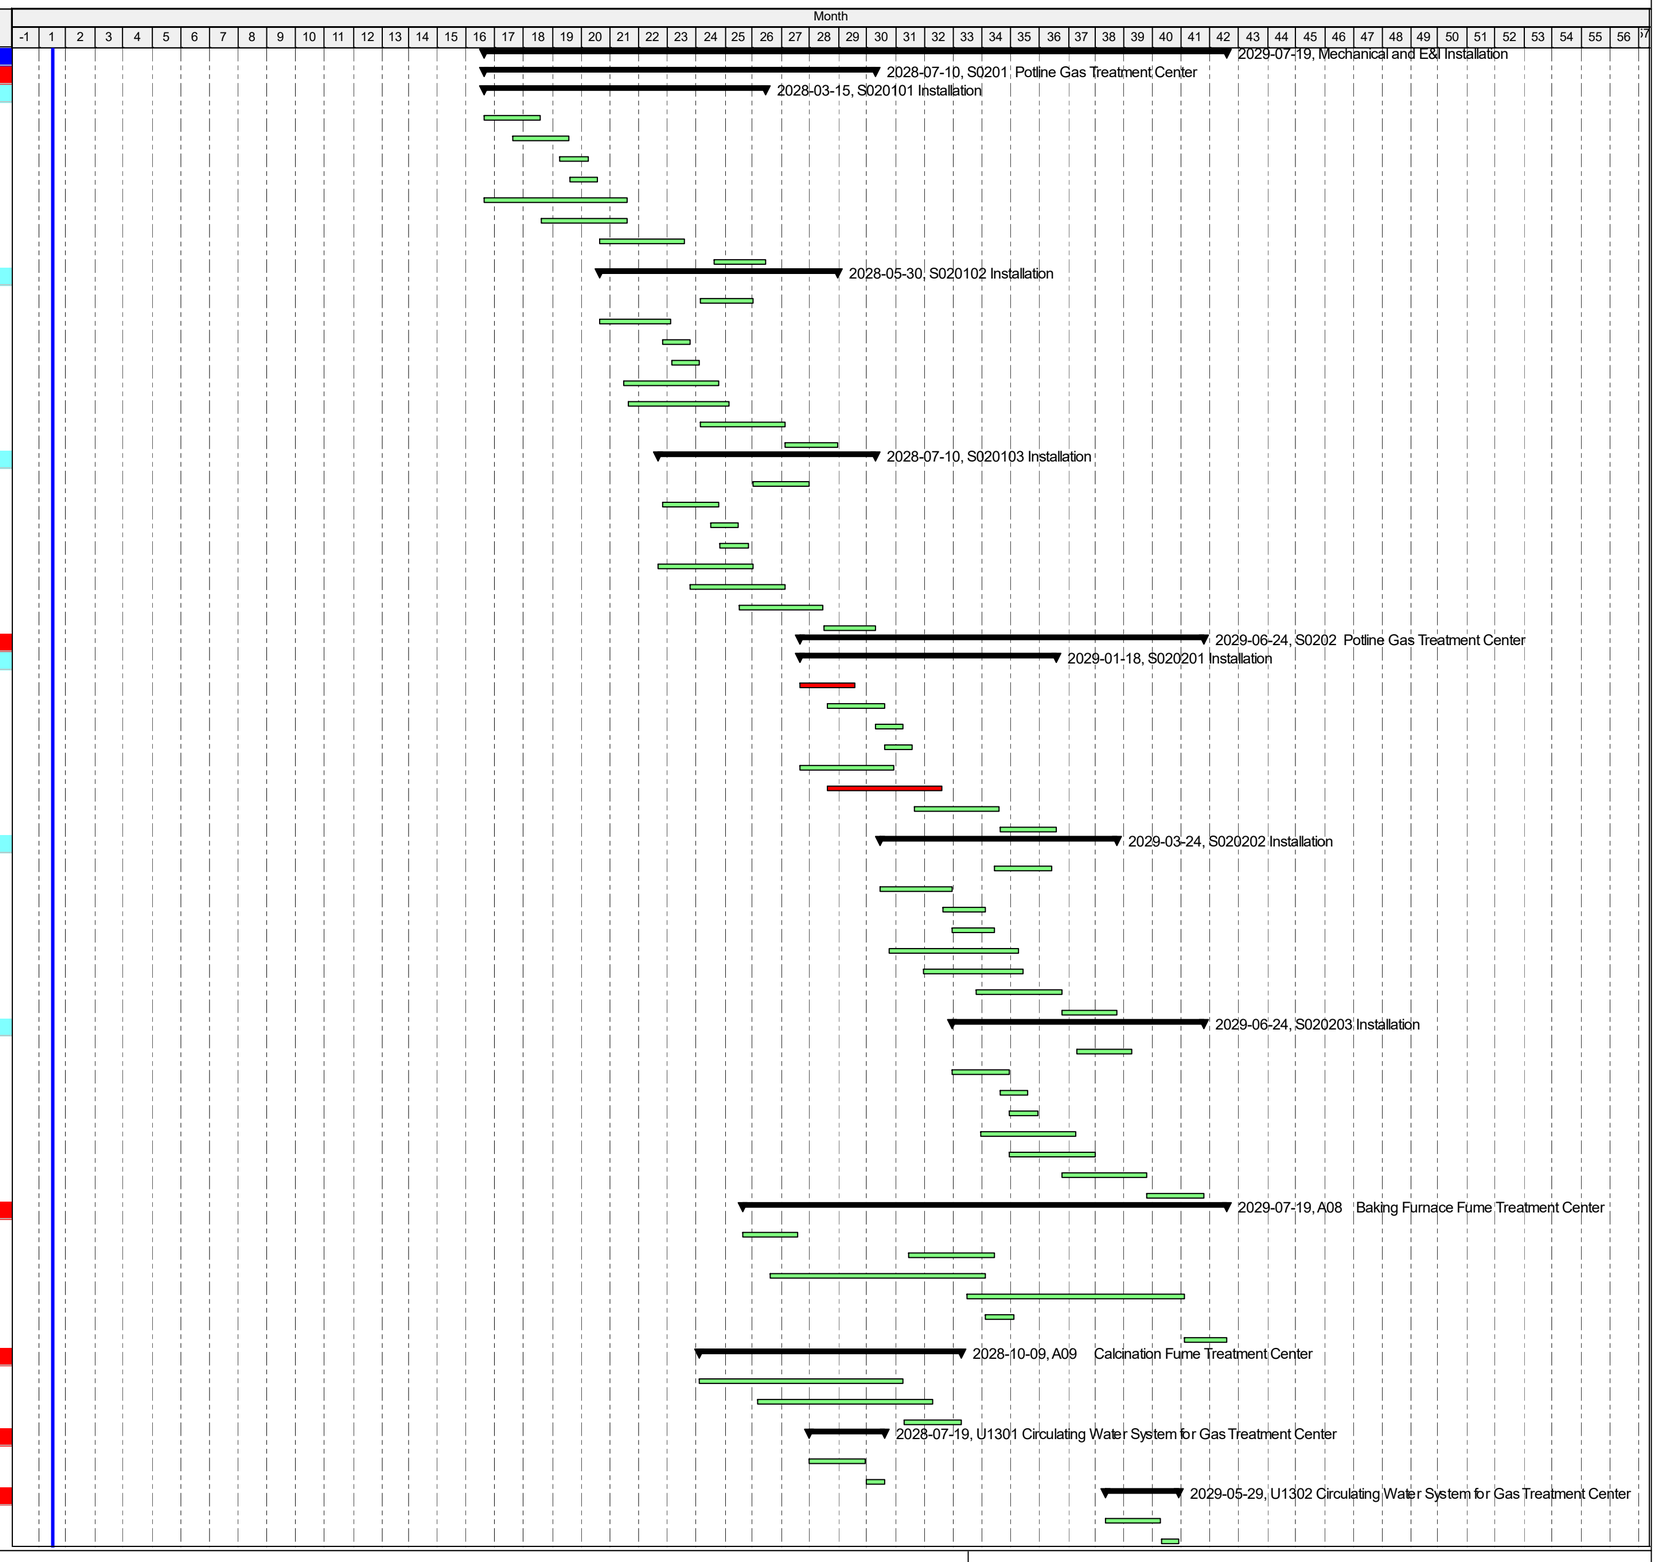

Remaining Level of Effort | Actual Work | Critical Remaining Work | summary
Actual Level of Effort | Remaining Work | Milestone

Project Schedule(Level 3)

Activity ID	Activity Name	Start	Finish
S00	Aluminum Reduction Plant (Cast House) Civil Work Package (10)	2026-05-06	2029-01-03
CON3370	BOQ Preparation	2026-05-06	2026-06-05
Bidding		2026-06-05	2026-07-30
CON3380	Bidding	2026-06-05	2026-06-25
CON3390	Tendering and Bid Clarification Meeting	2026-06-25	2026-07-30
Civil Subcontractors Selection and Award		2026-07-30	2026-11-12
CON3400	Contractor Evaluation	2026-07-30	2026-08-29
CON3410	Employer Evaluation and Award	2026-08-29	2026-09-28
CON3420	Advance Payment	2026-09-28	2026-11-12
Civil Subcontractor Mobilize on Site		2026-11-12	2027-03-17
CON3430	Civil Subcontractor Mobilize on Site	2026-11-12	2027-03-17
Civil Construction		2027-03-17	2029-01-03
S08	Cast House	2027-10-15	2028-12-19
Civil Work and Steel Structure		2027-10-15	2028-12-19
CON3440	Construction Preparation	2027-10-15	2027-11-03
CON3450	Plant and Equipment Foundation	2027-11-04	2028-05-04
CON3460	Steel Structure/Component Assembling	2028-01-20	2028-05-19
CON3470	Steel Structure Erection	2028-02-04	2028-06-18
CON3480	Cladding of Roof and Wall, and Attached Building	2028-03-20	2028-07-19
CON3490	Foundation of Equipment	2028-06-04	2028-09-03
CON3500	Concrete Floor	2028-10-21	2028-12-19
S09	Crucible Cleaning Workshop	2028-01-04	2028-10-29
Civil Work and Steel Structure		2028-01-04	2028-10-29
CON3510	Construction Preparation	2028-01-04	2028-02-03
CON3520	Plant and Equipment Foundation	2028-02-04	2028-03-20
CON3530	Steel Structure/Component Assembling	2028-03-11	2028-04-18
CON3540	Steel Structure Erection	2028-03-20	2028-04-29
CON3550	Cladding of Roof and Wall, and Decoration	2028-04-30	2028-05-29
CON3560	Concrete Floor	2028-09-30	2028-10-29
S10	Dross Treatment Workshop	2028-02-04	2029-01-03
Civil Work and Steel Structure		2028-02-04	2029-01-03
CON3570	Construction Preparation	2028-02-04	2028-03-05
CON3580	Plant and Equipment Foundation	2028-03-06	2028-04-18
CON3590	Steel Structure/Component Assembling	2028-03-25	2028-05-04
CON3600	Steel Structure Erection	2028-04-14	2028-05-24
CON3610	Cladding of Roof and Wall, and Decoration	2028-05-25	2028-06-13
CON3620	Concrete Floor	2028-12-15	2029-01-03
S11	Carbon Deposit Treatment Workshop	2027-05-15	2027-11-03
Civil Work and Steel Structure		2027-05-15	2027-11-03
CON3630	Construction Preparation	2027-05-15	2027-06-13
CON3640	Plant and Equipment Foundation	2027-06-14	2027-07-29
CON3650	Steel Structure/Component Assembling	2027-07-05	2027-08-03
CON3660	Steel Structure Erection	2027-08-04	2027-09-03
CON3670	Cladding of Roof and Wall, and Decoration	2027-09-04	2027-10-04
CON3680	Concrete Floor	2027-10-05	2027-11-03
S1201&1202	Aluminium Ingot Yard	2027-04-14	2027-06-28
CON3690	Aluminium Ingot Yard	2027-04-14	2027-06-28
S13	SPL Temporary Storage	2027-03-25	2027-08-13
Civil Work and Steel Structure		2027-03-25	2027-08-13
CON3700	Construction Preparation	2027-03-25*	2027-04-13
CON3710	Plant and Equipment Foundation	2027-04-14	2027-05-29
CON3720	Steel Structure/Component Assembling	2027-04-29	2027-06-13
CON3730	Steel Structure Erection	2027-05-15	2027-06-29
CON3740	Cladding of Roof and Wall, and Decoration	2027-05-30	2027-07-14
CON3750	Concrete Floor	2027-07-15	2027-08-13
A1202	Stem and Stub Repair Workshop	2027-11-14	2028-03-15
CON3760	Civil Work and Steel Structure	2027-11-14	2028-03-15
U0704	Diesel Generator Room	2027-09-25	2027-11-24
CON3770	Civil Work and Steel Structure	2027-09-25	2027-11-24
U09	Compressor Air Station	2027-09-16	2027-12-20
CON3780	Civil Work and Steel Structure	2027-09-16	2027-12-20
U11	Circulating Water System for Cast House	2028-03-01	2028-07-29
CON3790	Civil Work and Steel Structure	2028-03-01	2028-07-29
U12	Circulating Water System for Compressor Air Station	2027-12-21	2028-03-30
CON3800	Civil Work and Steel Structure	2027-12-21	2028-03-30
U23	Pot Maintenance Shop	2027-03-17	2027-11-18
Civil Work and Steel Structure		2027-03-17	2027-11-18
CON3810	Construction Preparation	2027-03-17	2027-04-13
CON3820	Plant and Equipment Foundation	2027-04-14	2027-07-24
CON3830	Steel Structure/Component Assembling	2027-05-24	2027-08-18
CON3840	Steel Structure Erection	2027-06-03	2027-08-29
CON3850	Cladding of Roof and Wall, and Decoration	2027-07-04	2027-09-18
CON3860	Concrete Floor	2027-09-19	2027-11-18
U33	Natural Gas Press Regulating Station	2028-04-20	2028-06-03
CON3870	Civil Work	2028-04-20	2028-06-03

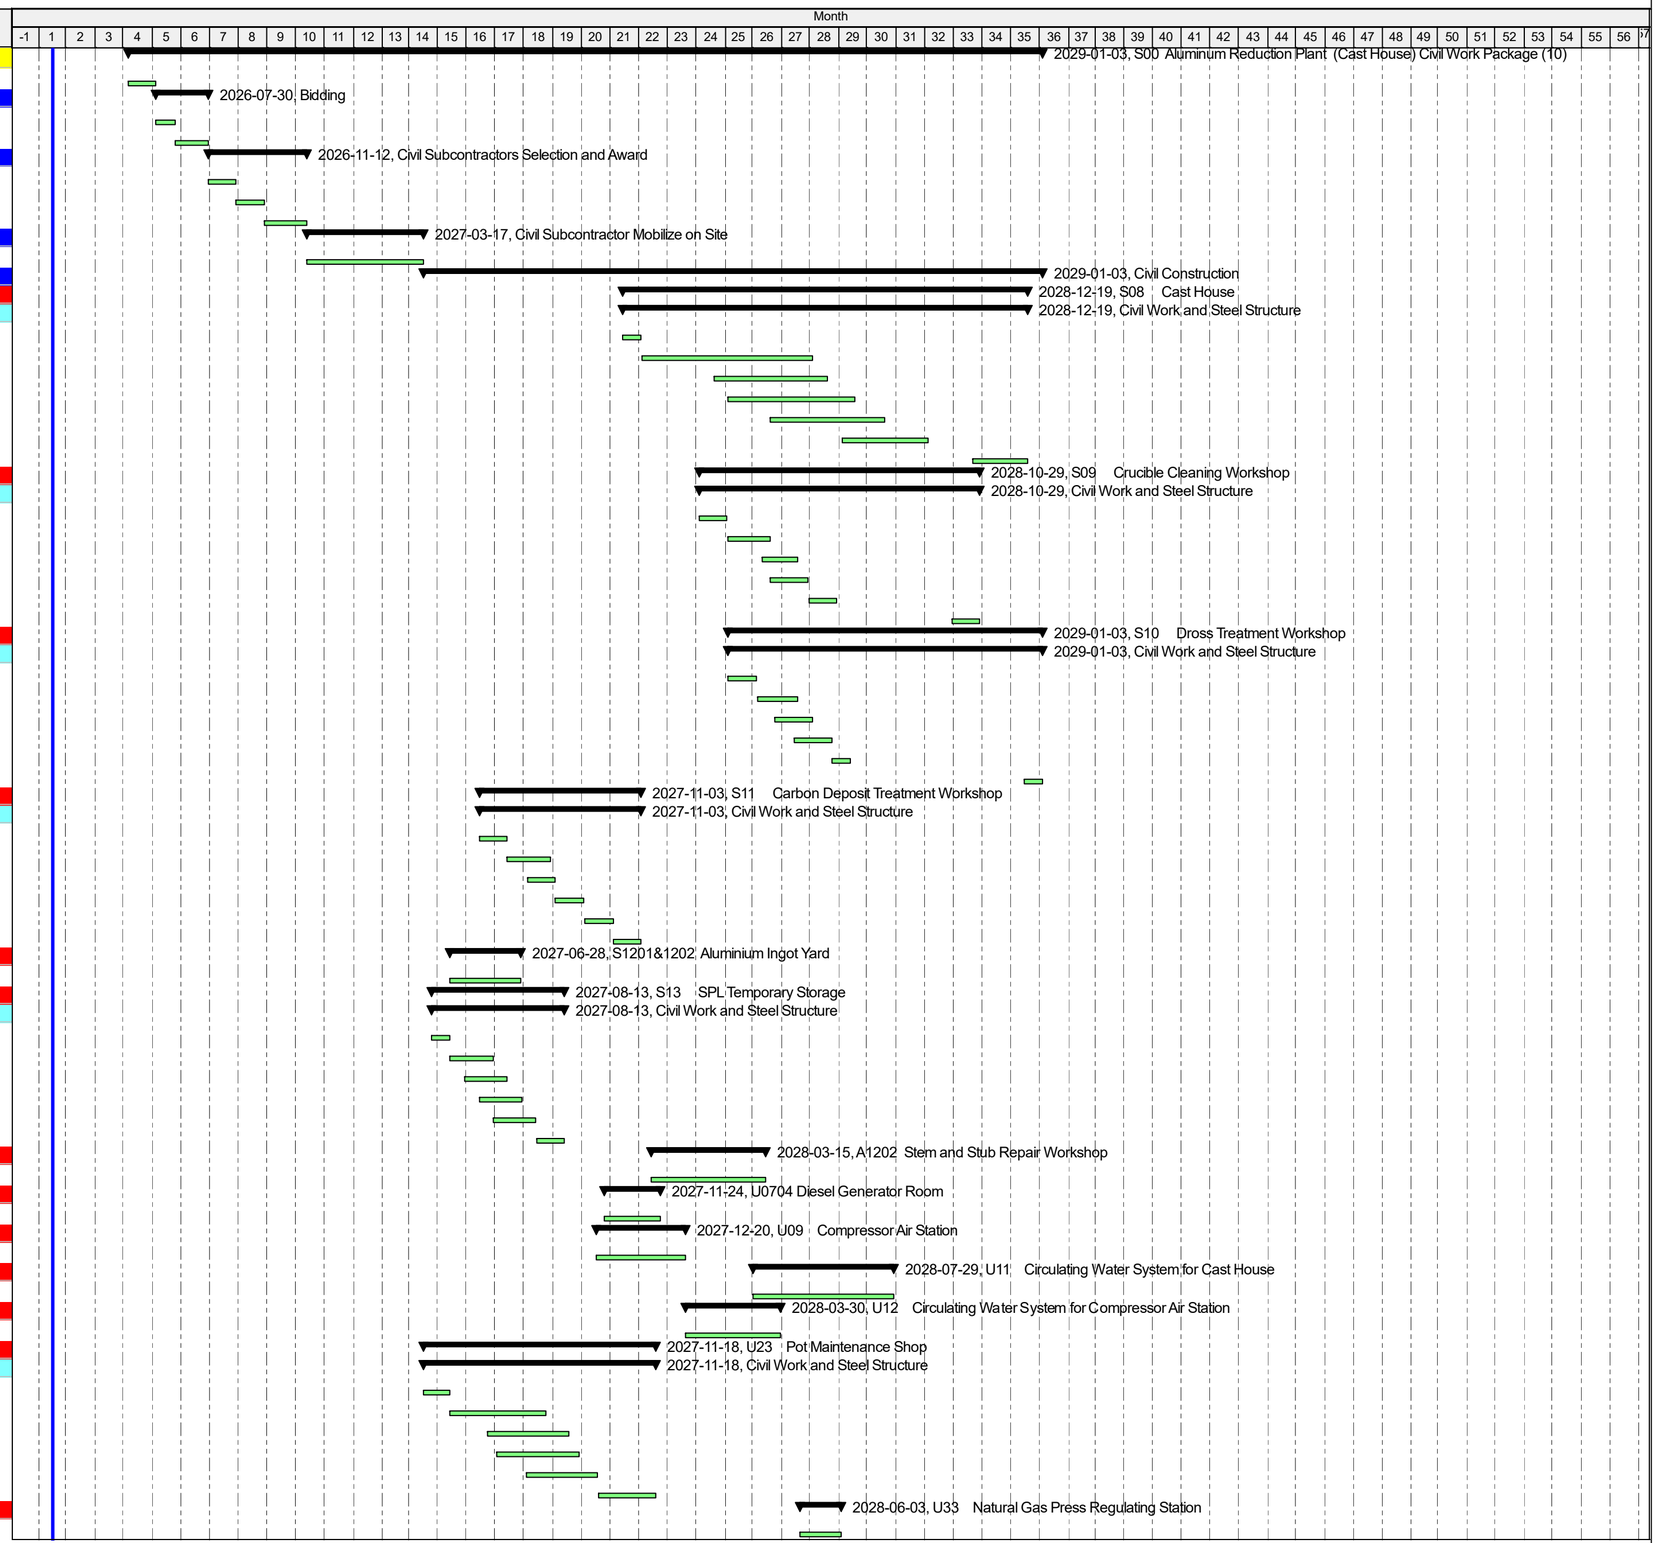

Remaining Level of Effort | Actual Work | Critical Remaining Work | summary
Actual Level of Effort | Remaining Work | Milestone

Project Schedule(Level 3)

Activity ID	Activity Name	Start	Finish
M01	Comprehensive Office Building	2027-12-05	2028-04-29
CON3880	Civil Work and Steel Structure	2027-12-05	2028-04-29
M02	Reduction Area Comprehensive Building	2027-11-04	2028-03-29
CON3890	Civil Work and Steel Structure	2027-11-04	2028-03-29
M03	Dining Hall	2028-02-14	2028-05-14
CON3900	Civil Work and Steel Structure	2028-02-14	2028-05-14
M04	Shower Room	2028-03-16	2028-05-14
CON3910	Civil Work and Steel Structure	2028-03-16	2028-05-14
S00	Aluminum Reduction Plant (Cast House) Installation Package (h)	2027-01-25	2029-01-18
CON3920	Installation Subcontractors Selection and Award	2027-01-25	2027-04-25
CON3930	Advance Payment	2027-04-25	2027-06-09
CON3940	Installation Subcontractor Mobilize on Site	2027-06-09	2027-11-06
Mechanical and E&I Installation		2027-11-25	2029-01-18
S08	Cast House	2028-05-20	2029-01-18
Installation		2028-05-20	2029-01-18
CON3950	Installation Overhead Crane	2028-05-20	2028-08-18
CON3960	MEI Installation and Cabling	2028-07-20	2028-12-19
CON3970	No Load Interlocking Test	2028-12-20	2029-01-18
S09	Crucible Cleaning Workshop	2028-05-30	2028-10-29
Installation		2028-05-30	2028-10-29
CON3980	Equipment, Dust Collector System, and Electrical System	2028-05-30	2028-09-29
CON3990	No Load Test	2028-09-30	2028-10-29
S10	Dross Treatment Workshop	2028-09-30	2029-01-13
Installation		2028-09-30	2029-01-13
CON4000	Equipment, Dust Collector System, and Electrical System	2028-09-30	2028-12-14
CON4010	No Load Test	2028-12-15	2029-01-13
S11	Carbon Deposit Treatment Workshop	2028-09-09	2028-12-09
Installation		2028-09-09	2028-12-09
CON4020	Equipment, Dust Collector System, and Electrical System	2028-09-09	2028-11-08
CON4030	No Load Test	2028-11-09	2028-12-09
A1202	Stem and Stub Repair Workshop	2028-10-30	2028-12-14
CON4040	Installation and Test	2028-10-30	2028-12-14
S13	SPL Temporary Storage	2028-11-09	2028-11-29
Installation		2028-11-09	2028-11-29
CON4050	Equipment and Electrical System	2028-11-09	2028-11-29
U0704	Diesel Generator Room	2027-11-25	2027-12-04
CON4060	Installation of Equipment	2027-11-25	2027-12-04
U09	Compressor Air Station	2027-12-21	2028-06-04
CON4070	Installation of Equipment	2027-12-21	2028-04-20
CON4080	No Load Test	2028-04-21	2028-06-04
U11	Circulating Water System for Cast House	2028-07-30	2028-11-18
CON4090	Installation of Equipment	2028-07-30	2028-10-29
CON4100	No Load Test	2028-10-29	2028-11-18
U12	Circulating Water System for Compressor Station	2028-03-31	2028-07-30
CON4110	Installation of Equipment	2028-03-31	2028-06-30
CON4120	No Load Test	2028-07-01	2028-07-30
U33	Natural Gas Press Regulating Station	2028-06-04	2028-09-24
CON4130	MEI Installation	2028-06-04	2028-09-03
CON4140	No Load Test	2028-09-04	2028-09-24
M01	Comprehensive Office Building	2028-04-30	2028-06-13
CON4150	Installation of Air Conditioning and Ventilation Equipment	2028-04-30	2028-06-13
M02	Reduction Area Comprehensive Building	2028-03-30	2028-06-13
CON4160	Installation of Air Conditioning & Ventilation and Lab Equipment	2028-03-30	2028-06-13
M03	Dining Hall	2028-05-15	2028-06-13
CON4170	Installation of Air Conditioning and Ventilation Equipment	2028-05-15	2028-06-13
M04	Shower Room	2028-05-15	2028-06-29
CON4180	Installation of Air Conditioning and Ventilation Equipment	2028-05-15	2028-06-29
S00	Aluminum Reduction Plant (Cathode Assembling) Installation Package (i)	2027-02-23	2029-10-05
CON4190	Installation Subcontractors Selection and Award	2027-02-23	2027-05-24
CON4200	Advance Payment	2027-05-24	2027-07-08
CON4210	Installation Subcontractor Mobilize on Site	2027-07-08	2027-12-05
CON4220	Cathode Assembling	2028-01-04	2029-10-05
A00	Anode Plant (Anode Rodding Shop) Civil Work Package (11)	2026-06-24	2028-12-14
CON4230	BOQ Preparation	2026-06-24	2026-07-19
Bidding		2026-07-19	2026-09-06
CON4240	Bidding	2026-07-19	2026-08-02
CON4250	Tendering and Bid Clarification Meeting	2026-08-02	2026-09-06
Civil Subcontractors Selection and Award		2026-09-06	2026-12-15
CON4260	Contractor Evaluation	2026-09-06	2026-10-06
CON4270	Employer Evaluation and Award	2026-10-06	2026-11-05
CON4280	Advance Payment	2026-11-05	2026-12-15
Civil Subcontractor Mobilize on Site		2026-12-15	2027-05-14
CON4290	Civil Subcontractor Mobilize on Site	2026-12-15	2027-05-14
Civil Construction		2027-04-14	2028-12-14
S05	Fluoride Storage	2027-04-14	2027-08-03

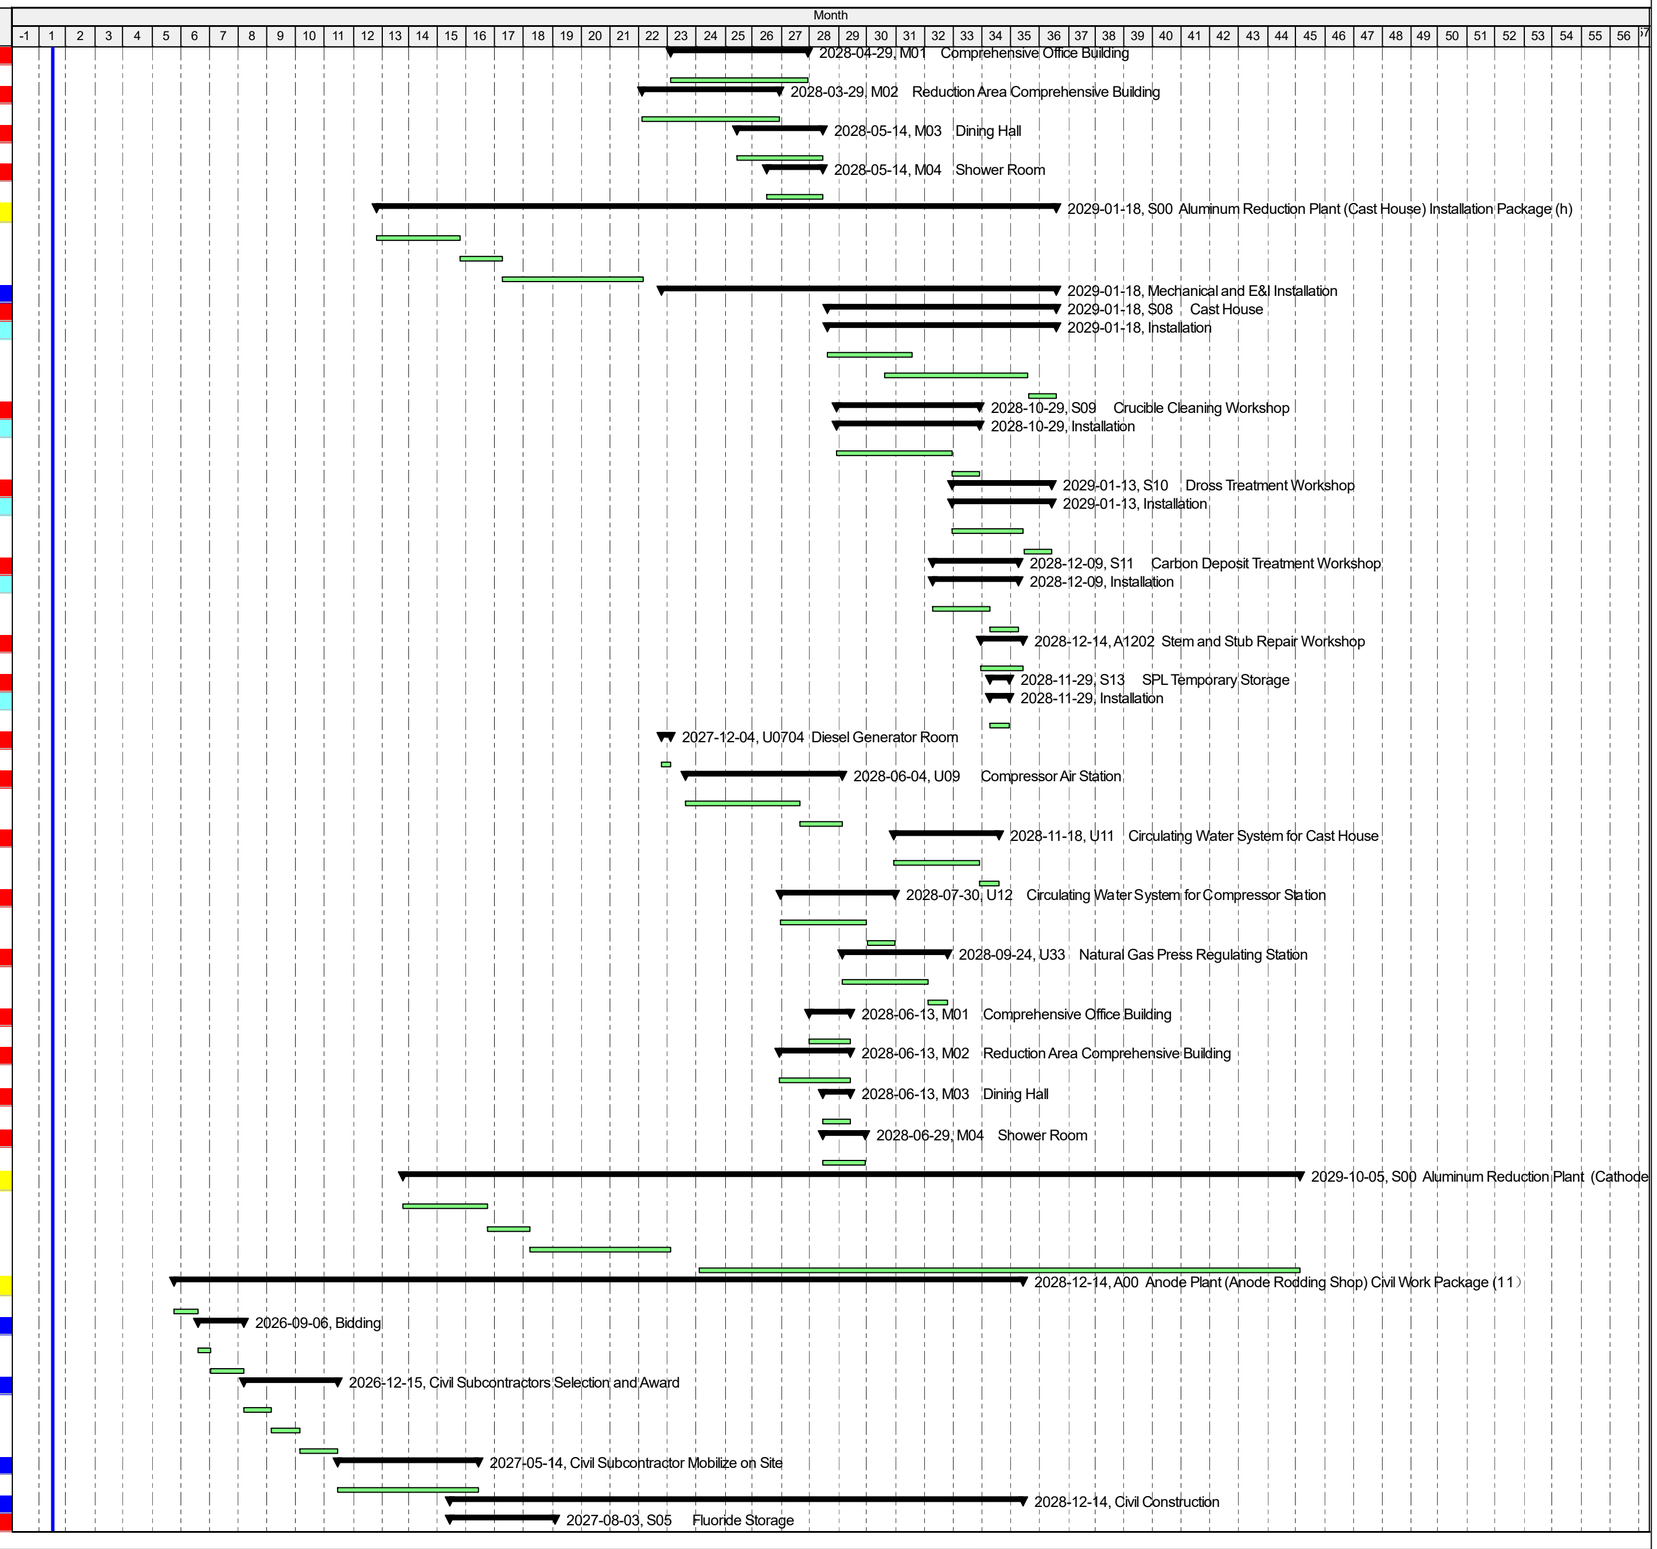

Remaining Level of Effort | Actual Work | Critical Remaining Work | summary
Actual Level of Effort | Remaining Work | Milestone

Project Schedule(Level 3)

Activity ID	Activity Name	Start	Finish
CON4300	Construction Preparation	2027-04-14	2027-05-04
CON4310	Civil Work and Steel Structure	2027-05-05	2027-08-03
A0501	Butts Treatment Shop	2027-09-20	2028-03-19
	Civil Work and Steel Structure	2027-09-20	2028-03-19
CON4320	Construction Preparation	2027-09-20	2027-10-19
CON4330	Plant and Equipment Foundation	2027-10-20	2028-01-18
CON4340	Silo Foundation	2027-10-20	2028-01-18
CON4350	Steel Structure/Component Assembling	2027-12-20	2028-02-03
CON4360	Steel Structure Erection	2027-12-25	2028-02-08
CON4370	Cladding of Roof and Wall, and Decoration	2028-01-24	2028-02-18
CON4380	Concrete Floor	2028-02-20	2028-03-19
A0502	Butts Treatment Shop	2028-03-16	2028-09-13
	Civil Work and Steel Structure	2028-03-16	2028-09-13
CON4390	Construction Preparation	2028-03-16	2028-04-13
CON4400	Plant and Equipment Foundation	2028-04-14	2028-06-13
CON4410	Steel Structure/Component Assembling	2028-04-30	2028-06-13
CON4420	Steel Structure Erection	2028-06-14	2028-07-14
CON4430	Cladding of Roof and Wall, and Decoration	2028-07-15	2028-08-13
CON4440	Concrete Floor	2028-08-14	2028-09-13
A1001	Anode Rodding Shop	2027-05-14	2028-05-14
	Civil Work and Steel Structure	2027-05-14	2028-05-14
CON4450	Construction Preparation	2027-05-14	2027-06-13
CON4460	Plant Foundation	2027-06-14	2027-10-13
CON4470	Steel Structure/Component Assembling	2027-06-29	2027-10-29
CON4480	Steel Structure, Roofing, and Cladding	2027-07-14	2027-11-13
CON4490	Indoor Pit and Equipment Foundation	2027-10-15	2028-02-13
CON4500	Flooring and Decoration	2028-02-14	2028-04-13
CON4510	Attached Building	2027-08-14	2027-10-19
CON4520	Completion of Civil Work	2028-04-14	2028-05-14
A1002	Anode Rodding Shop	2027-11-14	2028-12-14
	Civil Work and Steel Structure	2027-11-14	2028-12-14
CON4530	Construction Preparation	2027-11-14	2027-12-14
CON4540	Plant Foundation	2027-12-15	2028-04-13
CON4550	Steel Structure/Component Assembling	2027-12-30	2028-04-25
CON4560	Steel Structure, Roofing, and Cladding	2028-01-14	2028-05-14
CON4570	Indoor Pit and Equipment Foundation	2028-05-15	2028-09-13
CON4580	Flooring and Decoration	2028-09-14	2028-11-13
CON4590	Attached Building	2028-03-16	2028-05-14
CON4600	Completion of Civil Work	2028-11-14	2028-12-14
A1101	Bath Treatment System	2028-02-13	2028-05-14
CON4610	Civil Work and Steel Structure	2028-02-13	2028-05-14
A1102	Bath Treatment System	2028-05-15	2028-08-13
CON4620	Civil Work and Steel Structure	2028-05-15	2028-08-13
U06	10kV Power Distribution Room in Anode Area	2027-11-04	2028-01-03
CON4630	Civil Work and Steel Structure	2027-11-04	2028-01-03
U0703	Diesel Generator Room	2028-02-03	2028-04-03
CON4640	Civil Work and Steel Structure	2028-02-03	2028-04-03
U15	Circulating Water System for Green Anode Shop	2028-03-20	2028-06-18
CON4650	Civil Work and Steel Structure	2028-03-20	2028-06-18
U16	Circulating Water System for Anode Rodding Shop	2028-03-16	2028-06-13
CON4660	Civil Work and Steel Structure	2028-03-16	2028-06-13
A00	Anode Plant (Anode Rodding Shop) Installation Package (j)	2026-10-15	2029-07-24
CON4670	Installation Subcontractors Selection and Award	2026-10-15	2027-01-22
CON4680	Advance Payment	2027-01-22	2027-03-08
CON4690	Installation Subcontractor Mobilize on Site	2027-03-08	2027-08-05
	Mechanical and E&I Installation	2027-09-04	2029-07-24
S05	Fluoride Storage	2028-10-04	2028-12-04
CON4700	Installation	2028-10-04	2028-11-03
CON4710	No Load Test	2028-11-04	2028-12-04
A0501	Butts Treatment	2028-01-20	2028-08-03
	Installation	2028-01-20	2028-08-03
CON4720	Silo Erection	2028-01-20	2028-05-19
CON4730	Equipment and Electrical System	2028-03-20	2028-06-13
CON4740	No Load Test	2028-06-14	2028-08-03
A0502	Butts Treatment	2028-09-14	2028-12-04
	Installation	2028-09-14	2028-12-04
CON4750	Equipment and Electrical System	2028-09-14	2028-11-13
CON4760	Test	2028-11-14	2028-12-04
A1001	Anode Rodding Shop	2027-10-15	2028-10-14
	Installation	2027-10-15	2028-10-14
CON4770	Steel Structure/Component of Suspension Chain Conveyor Assembling	2027-10-15	2027-12-14
CON4780	Frequency Induction Furnace, etc.	2028-01-14	2028-04-13
CON4790	Test	2028-04-14	2028-06-13
CON4800	Installation of Suspension Chain and Conveyor Equipment	2027-12-15	2028-03-15
CON4810	Installation of Working Stations, Electrical Equipment, and Instrumentation	2028-02-14	2028-07-14

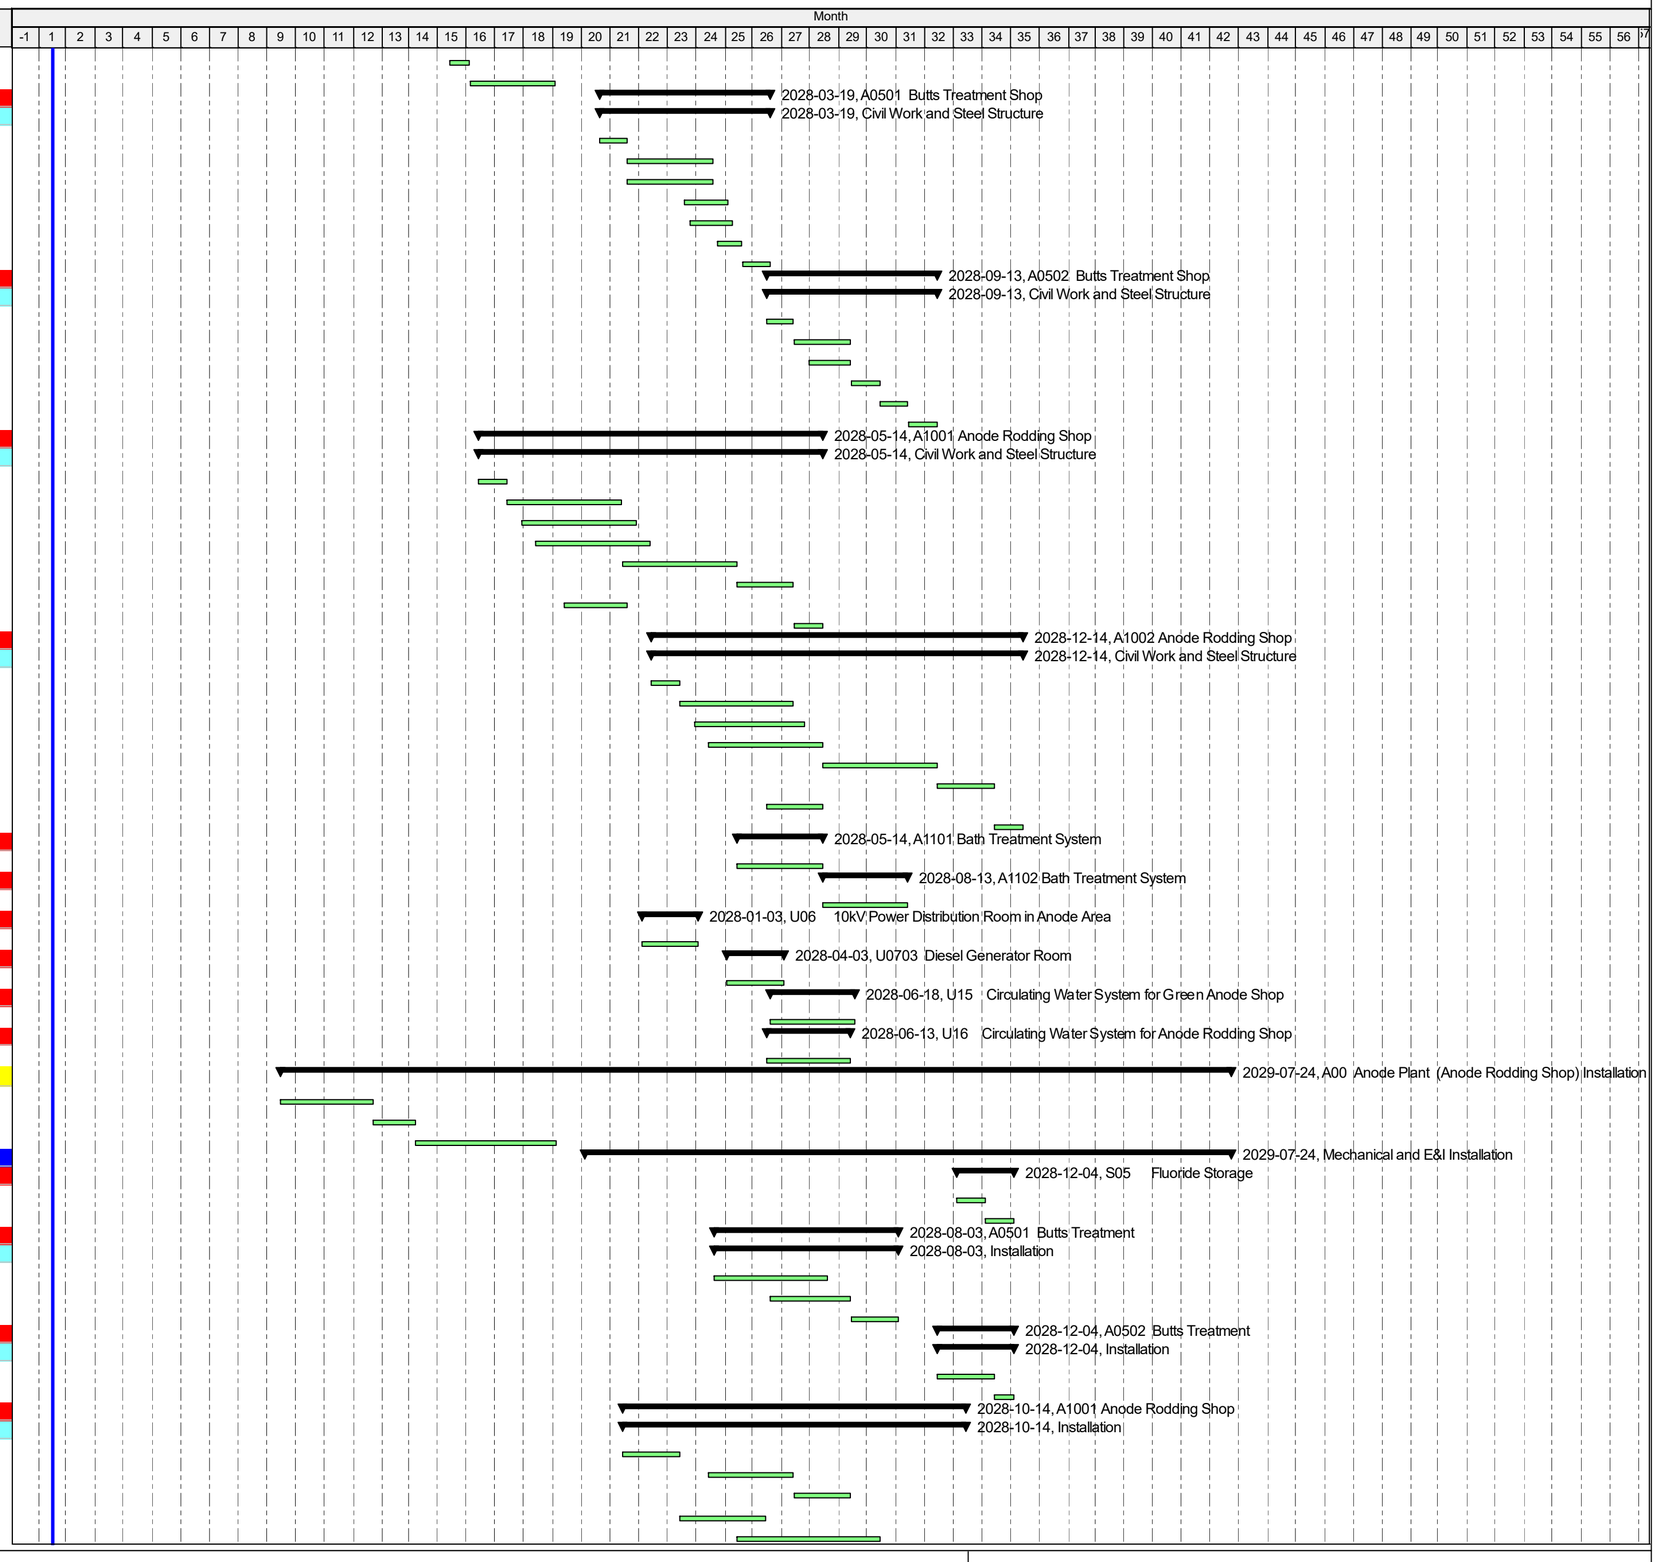

Remaining Level of Effort | Actual Work | Critical Remaining Work | summary
Actual Level of Effort | Remaining Work | Milestone

Project Schedule(Level 3)

Activity ID	Activity Name	Start	Finish
CON4820	Piping and Cabling	2028-03-16	2028-09-13
CON4830	No Load Test	2028-09-14	2028-10-14
A1002 Anode Rodding Shop		2028-05-15	2029-07-24
Installation		2028-05-15	2029-07-24
CON4840	Steel Structure/Component of Suspension Chain Conveyor Assembling	2028-05-15	2028-07-14
CON4850	Installation of Suspension Chain and Conveyor Equipment	2028-07-15	2028-11-13
CON4860	Installation of Working Stations, Electrical Equipment, and Instrumentation	2028-11-14	2029-04-13
CON4870	Piping and Cabling	2029-01-14	2029-06-13
CON4880	No Load Test	2029-06-14	2029-07-24
A1101 Bath Treatment System		2028-05-15	2028-10-19
CON4890	MEI Installation	2028-05-15	2028-09-18
CON4900	No Load Test	2028-09-20	2028-10-19
A1102 Bath Treatment System		2028-08-14	2029-01-13
CON4910	MEI Installation	2028-08-14	2028-12-14
CON4920	No Load Test	2028-12-15	2029-01-13
U0703 Diesel Generator Room		2028-04-04	2028-04-13
CON4930	Installation of Equipment	2028-04-04	2028-04-13
U15 Circulating Water System for Green Anode Shop		2028-06-20	2028-10-19
CON4940	Installation of Equipment	2028-06-20	2028-09-18
CON4950	No Load Test	2028-09-20	2028-10-19
U16 Circulating Water System for Anode Rodding Shop		2028-06-14	2028-10-24
CON4960	Installation of Equipment	2028-06-14	2028-09-08
CON4970	No Load Test	2028-09-09	2028-10-24
U23 Pot Maintenance Shop		2027-09-04	2028-01-03
Installation		2027-09-04	2028-01-03
CON4980	Installation of Overhead Crane and Electrical Equipment	2027-09-04	2027-11-03
CON4990	Installation of Intermediate Frequency Furnace	2027-10-05	2027-12-04
CON5000	Test	2027-12-05	2028-01-03
A00 Anode Plant (Green Anode Shop) Civil Work Package (12)		2026-05-17	2028-11-03
CON5010	BOQ Preparation	2026-05-17	2026-06-16
Civil Subcontractors Selection and Award		2026-06-17	2026-11-02
CON5020	Bidding	2026-06-17	2026-07-01
CON5030	Tendering and Bid Clarification Meeting	2026-07-02	2026-08-01
CON5040	Contractor Evaluation	2026-08-02	2026-09-01
CON5050	Employer Evaluation and Award	2026-09-02	2026-10-02
CON5060	Advance Payment	2026-10-03	2026-11-02
Civil Subcontractor Mobilize on Site		2026-11-04	2027-04-03
CON5070	Civil Subcontractor Mobilize on Site	2026-11-04	2027-04-03
Civil Construction		2027-03-16	2028-11-03
A01 GPC Storage and Conveying		2027-05-05	2028-05-04
CON5080	Civil Work and Steel Structure (axis 1-27)	2027-05-05	2027-09-01
CON5090	Civil Work and Steel Structure (axis 35-45)	2027-05-05	2027-08-07
CON5100	Civil Work and Steel Structure (axis 27-35)	2028-02-04	2028-05-04
A0201 Calcination Shop		2027-05-05	2027-11-18
CON5110	Foundation	2027-05-05	2027-08-03
CON5120	Steel Structure	2027-06-04	2027-09-03
CON5130	Cladding of Roof and Wal	2027-09-04	2027-11-18
A0202 Calcination Shop		2027-08-04	2028-02-18
CON5140	Foundation	2027-08-04	2027-11-03
CON5150	Steel Structure	2027-09-04	2027-12-04
CON5160	Cladding of Roof and Wal	2027-12-05	2028-02-18
A03 Green Anode Shop		2027-03-16	2028-11-03
Civil Work and Steel Structure		2027-03-16	2028-11-03
CON5170	Construction Preparation	2027-03-16	2027-04-03
CON5180	Plant and Equipment Foundation	2027-04-04	2027-08-03
CON5190	Framework and Roof of Floor 1&2	2027-06-04	2027-09-03
CON5200	Framework from Floor 3 To Floor 8	2027-08-04	2028-04-03
CON5210	Roofing & Waterproofing	2027-10-05	2028-05-04
CON5220	Cladding of Floor 1 To Floor 6	2028-04-04	2028-08-03
CON5230	Indoor and Outdoor Plastering and Decoration	2028-05-05	2028-09-03
CON5240	Flooring	2028-07-05	2028-11-03
CON5250	Foundation of Equipment/Silo	2027-06-14	2027-09-08
CON5260	Erection of Belt Gallery and Steel Structure on Silo	2028-04-09	2028-07-09
A06 Solid Pitch Storage		2028-01-20	2028-05-19
CON5270	Civil Work and Steel Structure	2028-01-20*	2028-05-19
A07 Pitch Melting Shop		2028-03-01	2028-08-03
CON5280	Civil Work and Steel Structure	2028-04-04*	2028-08-03
CON5290	Tank and Equipment Foundation	2028-03-01	2028-04-08
A09 Calcination Fume Treatment Center		2027-09-04	2028-03-05
CON5300	Foundation	2027-09-04	2028-01-03
CON5310	Steel Structure	2028-01-04	2028-03-05
A13 Waste Heat Boiler Room		2027-09-03	2028-01-20
CON5320	Boiler Foundation	2027-09-03	2027-12-19
CON5330	Civil Work and Steel Structure for Building	2027-09-20	2028-01-20
A14 Heat Transfer Medium Boiler and Pump Room		2027-12-05	2028-05-18

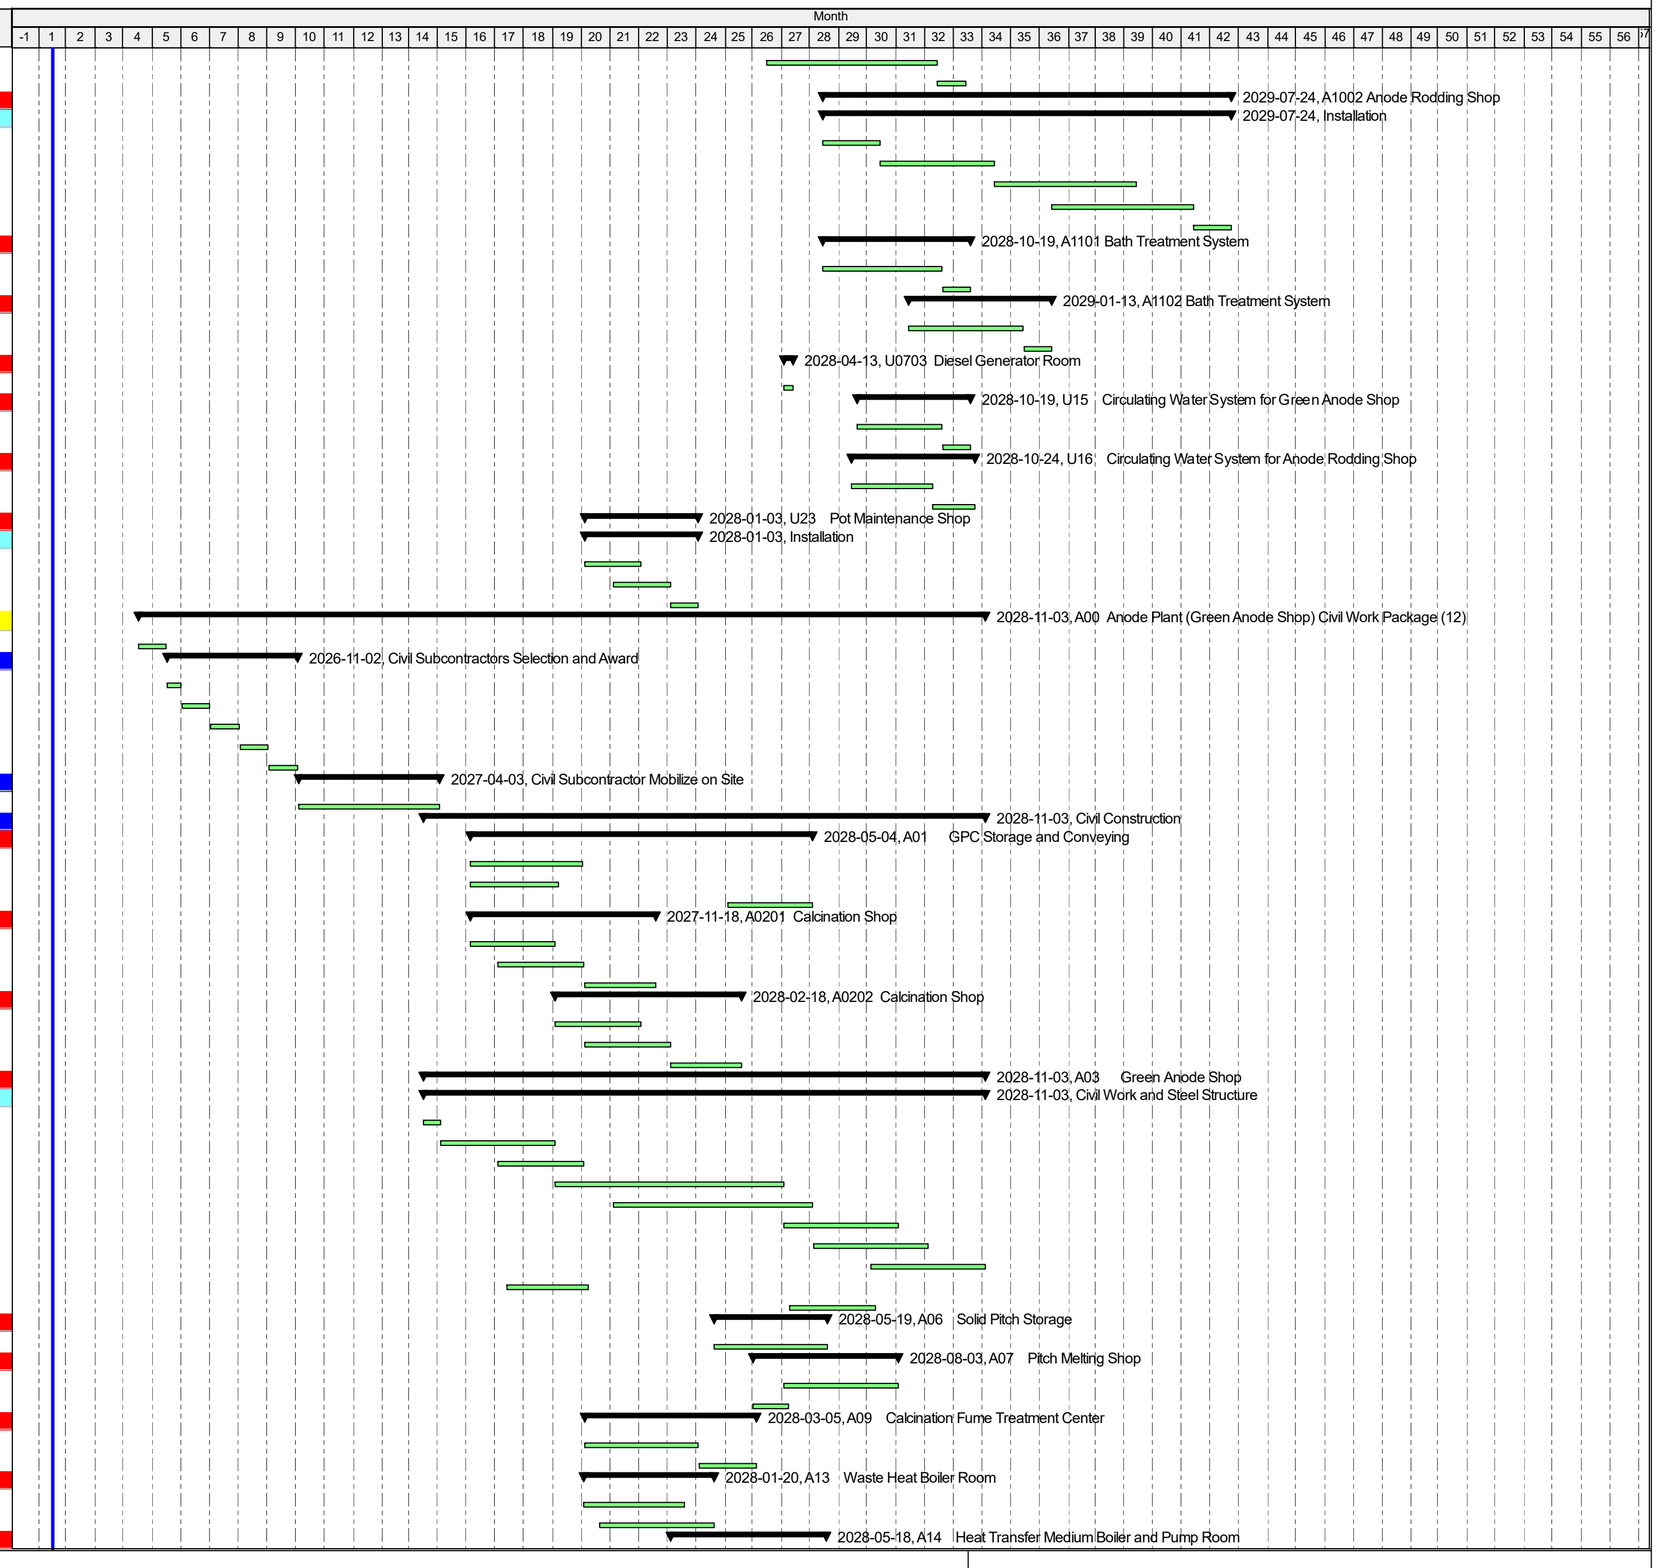

Remaining Level of Effort | Actual Work | Critical Remaining Work | summary
Actual Level of Effort | Remaining Work | Milestone

Project Schedule(Level 3)

Activity ID	Activity Name	Start	Finish
CON5340	Boiler Foundation	2027-12-05	2028-02-08
CON5350	Civil Work and Steel Structure for Building	2028-02-03	2028-05-18
U14	Circulating Water System for Calcination Shop	2027-12-05	2028-03-19
CON5360	Civil Work and Steel Structure	2027-12-05	2028-03-19
U24	Carbon Repair Room	2028-03-20	2028-06-18
CON5370	Civil Work and Steel Structure	2028-03-20	2028-06-18
A00	Anode Plant (Green Anode Shop) Intallation Package (k)	2026-10-24	2028-11-03
CON5380	Installation Subcontractors Selection and Award	2026-10-24	2027-01-22
CON5390	Advance Payment	2027-01-22	2027-03-08
CON5400	Mechanical Subcontractor Mobilize on Site	2027-03-08	2027-08-05
	Mechanical and E&I Installation	2027-09-04	2028-11-03
A01	GPC Storage and Conveying	2028-04-04	2028-08-03
CON5410	Installation of Equipment	2028-04-04	2028-07-04
CON5420	No Load Test	2028-07-05	2028-08-03
A0201	Calcination Shop	2027-09-04	2028-08-08
CON5430	Steel Structure	2027-09-04	2027-11-18
CON5440	VSF Lining	2027-11-20	2028-02-18
CON5450	Installation of Equipment and Duct	2027-12-20	2028-04-18
CON5460	E&I and Cabling	2028-02-18	2028-06-24
CON5470	No Load Test	2028-06-25	2028-08-08
A0202	Calcination Shop	2027-12-05	2028-10-04
CON5480	Steel Structure	2027-12-05	2028-02-18
CON5490	VSF Lining	2028-02-20	2028-05-19
CON5500	Installation of Equipment and Duct	2028-03-20	2028-07-19
CON5510	E&I and Cabling	2028-04-20	2028-08-24
CON5520	No Load Test	2028-08-25	2028-10-04
A03	Green Anode Shop	2027-09-04	2028-10-19
	Installation	2027-09-04	2028-10-19
CON5530	Erection of Steel Silos	2027-09-09	2028-04-08
CON5540	Installation of Equipment (Vertical Mill, Breaker, Vibrating Former, Preheate	2027-09-04	2028-07-04
CON5550	Installation of Conveying Equipment	2028-07-11	2028-09-08
CON5560	Installation of Electrical Equipment, Instrumentation and Piping	2027-11-04	2028-09-29
CON5570	No Load Test	2028-08-20	2028-10-19
A06	Solid Pitch Storage	2028-05-20	2028-08-18
CON5580	Equipment Installation	2028-05-20*	2028-07-19
CON5590	No Load Test	2028-07-20	2028-08-18
A07	Pitch Melting Shop	2028-04-09	2028-10-19
CON5600	Tank and Pump Installation	2028-04-09	2028-06-08
CON5610	Equipment Installation	2028-06-04*	2028-09-03
CON5620	No Load Test	2028-09-04	2028-10-19
A13	Waste Heat Boiler Room	2027-12-20	2028-10-19
CON5630	Boiler Steel Structure	2027-12-20	2028-03-19
CON5640	Boiler Installation	2028-02-20	2028-06-18
CON5650	Lining and Insulation	2028-05-20	2028-08-18
CON5660	MEI & Duct Installation	2028-04-20	2028-09-18
CON5670	No Load Test	2028-09-20	2028-10-19
A14	Heat Transfer Medium Boiler and Pump Room	2028-03-20	2028-11-03
CON5680	Boiler Steel Structure	2028-03-20	2028-05-19
CON5690	Boiler Installation	2028-05-20	2028-08-18
CON5700	Lining and Insulation	2028-07-20	2028-09-18
CON5710	MEI & Duct Installation	2028-07-05	2028-10-04
CON5720	No Load Test	2028-10-05	2028-11-03
U14	Circulating Water System for Calcination Shop	2028-03-20	2028-07-04
CON5730	Installation of Equipment	2028-03-20	2028-06-03
CON5740	No Load Test	2028-06-04	2028-07-04
U24	Carbon Repair Room	2028-06-20	2028-09-17
CON5750	Installation of Equipment	2028-06-20	2028-08-18
CON5760	No Load Test	2028-08-19	2028-09-17
A00	Anode Plant (Baking Furnace) Civil Work Package (13)	2026-06-08	2029-04-13
CON5770	BOQ Preparation	2026-06-08	2026-07-08
	Civil Subcontractors Selection and Award	2026-07-08	2027-04-13
CON5780	Bidding	2026-07-08	2026-07-22
CON5790	Tendering and Bid Clarification Meeting	2026-07-22	2026-08-31
CON5800	Contractor Evaluation	2026-08-31	2026-09-30
CON5810	Employer Evaluation and Award	2026-09-30	2026-10-30
CON5820	Advance Payment	2026-10-30	2026-12-14
CON5830	Civil Subcontractor Mobilize on Site	2026-12-14	2027-04-13
	Civil Construction	2027-04-14	2029-04-13
A0401	Baking Furnace & Anode Transfer Station	2027-04-14	2028-10-04
	Civil Work and Steel Structure	2027-04-14	2028-10-04
CON5840	Construction Preparation	2027-04-14	2027-05-04
CON5850	Transfer Station Foundation	2027-05-05	2027-09-03
CON5860	Transfer Station Steel Structure, Roof and Cladding	2027-06-04	2027-10-04

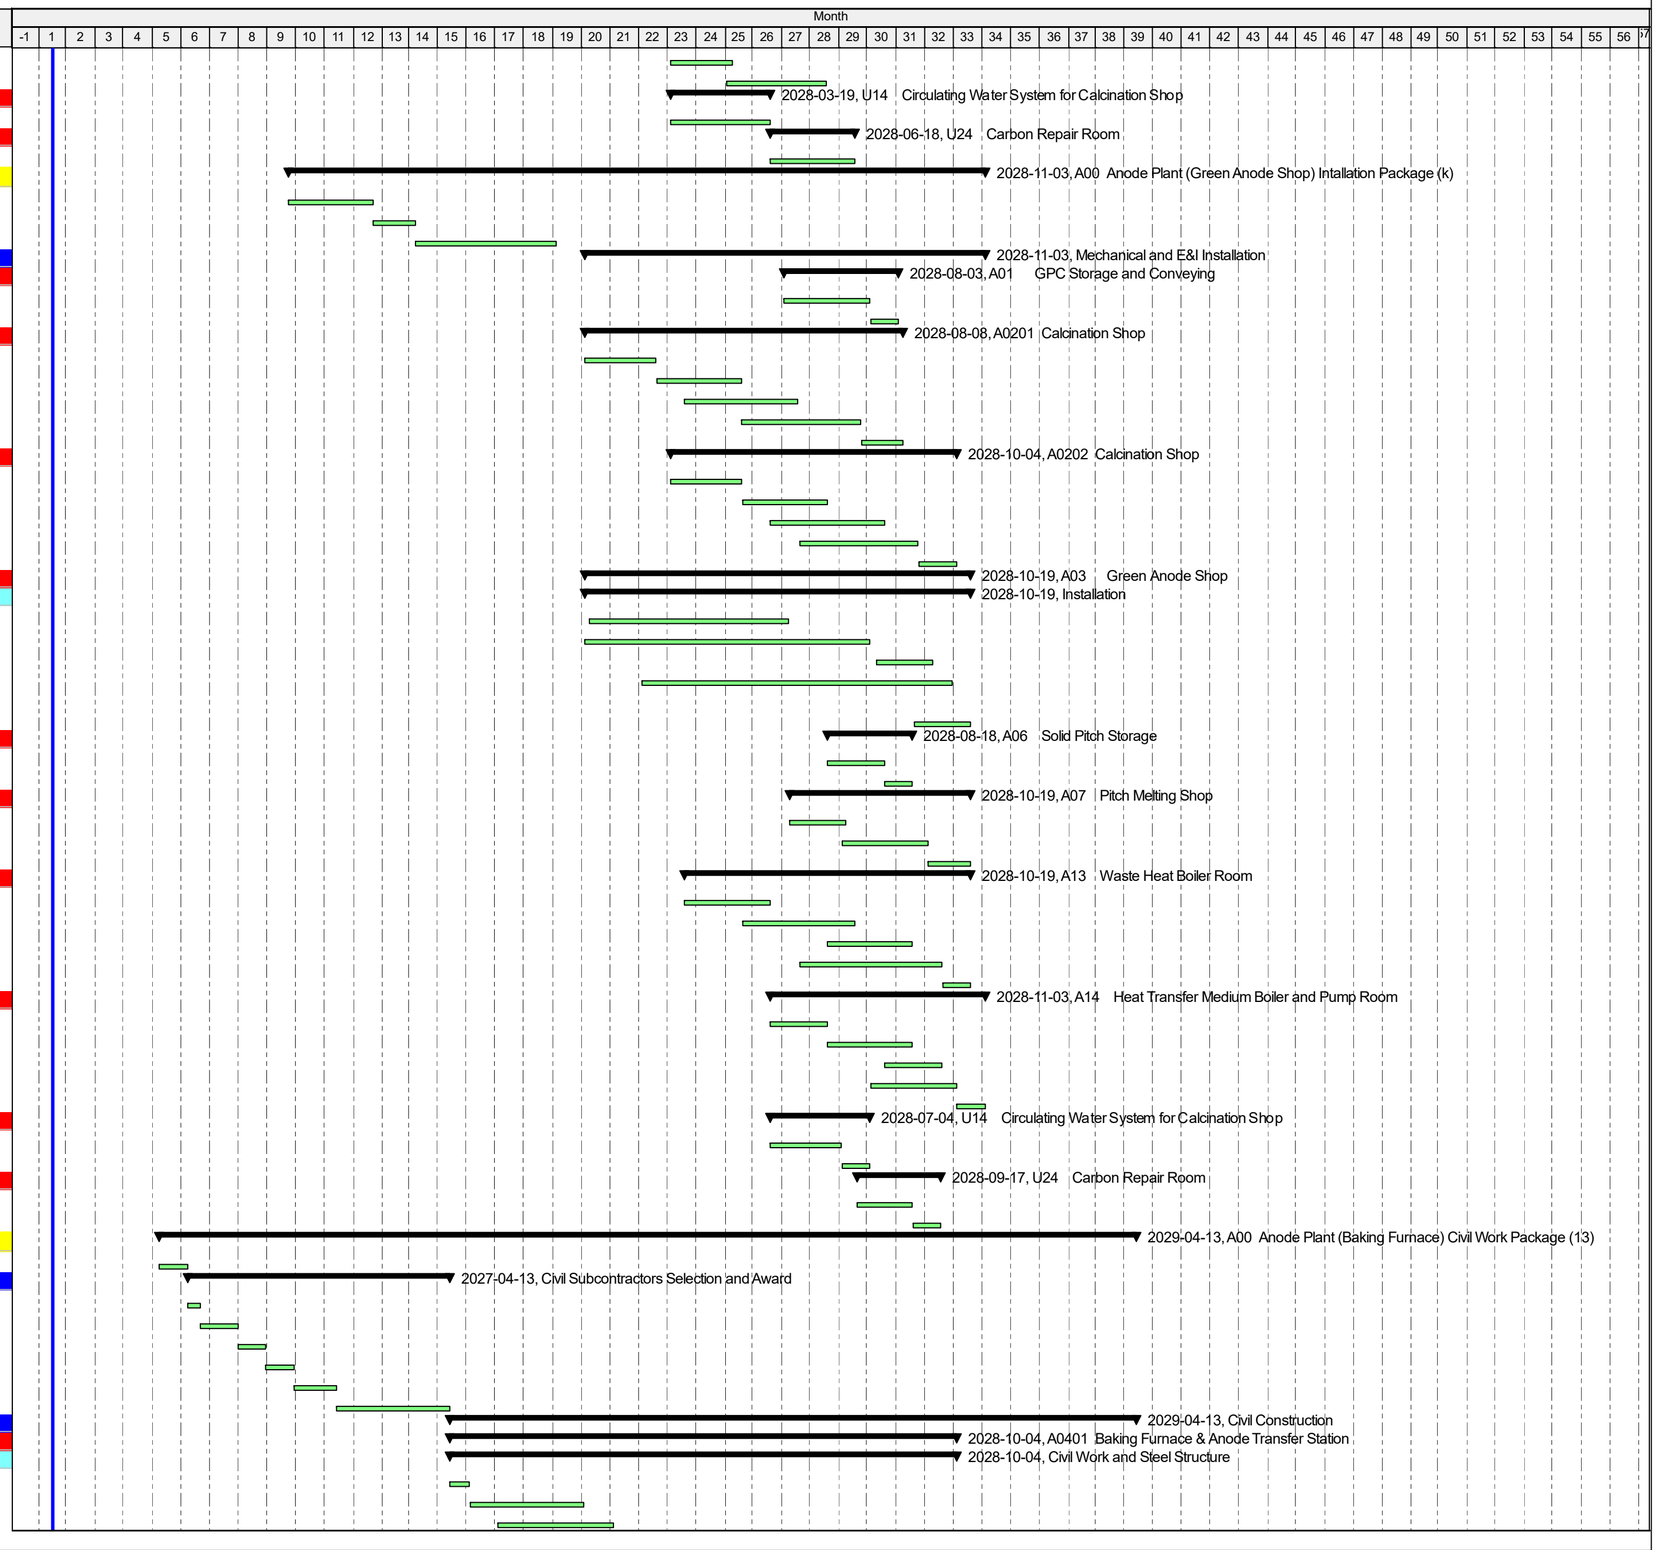

Remaining Level of Effort | Actual Work | Critical Remaining Work | summary
Actual Level of Effort | Remaining Work | Milestone

Project Schedule(Level 3)

Activity ID	Activity Name	Start	Finish
CON5870	Transfer Station Equipment Foundation	2028-06-04	2028-08-03
CON5880	Baking Shop Foundation	2027-05-05	2027-09-03
CON5890	Steel Structure/Component Assembling	2027-05-20	2027-09-18
CON5900	Baking Shop Steel Structure Erection and Roofing 1-1	2027-06-04	2027-08-03
CON5910	Baking Shop Steel Structure Erection and Roofing 1-2	2027-08-04	2027-10-04
CON5920	Cladding and Decoration	2027-08-04	2028-01-03
CON5930	Furnace Foundation 1-1	2027-08-04	2027-11-03
CON5940	Furnace Foundation 1-2	2027-11-04	2028-02-03
CON5950	Grouping and Cleaning Machine Foundation 1-1	2028-04-04	2028-06-03
CON5960	Grouping and Cleaning Machine Foundation 1-2	2028-08-04	2028-10-04
A0402 Baking Furnace & Anode Transfer Station		2027-10-15	2029-04-13
Civil Work and Steel Structure		2027-10-15	2029-04-13
CON5970	Construction Preparation	2027-10-15	2027-11-13
CON5980	Transfer Station Foundation	2027-11-14	2028-02-13
CON5990	Transfer Station Steel Structure, Roof and Cladding	2027-12-15	2028-04-13
CON6000	Transfer Station Equipment Foundation	2028-12-15	2029-02-13
CON6010	Baking Shop Foundation 2-1	2027-11-14	2028-01-13
CON6020	Baking Shop Foundation 2-2	2028-01-14	2028-03-15
CON6030	Steel Structure/Component Assembling	2027-11-30	2028-03-29
CON6040	Baking Steel Structure Erection and Roofing 2-1	2027-12-15	2028-02-13
CON6050	Baking Steel Structure Erection and Roofing 2-2	2028-02-14	2028-04-13
CON6060	Cladding and Decoration	2028-02-14	2028-07-14
CON6070	Furnace Foundation 2-1	2028-02-14	2028-05-14
CON6080	Furnace Foundation 2-2	2028-05-15	2028-08-13
CON6090	Grouping and Cleaning Machine Foundation 2-1	2028-10-15	2028-12-14
CON6100	Grouping and Cleaning Machine Foundation 2-2	2029-02-14	2029-04-13
A08 Baking Furnace Fume Treatment Center		2028-01-04	2028-11-13
CON6110	Chimney Foundation (Phase 1A)	2028-01-04	2028-02-18
CON6120	Chimney Foundation (Phase 1B)	2028-05-15	2028-08-13
CON6130	Foundation of Dust Collector and Equipment (Phase 1A)	2028-02-20	2028-04-18
CON6140	Foundation of Dust Collector and Equipment (Phase 1B)	2028-08-14	2028-11-13
A00 Anode Plant (Baking Furnace) Installation Package (I)		2026-10-24	2029-08-13
CON6150	Installation Subcontractors Selection and Award	2026-10-24	2027-01-22
CON6160	Advance Payment	2027-01-22	2027-03-08
CON6170	Mechanical Subcontractor Mobilize on Site	2027-03-08	2027-08-05
Mechanical and E&I Installation		2027-11-04	2029-08-13
A0401 Baking Furnace & Anode Transfer Station		2027-11-04	2029-02-03
Installation		2027-11-04	2029-02-03
CON6180	Furnace Lining and Duct & Steel Structure Installation 1-1	2027-11-04	2028-04-03
CON6190	Furnace Lining and Duct & Steel Structure Installation 1-2	2028-03-06	2028-08-03
CON6200	Duct and Equipment Installation	2028-08-04	2028-10-02
CON6210	Grouping and Cleaning Machine Installation	2028-05-05	2028-11-03
CON6220	Stacking Crane Installation	2028-01-04	2028-05-04
CON6230	FAT Installation	2028-05-05	2028-11-27
CON6240	Installation of Electrical Equipment, Instrumentation and Piping	2028-06-04	2028-12-04
CON6250	Transfer Station Equipment Installation and Piping	2028-08-04	2029-01-03
CON6260	No Load Test	2029-01-04	2029-02-03
A0402 Baking Furnace & Anode Transfer Station		2028-05-15	2029-08-13
Installation		2028-05-15	2029-08-13
CON6270	Furnace Lining and Duct & Steel Structure Installation 2-1	2028-05-15	2028-10-14
CON6280	Furnace Lining and Duct & Steel Structure Installation 2-2	2028-09-14	2029-02-13
CON6290	Duct and Equipment Installation	2029-02-14	2029-04-13
CON6300	Grouping and Cleaning Machine Installation	2028-11-14	2029-05-14
CON6310	Stacking Crane Installation	2028-07-15	2028-11-13
CON6320	FAT Installation	2028-11-14	2029-06-08
CON6330	Installation of Electrical Equipment, Instrumentation and Piping	2028-12-15	2029-06-13
CON6340	Transfer Station Equipment Installation and Piping	2029-02-14	2029-07-14
CON6350	No Load Test	2029-07-15	2029-08-13
U00 Utilities (Rectifier Station) Civil Work Package (14)		2026-05-06	2029-01-03
CON6360	BOQ Preparation	2026-05-06	2026-06-05
Civil Subcontractors Selection and Award		2026-06-05	2027-03-17
CON6370	Bidding	2026-06-05	2026-07-20
CON6380	Contractor Evaluation	2026-07-20	2026-08-19
CON6390	Employer Evaluation and Award	2026-08-19	2026-09-18
CON6400	Advance Payment	2026-09-18	2026-11-02
CON6410	Civil Subcontractor Mobilize on Site	2026-11-02	2027-03-17
Civil Construction		2027-03-17	2029-01-03
E01 Raw Material Conveying system		2027-09-30	2028-07-09
CON6420	Civil Work and Steel Structure	2027-09-30*	2028-07-09
S03 Alumina Storage		2027-08-14	2028-03-10
CON6430	Construction Preparation	2027-08-14	2027-09-13
CON6440	Silo Foundation and Civil Work	2027-09-14	2028-03-10
A1201 Stem and Stub Repair Workshop		2027-06-04	2027-09-29
CON6450	Civil Work and Steel Structure	2027-06-04	2027-09-29

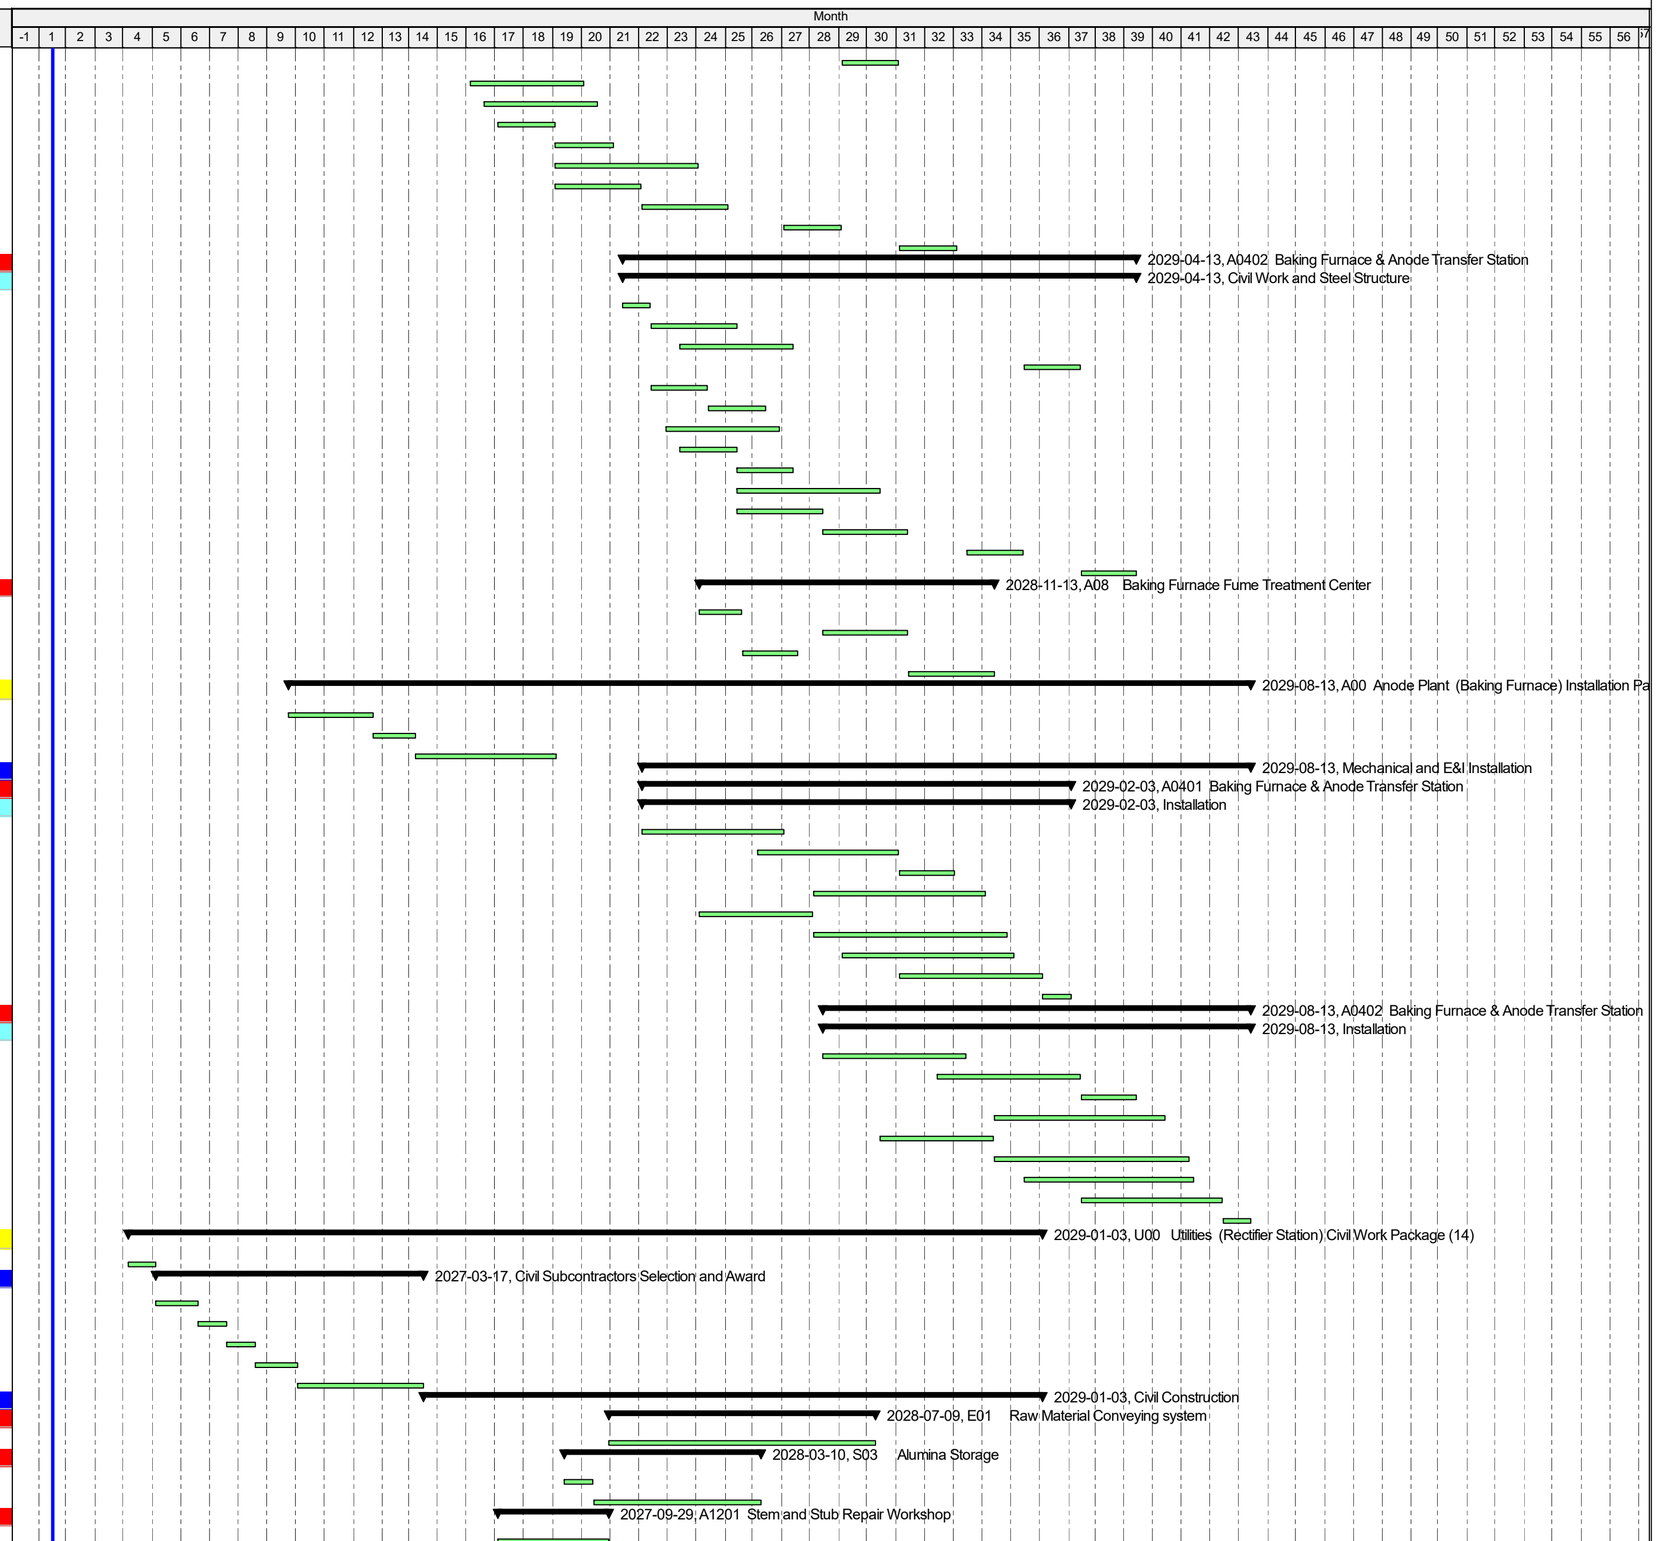

Remaining Level of Effort | Actual Work | Critical Remaining Work | summary
Actual Level of Effort | Remaining Work | Milestone

Project Schedule(Level 3)

Activity ID	Activity Name	Start	Finish
U0101	330kV Power Distribution Device	2027-08-14	2028-05-04
	Civil Work and Steel Structure	2027-08-14	2028-05-04
CON6460	Construction Preparation	2027-08-14	2027-09-13
CON6470	Civil Work and Steel Structure	2027-09-14	2028-04-03
CON6480	Foundation of Equipment	2027-09-14	2028-05-04
U0102	330kV Power Distribution Device	2028-01-14	2028-10-14
	Civil Work and Steel Structure	2028-01-14	2028-10-14
CON6490	Construction Preparation	2028-01-14	2028-02-13
CON6500	Civil Work and Steel Structure	2028-02-14	2028-09-13
CON6510	Foundation of Equipment	2028-02-14	2028-10-14
U0201	330/10.5kV Substation and Center Control Room of the Smelter	2027-05-05	2028-01-29
	Civil Work and Steel Structure	2027-05-05	2028-01-29
CON6520	Construction Preparation	2027-05-05	2027-06-03
CON6530	Foundation of Equipment	2027-06-04	2027-12-04
CON6540	Civil Work and Steel Structure	2027-06-04	2028-01-29
U0202	330/10.5kV Substation and Center Control Room of the Smelter	2028-02-14	2028-11-13
	Civil Work and Steel Structure	2028-02-14	2028-11-13
CON6550	Construction Preparation	2028-02-14	2028-03-15
CON6560	Foundation of Equipment	2028-03-16	2028-05-14
CON6570	Civil Work and Steel Structure	2028-03-16	2028-11-13
U0301	Rectifier Station	2027-03-17	2028-03-24
	Civil Work and Steel Structure	2027-03-17	2028-03-24
CON6580	Construction Preparation	2027-03-17	2027-04-15
CON6590	Civil Work and Steel Structure, and Foundation of Transformer	2027-04-16	2028-01-24
CON6600	Foundation of Other Equipment	2027-11-25	2028-03-24
U0302	Rectifier Station	2028-01-14	2029-01-03
	Civil Work and Steel Structure	2028-01-14	2029-01-03
CON6610	Construction Preparation	2028-01-14	2028-02-13
CON6620	Civil Work and Steel Structure, and Foundation of Transformer	2028-02-14	2028-10-04
CON6630	Foundation of Other Equipment	2028-08-04	2029-01-03
U05	Emergency Oil Pools and Oil Storage Facilities	2028-01-30	2028-03-15
CON6640	Civil Work	2028-01-30	2028-03-15
U0701&02	Diesel Generator Room	2028-02-03	2028-04-03
CON6650	Civil Work and Steel Structure	2028-02-03	2028-04-03
U10	Water Supply Pressurized Pump House	2027-08-14	2028-02-13
CON6660	Civil Work and Steel Structure	2027-08-14	2028-02-13
U18	Production Waste Water Treatment Station	2027-11-14	2028-04-13
CON6670	Civil Work and Steel Structure	2027-11-14	2028-04-13
U19	Domestic Waste Water Treatment Station	2028-01-14	2028-04-13
CON6680	Civil Work and Steel Structure	2028-01-14	2028-04-13
U22	Comprehensive Maintenance Workshop	2027-05-15	2027-09-08
CON6690	Civil Work and Steel Structure	2027-05-15	2027-09-08
U25	General Warehouse	2027-03-17	2027-10-04
	Civil Work and Steel Structure	2027-03-17	2027-10-04
CON6700	Construction Preparation	2027-03-17	2027-04-13
CON6710	Plant and Equipment Foundation	2027-04-14	2027-06-13
CON6720	Steel Structure/Component Assembling	2027-04-30	2027-06-29
CON6730	Steel Structure Erection	2027-05-20	2027-08-03
CON6740	Cladding of Roof and Wall, and Decoration	2027-06-20	2027-09-03
CON6750	Concrete Floor	2027-09-04	2027-10-04
U26	Process Vehicle Garage and Repair Shop	2028-01-04	2028-04-03
CON6760	Civil Work and Steel Structure	2028-01-04	2028-04-03
U00	Utilities (Rectifier Station) Installation Package (m)	2027-01-14	2029-07-18
CON6770	Installation Subcontractors Selection and Award	2027-01-14	2027-04-14
CON6780	Advance Payment	2027-04-14	2027-05-29
CON6790	Mechanical Subcontractor Mobilize on Site	2027-05-29	2027-10-26
	Mechanical and E&I Installation	2027-11-25	2029-07-18
A1201	Stem and Stub Repair Workshop	2028-09-14	2028-10-29
CON6800	Equipment Installation and Test	2028-09-14	2028-10-29
U0101	330kV Power Distribution Device	2028-02-05	2028-08-04
	Installation	2028-02-05	2028-08-04
CON6810	Installation of Incoming and Feeder Equipment	2028-02-05	2028-08-04
CON6820	No Load Test	2028-06-05	2028-08-04
U0102	330kV Power Distribution Device	2028-08-20	2029-05-19
	Installation	2028-08-20	2029-05-19
CON6830	Installation of Incoming and Feeder Equipment	2028-08-20	2029-03-19
CON6840	No Load Test	2029-03-20	2029-05-19
U0201	330/10.5kV Substation and Center Control Room of the Smelter	2027-11-30	2028-08-05
	Installation	2027-11-30	2028-08-05
CON6850	Installation of Power Transformer, Switchgear, and Others	2027-11-30	2028-06-29
CON6860	No Load Test	2028-05-25	2028-08-05
U0202	330/10.5kV Substation and Center Control Room of the Smelter	2028-09-14	2029-07-15
	Installation	2028-09-14	2029-07-15
CON6870	Installation of Power Transformer, Switchgear, and Others	2028-09-14	2029-05-24
CON6880	No Load Test	2029-05-05	2029-07-15
U0301	Rectifier Station	2027-11-25	2028-07-25

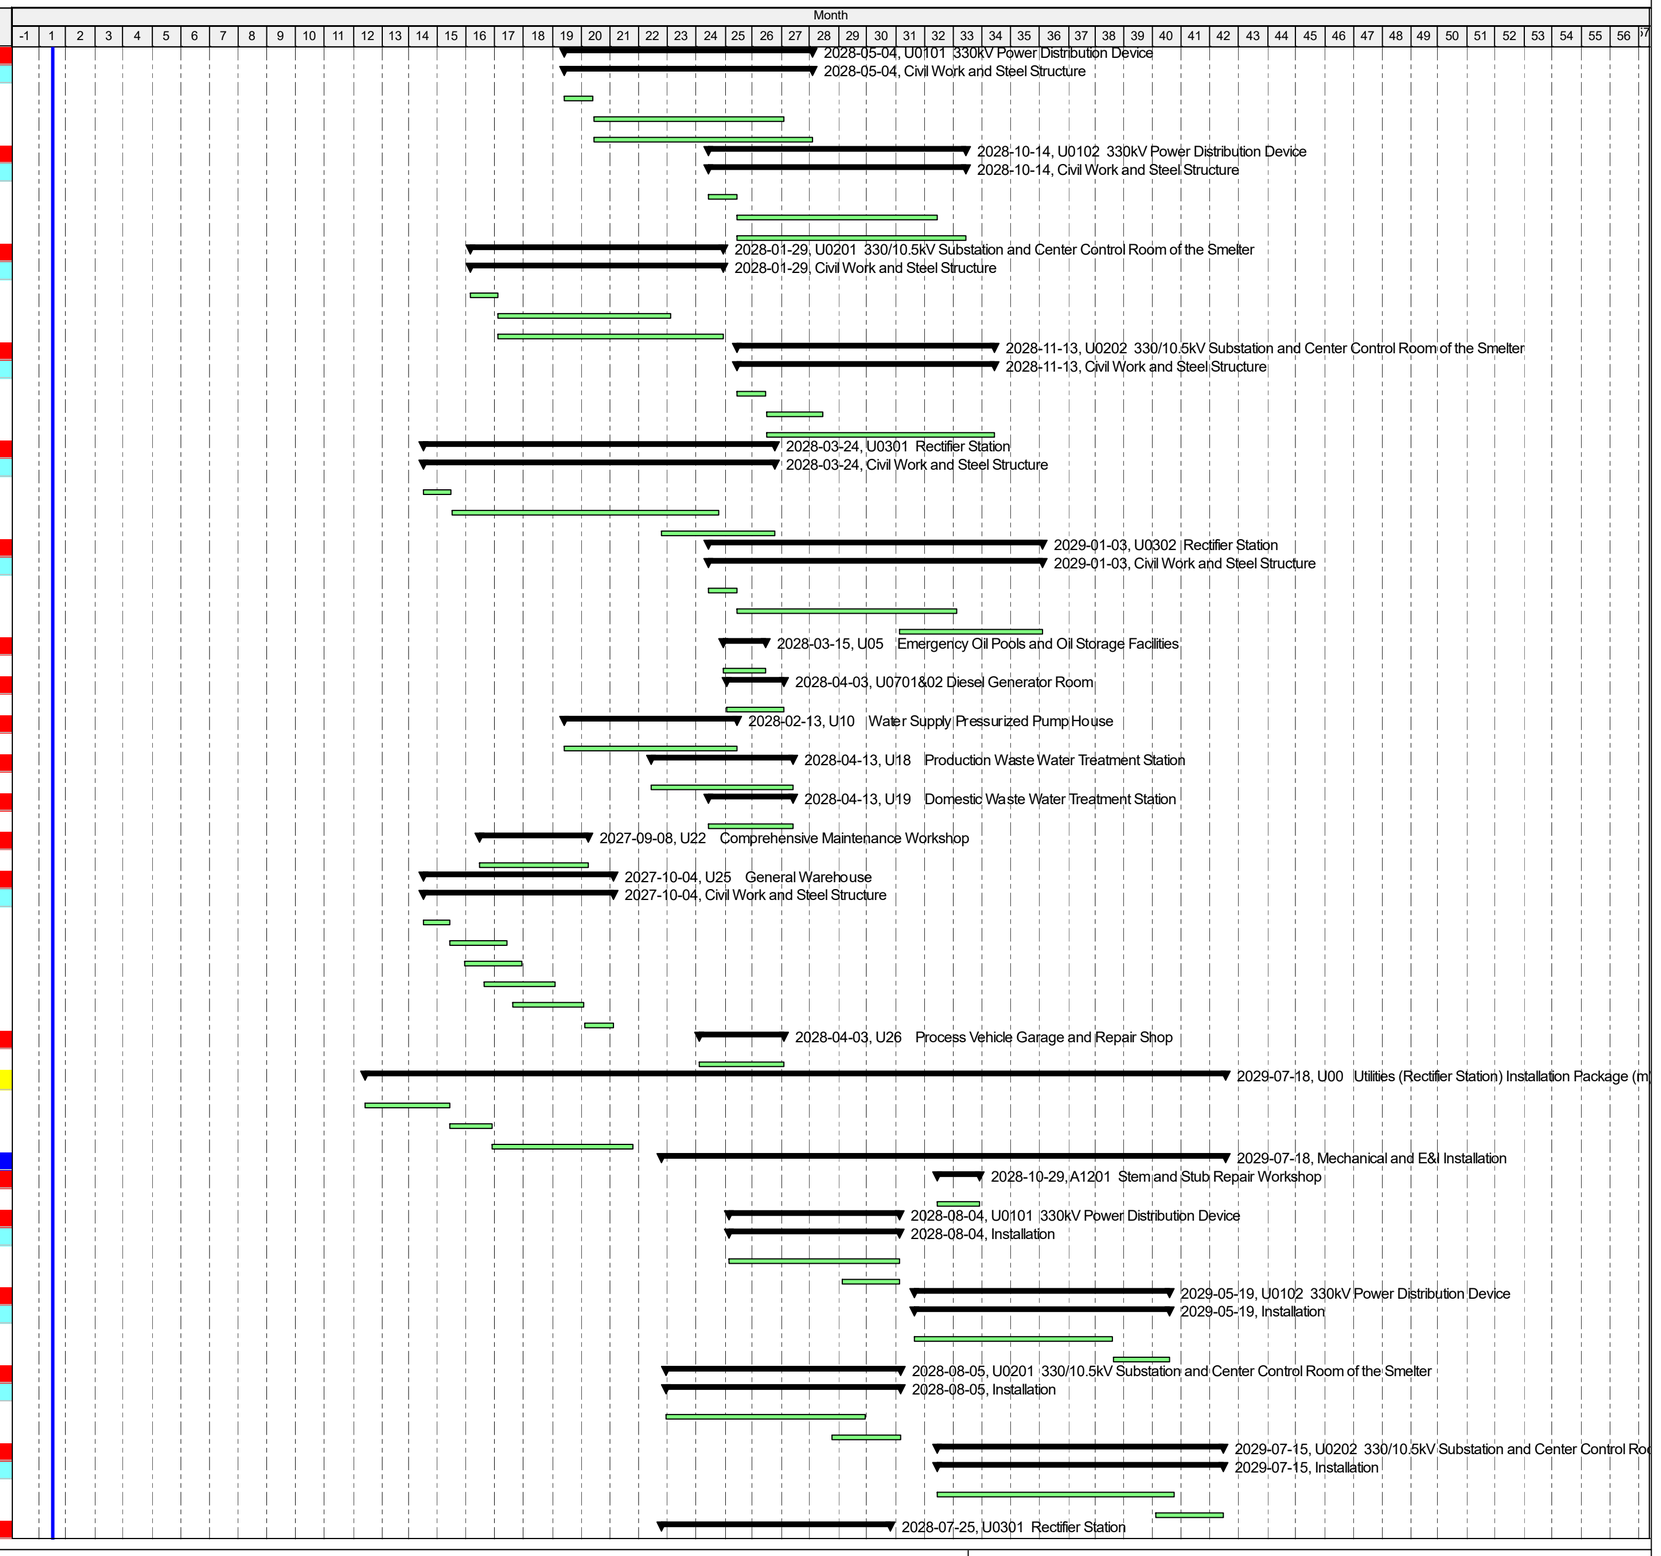

Remaining Level of Effort | Actual Work | Critical Remaining Work | summary
Actual Level of Effort | Remaining Work | Milestone

Project Schedule(Level 3)

Activity ID	Activity Name	Start	Finish
	Installation	2027-11-25	2028-07-25
CON6890	Installation of Rectifier Equipment	2027-11-25	2028-06-24
CON6900	No Load Test	2028-05-26	2028-07-25
	U0302 Rectifier Station	2028-10-05	2029-07-18
	Installation	2028-10-05	2029-07-18
CON6910	Installation of Rectifier Equipment	2028-10-05	2029-05-19
CON6920	No Load Test	2029-05-20	2029-07-18
	U06 10kV Distribution Room in Anode Area	2028-01-04	2028-07-14
CON6930	Installation of Equipment	2028-01-04	2028-04-03
CON6940	No Load Test	2028-04-04	2028-07-14
	U0701&02 Diesel Generator Room	2028-04-04	2028-04-13
CON6950	Installation of Equipment	2028-04-04	2028-04-13
	U10 Water Supply Pressurized Pump House	2028-02-14	2028-05-14
CON6960	Installation of Equipment	2028-02-14	2028-04-13
CON6970	No Load Test	2028-04-14	2028-05-14
	U18 Production Waste Water Treatment Station	2028-02-14	2028-06-13
CON6980	Installation of Equipment	2028-02-14	2028-05-14
CON6990	No Load Test	2028-05-15	2028-06-13
	U19 Domestic Waste Water Treatment Station	2028-04-14	2028-06-29
CON7000	Installation of Equipment	2028-04-14	2028-05-29
CON7010	No Load Test	2028-05-30	2028-06-29
	U22 Comprehensive Maintenance Workshop	2028-08-09	2028-11-08
CON7020	Installation and Test of Equipment	2028-08-09	2028-11-08
	U25 General Warehouse	2027-12-01	2028-01-15
	Installation	2027-12-01	2028-01-15
CON7030	Installation of Overhead Crane and Electrical Equipment	2027-12-01	2028-01-15
	U26 Process Vehicle Garage and Repair Shop	2028-08-04	2028-09-03
CON7040	Installation of Equipment	2028-08-04	2028-09-03
	U00 Utilities Civil Work (Piping)	2027-03-08	2029-03-30
	Civil Construction	2027-03-08	2029-03-30
	U31 Piping and Cable Tray Network	2027-03-08	2029-03-30
CON7050	Civil Work and Steel Structure	2027-03-08	2029-03-30
	U00 Utilities (Piping) Installation Package (n)	2027-02-13	2029-11-13
CON7060	Installation Subcontractors Selection and Award	2027-02-13	2027-05-14
CON7070	Advance Payment	2027-05-14	2027-06-28
CON7080	Mechanical Subcontractor Mobilize on Site	2027-06-28	2027-11-25
	Mechanical and E&I Installation	2027-12-25	2029-11-13
	U31 Piping and Cable Tray Network	2027-12-25	2029-11-13
CON7090	Piping	2027-12-25	2029-11-13
	U00 Utilities (Road, Drainage Ditch, and Fence) Civil Work Package (15)	2026-02-24	2029-01-18
CON7100	BOQ Preparation	2026-02-24	2026-03-16
	Package Selection and Award	2026-03-16	2026-11-20
CON7110	Bidding	2026-03-16	2026-04-15
CON7120	Contractor Evaluation	2026-04-15	2026-05-09
CON7130	Employer Evaluation and Award	2026-05-09	2026-06-08
CON7140	Advance Payment	2026-06-08	2026-07-23
CON7150	Civil Subcontractor Mobilize on Site	2026-07-23	2026-11-20
	Civil Construction	2026-12-10	2029-01-18
	U30 Plant Roadway & Vertical Planning	2026-12-10	2029-01-18
CON7160	Subgrade	2026-12-10	2028-08-29
CON7170	Pavement	2028-05-15	2029-01-18
CON7180	Rain Water Drainage Main Ditch 1	2027-04-14	2027-12-09
CON7190	Rain Water Drainage branch Ditch 1	2027-12-10	2028-06-08
CON7200	Rain Water Drainage Main Ditch 2	2028-01-29	2028-08-24
CON7210	Rain Water Drainage branch Ditch 2	2028-06-25	2028-11-24
	M00 Management and Welfare Facilities Administration and Welfare Facilities	2026-12-10	2027-09-08
	Civil Construction	2026-12-10	2027-09-08
	M06 Plant Fence, Gate and Guard Room	2026-12-10	2027-09-08
CON7220	Civil Work Zone A	2026-12-10	2027-03-11
CON7230	Civil Work Zone C	2027-03-12	2027-05-09
CON7240	Civil Work Zone D	2027-05-10	2027-07-09
CON7250	Civil Work Zone E	2027-06-09	2027-07-09
CON7260	Civil Work Zone F	2027-07-10	2027-09-08
	Commissioning	2028-08-15	2030-01-24
	Utilities Commissioning	2028-08-15	2029-12-30
COM1010	U0101 330kV Power Distribution Device Commissioning	2028-08-15	2028-10-14
COM1020	U0201 10kV Substation of the Smelter Commissioning	2028-08-15	2028-09-04
COM1030	U0201 330/10.5kV Substation and Center Control Room of the Smelter C	2028-08-16	2028-10-15
COM1040	U0301 Rectifier Station Commissioning	2028-08-16	2028-10-15
COM1050	U06 10kV Power Distribution Room in Anode Area Commissioning	2028-09-05	2028-09-19
COM1060	U09 Compressor Air Station Commissioning	2028-09-05	2028-09-29
COM1070	U10 Water Supply Pressurized Pump House Commissioning	2028-09-20	2028-09-24
COM1080	U11 Circulating Water System for Cast House Commissioning	2028-12-30	2029-01-03
COM1090	U12 Circulating Water System for Compressor Air Station Commissioning	2028-09-25	2028-09-29

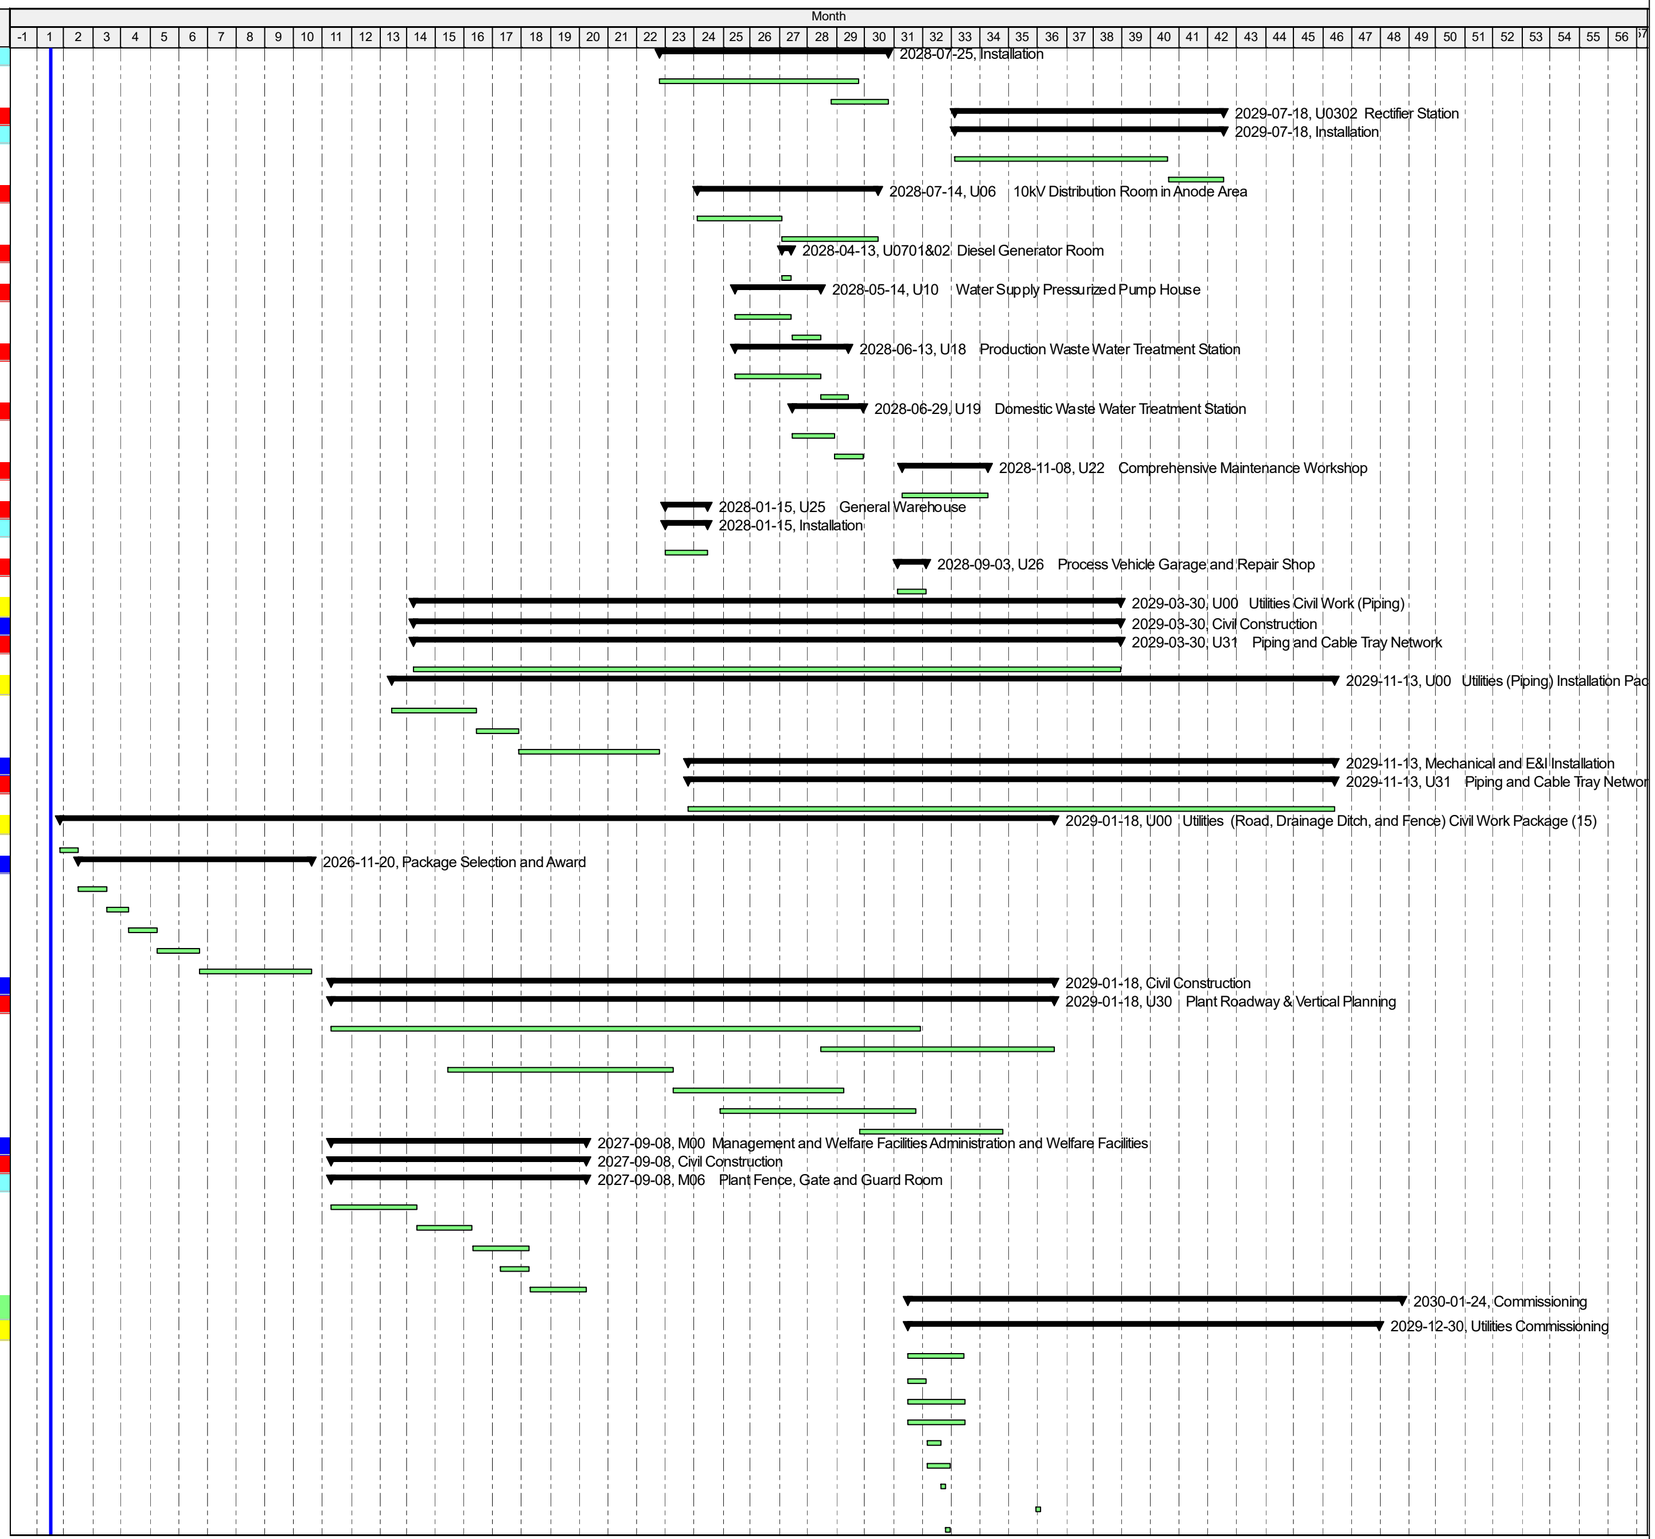

Remaining Level of Effort | Actual Work | Critical Remaining Work | summary
Actual Level of Effort | Remaining Work | Milestone

Project Schedule(Level 3)

Activity ID	Activity Name	Start	Finish
COM1100	U14 Circulating Water System for Calcination Shop Commissioning	2028-11-10	2028-11-14
COM1110	U15 Circulating Water System for Green Anode Shop Commissioning	2028-11-20	2028-11-29
COM1120	U16 Circulating Water System for Anode Rodding Shop Commissioning	2028-11-04	2028-11-08
COM1130	U33 Natural Gas Press Regulating Station Commissioning	2028-11-05	2028-12-05
COM1140	U0102 330kV Power Distribution Device Commissioning	2029-07-16	2029-09-14
COM1150	U0202 10kV Substation of the Smelter Commissioning	2029-07-16	2029-08-04
COM1160	U0202 330/11kV Substation and Center Control Room of the Smelter Cc	2029-07-16	2029-09-14
COM1170	U0302 Rectifier Station Commissioning	2029-07-19	2029-09-17
COM1180	Other Utilities Commissioning	2028-09-05	2029-12-30
External Engineering Commissioning		2028-11-14	2028-12-04
COM1190	E01 Raw Material Conveying System Commissioning	2028-11-14	2028-12-04
Management and Welfare Facilities Commissioning		2028-09-30	2028-10-20
COM1200	Management and Living Facilities Commissioning	2028-09-30	2028-10-20
Phase 1A Anode System Commissioning		2028-09-20	2029-03-29
COM1210	A01 GPC Storage and Conveying Commissioning	2028-09-25	2028-09-29
COM1220	A0201 Calcination Shop Commissioning	2028-09-20	2028-11-14
COM1230	A03 Green Anode Shop Commissioning	2028-10-20	2029-01-18
COM1240	A0401 Baking Furnace & Anode Transfer Station Commissioning	2029-02-04	2029-03-29
COM1250	A0501 Butts Treatment Commissioning	2028-11-09	2028-11-28
COM1260	A06 Solid Pitch Storage Commissioning	2028-11-09	2028-11-13
COM1270	A07 Pitch Melting Shop Commissioning	2028-11-09	2028-11-29
COM1280	A08 Baking Furnace Fume Treatment Center (Phase 1A) Commissionin	2028-12-05	2029-02-03
COM1290	A09 Calcination Fume Treatment Center Commissioning	2028-10-10	2028-12-09
COM1300	A1001 Anode Rodding Shop Commissioning	2028-10-15	2029-01-03
COM1310	A1101 Bath Treatment System Commissioning	2028-12-15	2029-01-03
COM1320	A13 Waste Heat Boiler Room Commissioning	2028-10-20	2028-12-04
COM1330	A14 Heat Transfer Medium Boiler and Pump Room Commissioning	2028-11-04	2028-12-09
Phase 1B Anode System Commissioning		2029-04-09	2029-10-20
COM1340	A0202 Calcination Shop Commissioning	2029-04-09	2029-06-03
COM1350	A0402 Baking Furnace & Anode Transfer Station Commissioning	2029-08-14	2029-10-04
COM1360	A08 Baking Furnace Fume Treatment Center (Phase 1B) Commissionin	2029-07-20	2029-10-04
COM1370	A1002 Anode Rodding Shop Commissioning	2029-08-05	2029-10-20
Phase 1A Reduction System Commissioning		2028-09-05	2029-03-24
COM1380	S0101 Loading Test of Anode Transfer Frame	2028-10-05	2029-01-04
COM1390	S0101 Test of Pot Control System & Equipment	2028-10-05	2029-01-04
COM1400	S0101 Test of Insulation	2028-10-15	2029-01-19
COM1410	S0101 Feeding Test	2029-01-05	2029-02-24
COM1420	S0101 Busbar System Test	2029-01-20	2029-02-09
COM1430	S0201 Potline Gas Treatment Center Commissioning	2028-09-05	2028-12-20
COM1440	S03 Alumina Storage Commissioning	2028-11-09	2028-11-29
COM1450	S0401 Alumina Conveying System and Daily Silo Commissioning	2028-11-09	2028-11-29
COM1460	S05 Fluoride Storage Commissioning	2028-12-05	2028-12-19
COM1470	S0601 Super Dense Phase Conveying System Commissioning	2028-11-15	2028-12-30
COM1480	S08 Cast House Commissioning	2029-01-20	2029-03-24
Phase 1B Reduction System Commissioning		2029-08-05	2030-01-24
COM1490	S0102 Loading Test of Anode Transfer Frame by Temporary Power Sourc	2029-09-04	2029-12-05
COM1500	S0102 Test of pot control system & Equipment by Temporary Power Sourc	2029-09-04	2029-12-05
COM1510	S0102 Test of insulation	2029-09-14	2029-12-20
COM1520	S0102 Feeding Test	2029-12-05	2030-01-24
COM1530	S0102 Busbar System Test	2029-12-21	2030-01-09
COM1540	S0202 Potline Gas Treatment Center Commissioning	2029-08-05	2029-11-19
COM1550	S0402 Alumina Conveying System and Daily Silo Commissioning	2029-09-04	2029-09-24
COM1560	S0602 Super Dense Phase Conveying System Commissioning	2029-10-15	2029-11-29
Trial Operation		2028-09-05	2030-08-12
Utilities Trial Operation		2028-09-05	2029-12-15
TO1010	U0101 330kV Power Distribution Device Trial Operation	2028-10-15	2028-11-04
TO1020	U0201 10.5kV Substation of the Smelter Trial Operation	2028-09-05	2028-09-24
TO1030	U0201 330/10.5kV Substation and Center Control Room of the Smelter	2028-10-16	2028-11-05
TO1040	U0301 Rectifier Station Trial Operation	2028-10-16	2028-11-05
TO1050	U06 10kV Power Distribution Room in Anode Area Trial Operation	2028-09-20	2028-09-24
TO1060	U09 Compressor Air Station (Phase 1A) Trial Operation	2028-10-03	2028-10-20
TO1070	U09 Compressor Air Station (Phase 1B) Trial Operation	2029-10-21	2029-10-25
TO1080	U10 Water Supply Pressurized Pump House Trial Operation	2028-09-25	2028-09-29
TO1090	U11 Circulating Water System for Cast House Trial Operation	2029-04-03	2029-04-07
TO1100	U12 Circulating Water System for Compressor Air Station Trial Operatio	2028-09-30	2028-10-02
TO1110	U14 Circulating Water System for Calcination Shop Trial Operation	2028-12-05	2028-12-10
TO1120	U15 Circulating Water System for Green Anode Shop Trial Operation	2029-02-10	2029-02-20
TO1130	U16 Circulating Water System for Anode Rodding Shop Trial Operation	2028-12-29	2029-01-03
TO1140	U33 Natural Gas Press Regulating Station Trial Operation	2028-12-06	2028-12-11

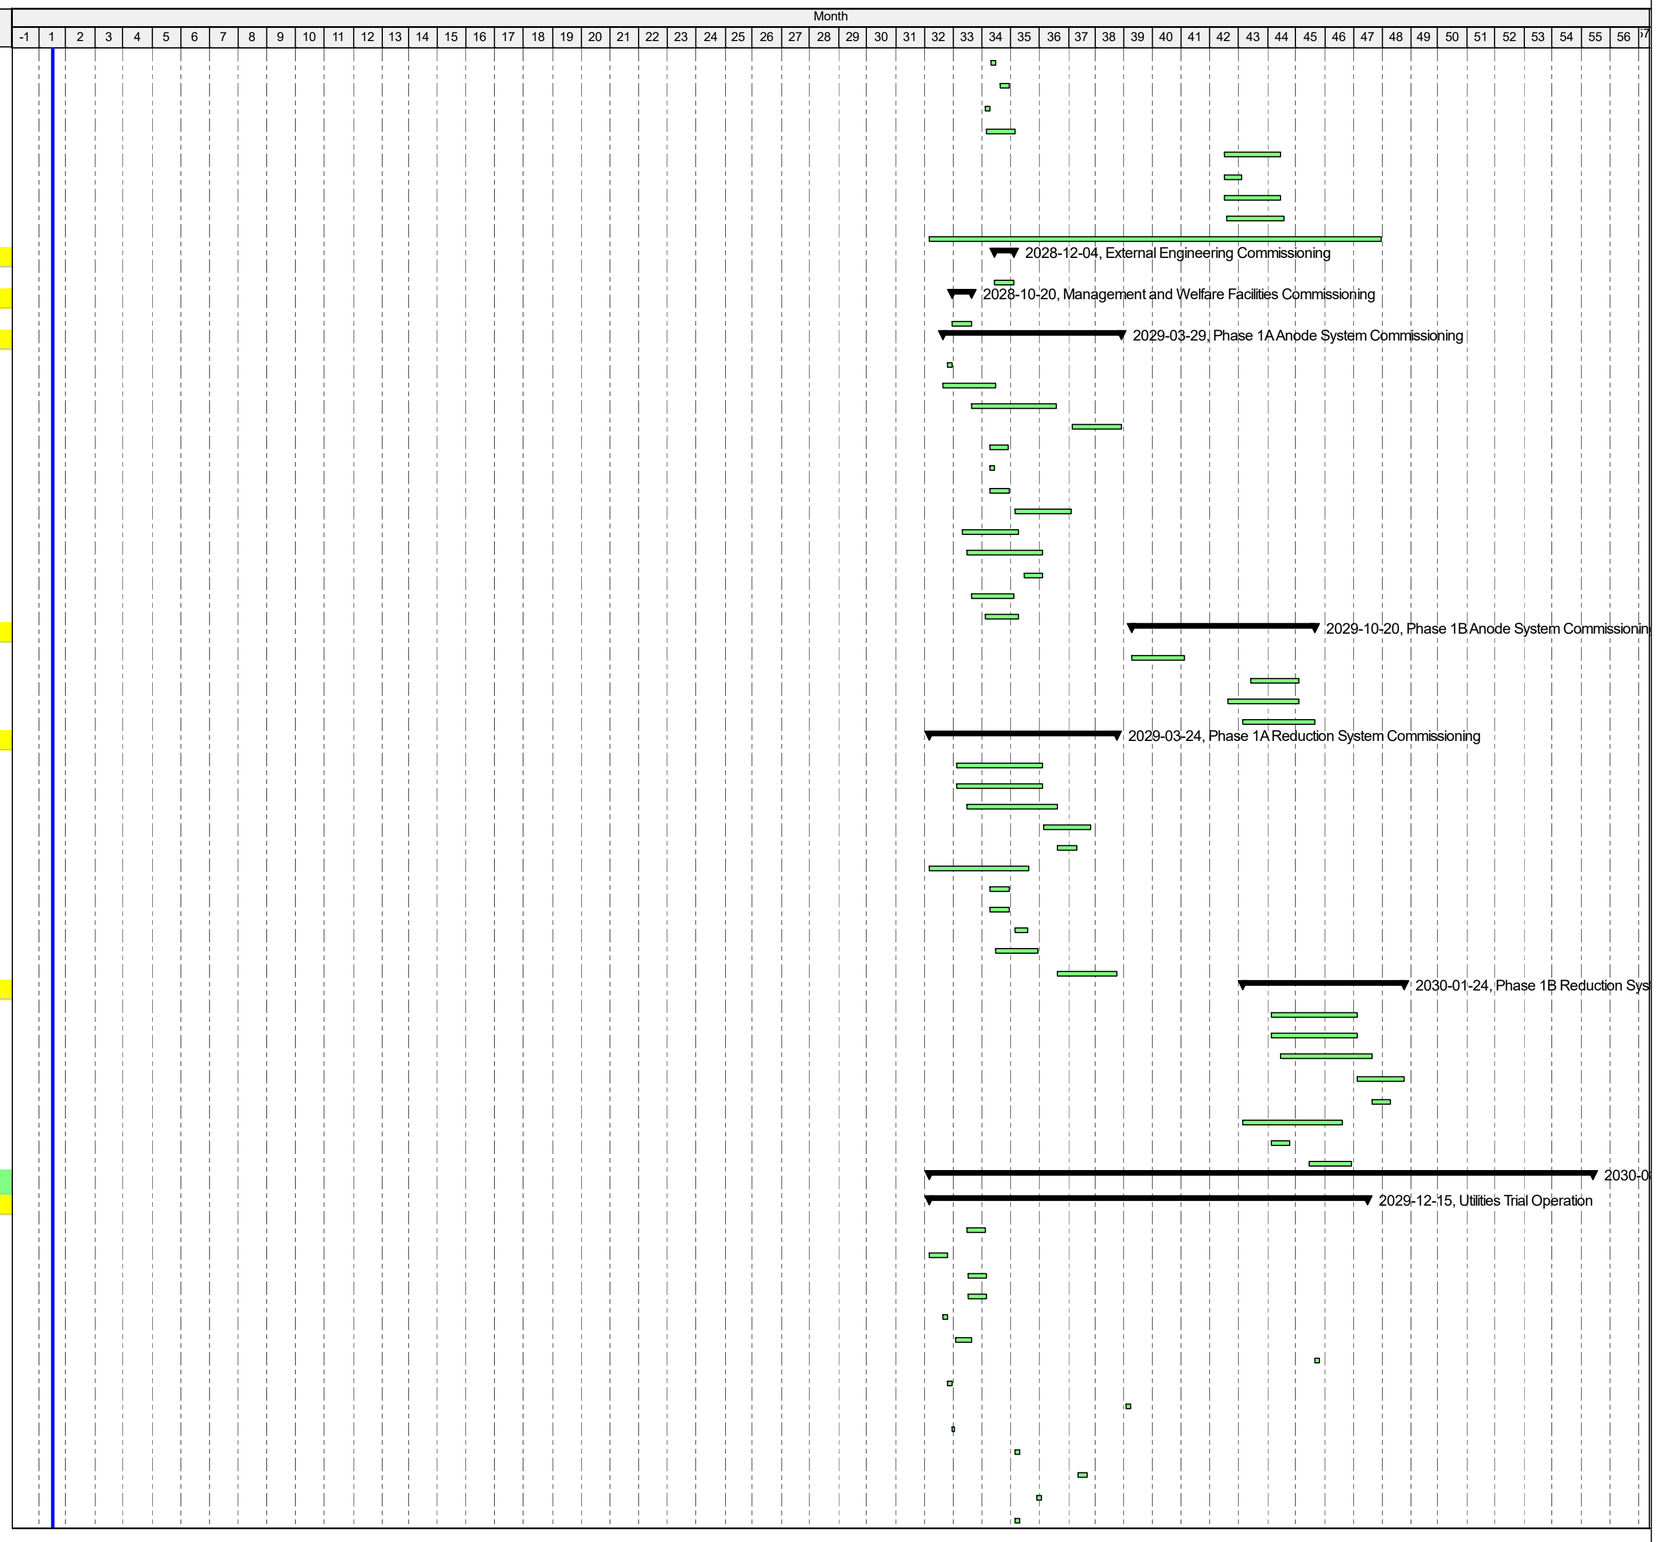

Remaining Level of Effort | Actual Work | Critical Remaining Work | summary
Actual Level of Effort | Remaining Work | Milestone

Project Schedule(Level 3)

Activity ID	Activity Name	Start	Finish
TO1150	U0102 330kV Power Distribution Device Trial Operation	2029-09-15	2029-09-29
TO1160	U0202 10kV Substation of the Smelter Trial Operation	2029-08-05	2029-08-24
TO1170	U0202 330/10kV Substation and Center Control Room of the Smelter Tri	2029-09-15	2029-09-29
TO1180	U0302 Rectifier Station Trial Operation	2029-09-18	2029-10-02
TO1190	Other Utilities Trial Operation	2029-10-26	2029-12-15
Phase 1A Anode System Trial Operation		2028-12-01	2029-05-30
TO1200	A01 GPC Storage and Conveying Trial Operation	2028-12-01	2028-12-15
TO1210	A0201 Calcination Shop Trial Operation	2028-12-11	2029-02-19
TO1220	A03 Green Anode Shop Trial Operation	2029-02-21	2029-03-30
TO1230	A0401 Baking Furnace & Anode Transfer Station Trial Operation	2029-03-31	2029-05-30
TO1240	A0501 Butts Treatment Trial Operation	2029-01-04	2029-01-29
TO1250	A06 Solid Pitch Storage Trial Operation	2029-01-05	2029-01-09
TO1260	A07 Pitch Melting Shop Trial Operation	2029-01-05	2029-02-19
TO1270	A08 Baking Furnace Fume Treatment Center (Phase 1A) Trial Operatic	2029-03-31	2029-05-30
TO1280	A09 Calcination Fume Treatment Center Trial Operation	2028-12-11	2029-02-08
TO1290	A1001 Anode Rodding Shop Trial Operation	2029-01-04	2029-02-03
TO1300	A13 Waste Heat Boiler Room Trial Operation	2028-12-11	2029-01-30
TO1310	A14 Heat Transfer Medium Boiler and Pump Room Trial Operation	2028-12-11	2029-01-30
Phase 1B Anode System Trial Operation		2029-06-04	2029-12-04
TO1320	A0202 Calcination Shop Trial Operation	2029-06-04	2029-08-13
TO1330	A0402 Baking Furnace & Anode Transfer Station Trial Operation	2029-10-05	2029-12-04
TO1340	A08 Baking Furnace Fume Treatment Center (Phase 1B) Trial Operati	2029-10-05	2029-11-03
TO1350	A1002 Anode Rodding Shop Trial Operation Trial Operation	2029-10-21	2029-11-09
Phase 1A Reduction System Trial Operation		2028-12-05	2030-02-14
TO1360	E01 & S05 Trial Operation	2028-12-05	2028-12-09
TO1370	S03 Alumina Storage Trial Operation	2028-12-07	2028-12-11
TO1380	S0201 Potline Gas Treatment Center & U13 Trial Operation	2028-12-21	2029-04-24
TO1390	S0401 Alumina Conveying System and Daily Silo Trial Operation	2028-12-12	2028-12-20
TO1400	S0601 Super Dense Phase Conveying System Trial Operation	2028-12-31	2029-02-24
TO1410	S08 Cast House Trial Operation	2029-04-06	2029-04-10
TO1420	Phase 1A Pots Baking and Start-up	2029-04-01	2029-11-14*
TO1430	Fine Tune	2029-11-15	2030-02-14
Phase 1B Reduction System Trial Operation		2029-10-25	2030-08-12
TO1440	S0202 Potline Gas Treatment Center & U13 Trial Operation	2029-11-20	2030-03-24
TO1450	S0402 Alumina Conveying System and Daily Silo Trial Operation	2029-10-25	2029-11-14
TO1460	S0602 Super Dense Phase Conveying System Trial Operation	2029-11-30	2030-01-24
TO1470	Phase 1B Pots Baking and Start-up	2030-02-11	2030-08-12*

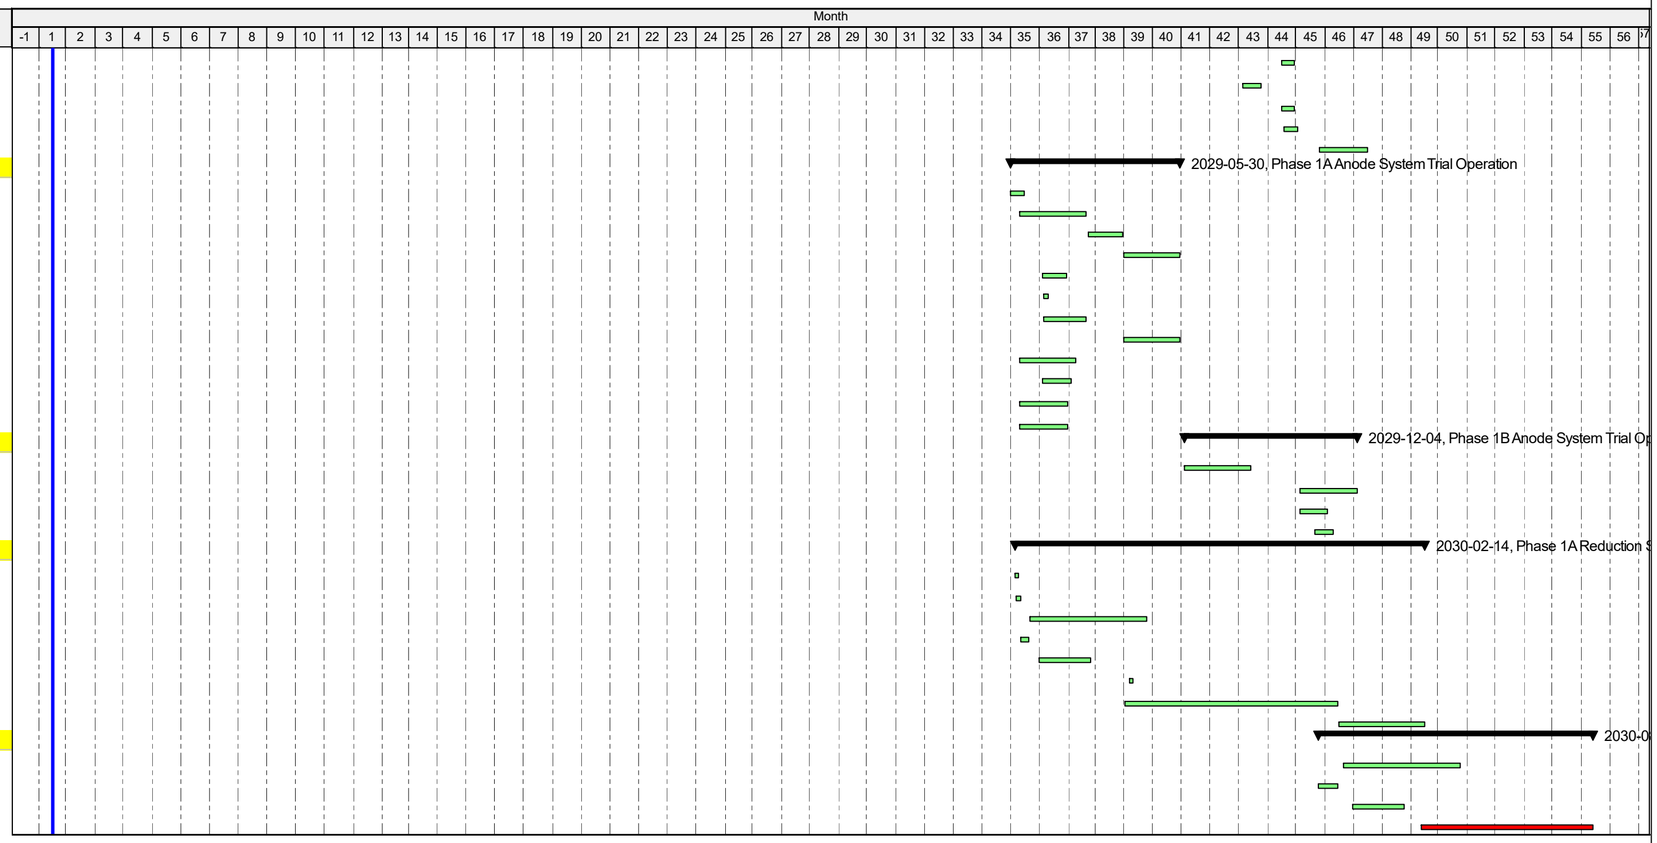

Remaining Level of Effort
Actual Work
Critical Remaining Work
summary
Actual Level of Effort
Remaining Work
Milestone